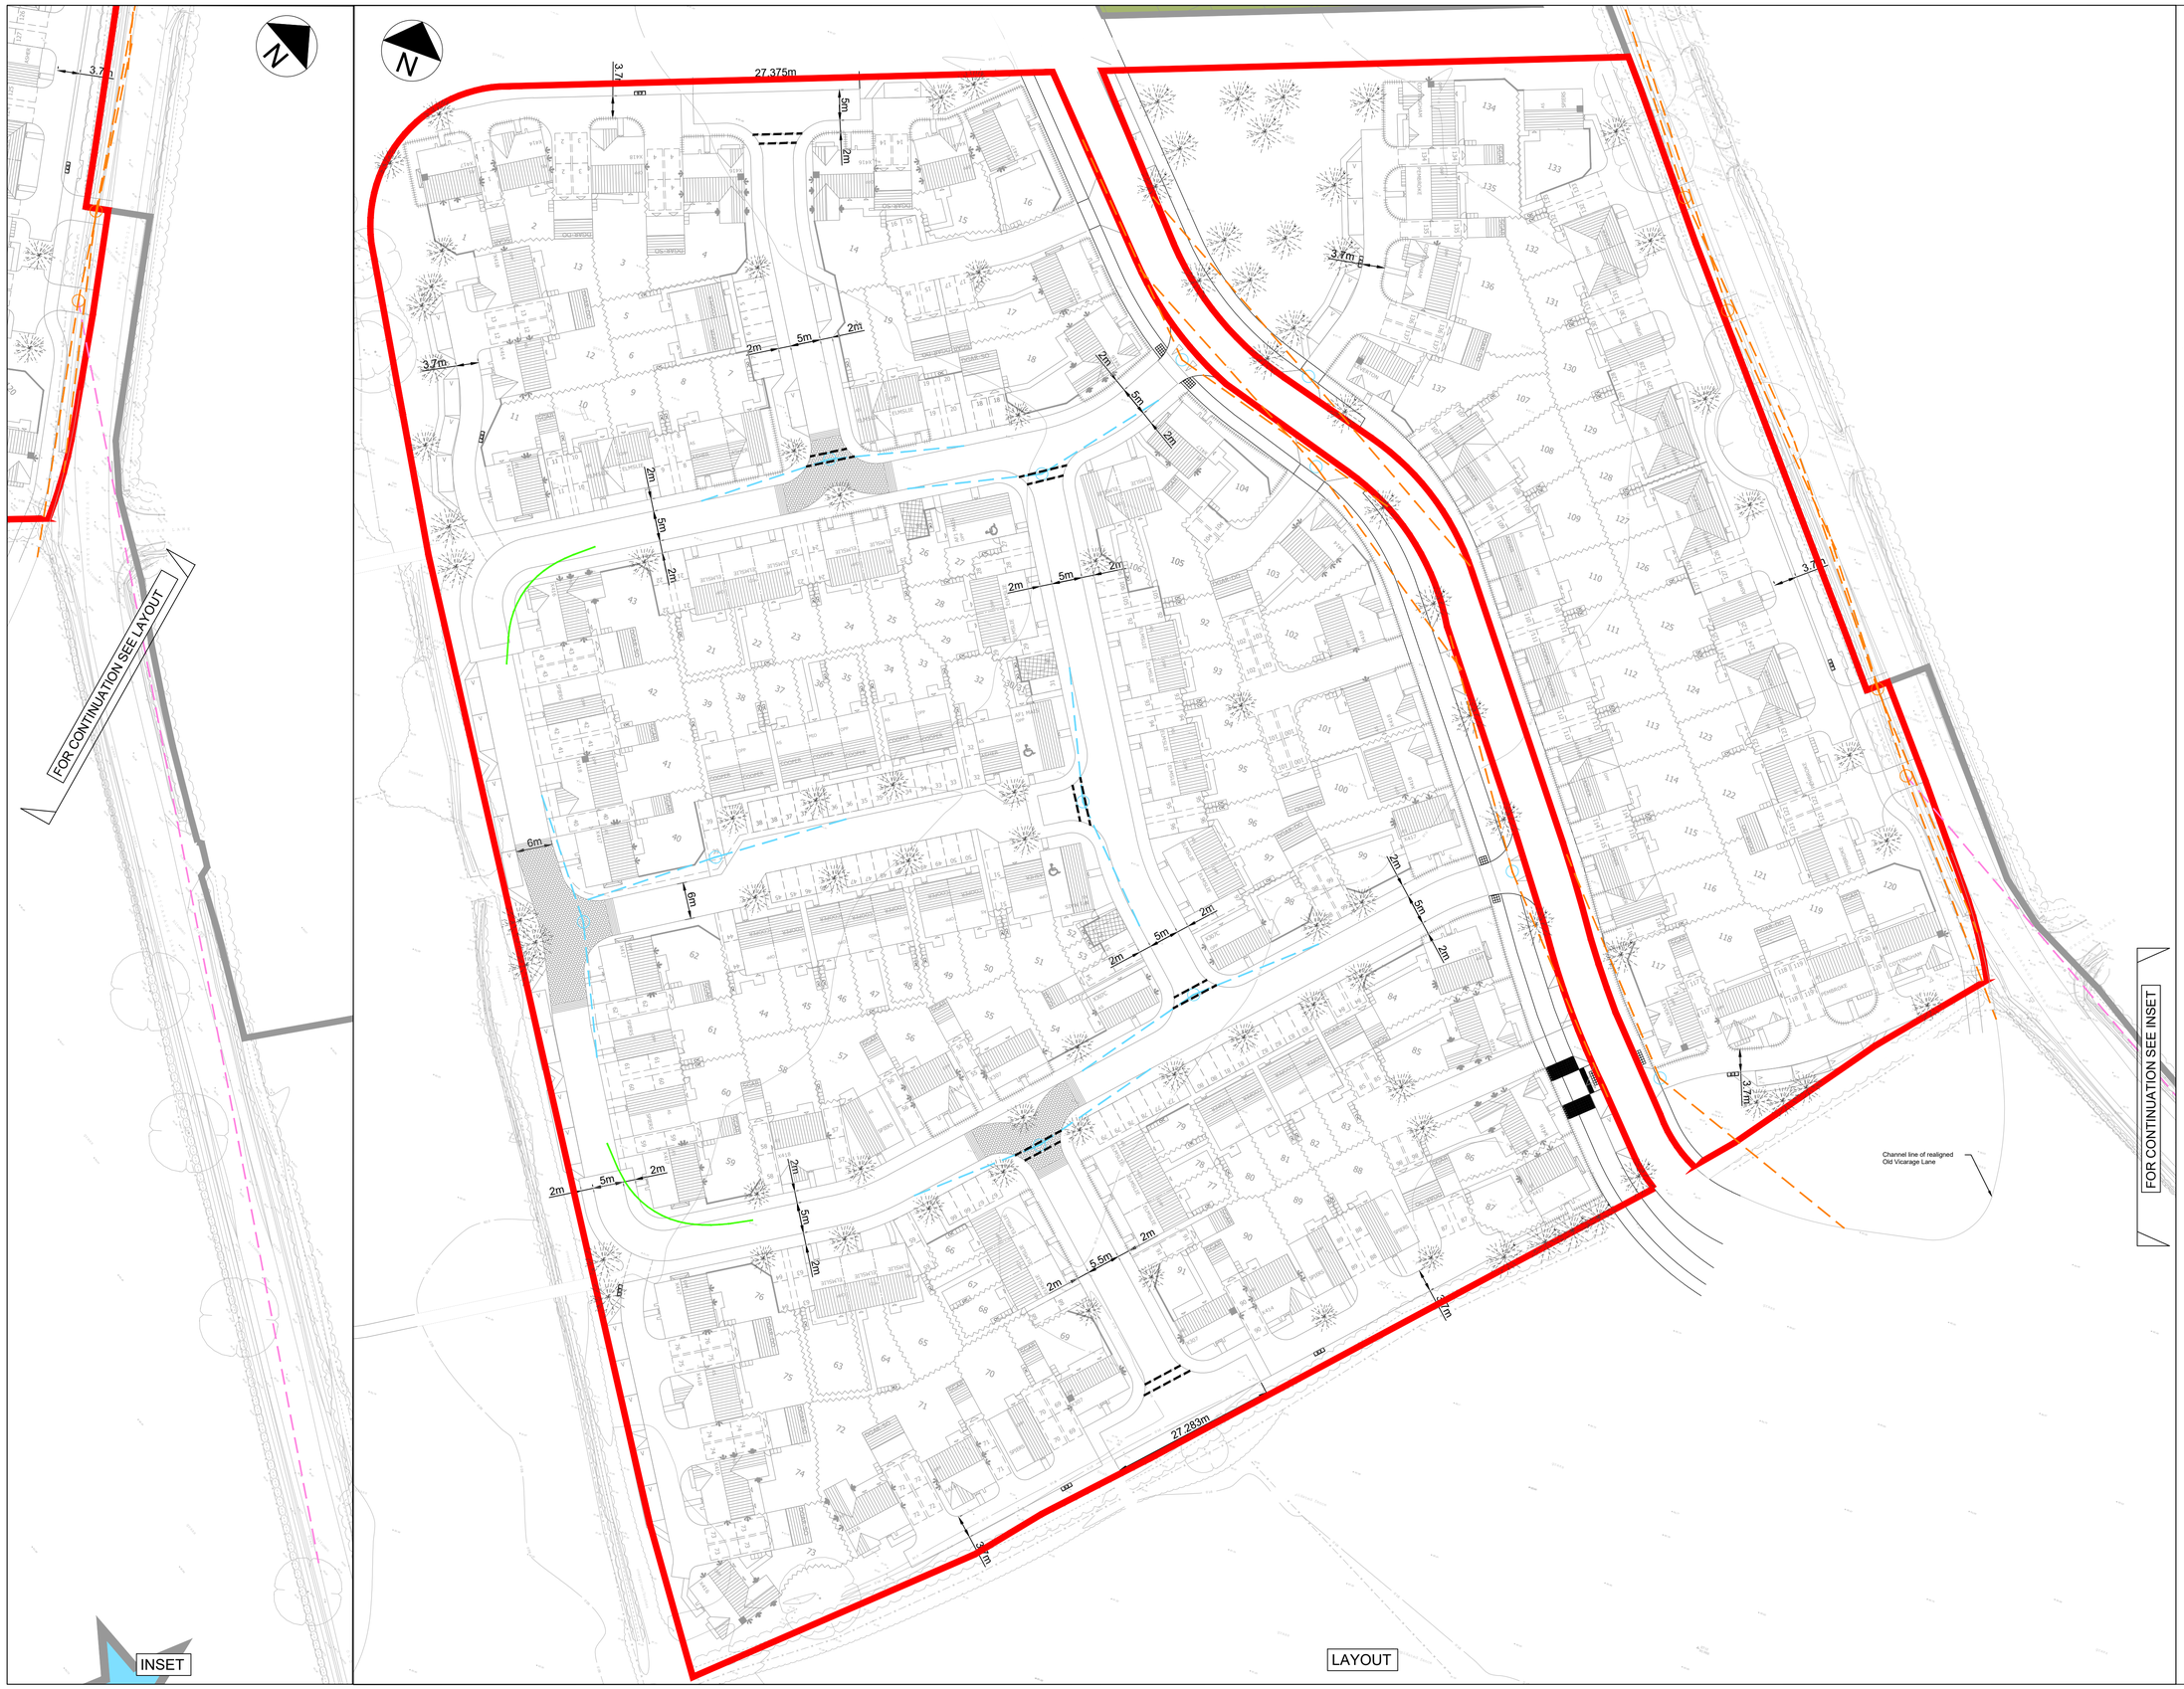

Notes:

1. Do not scale from this drawing. All dimensions are in metres, unless stated otherwise.
2. This drawing is based on the Architect's layout.
3. Ordnance Survey, (c) Crown Copyright 2023. All rights reserved. Licence number 100022432.
4. Drawing to be read in conjunction with all other drawings. Any discrepancies are to be reported to the engineer 5 working days in advance of undertaking any work.
5. Any land over visibility to be safeguarded, offered for adoption and maintained as public highway as part of the S278 / S38. Vegetation will be maintained below 600mm total height.

Key:

- 2.4x22m visibility splay. As per Table 7.1 of Manual for Streets for 20mph road
- 2.4x43m visibility splay. As per Table 7.1 of Manual for Streets for 30mph road
- 2.4x210m visibility splay in accordance with DMRB
- Forward visibility splay for 15mph road.

Rev	Date	Details	By	Chkd
P03	07.11.24	Updated to suit new layout	EB	JB
P02	11.10.24	Amended following masterplan updates	RH	RS
P01	01.08.24	First Issue	LB	RS

rappor

rappor.co.uk

CLIENT:
Vistry Homes Ltd.

PROJECT:
Woodlands
South Marston

TITLE:
Highway Layout

SCALE @ A1:	DATE:	DRAWN:	CHECKED:	APPROVED:
1:500	01.08.24	LB	RS	RS

STATUS: PLANNING

DRAWING NO: 240616-RAP-XX-XX-DR-C-0101

REVISION: P03

RESERVED COPYRIGHT