Original Drawing Size A1

KEY:

PROPOSED LEVEL

EXISTING GROUND LEVEL

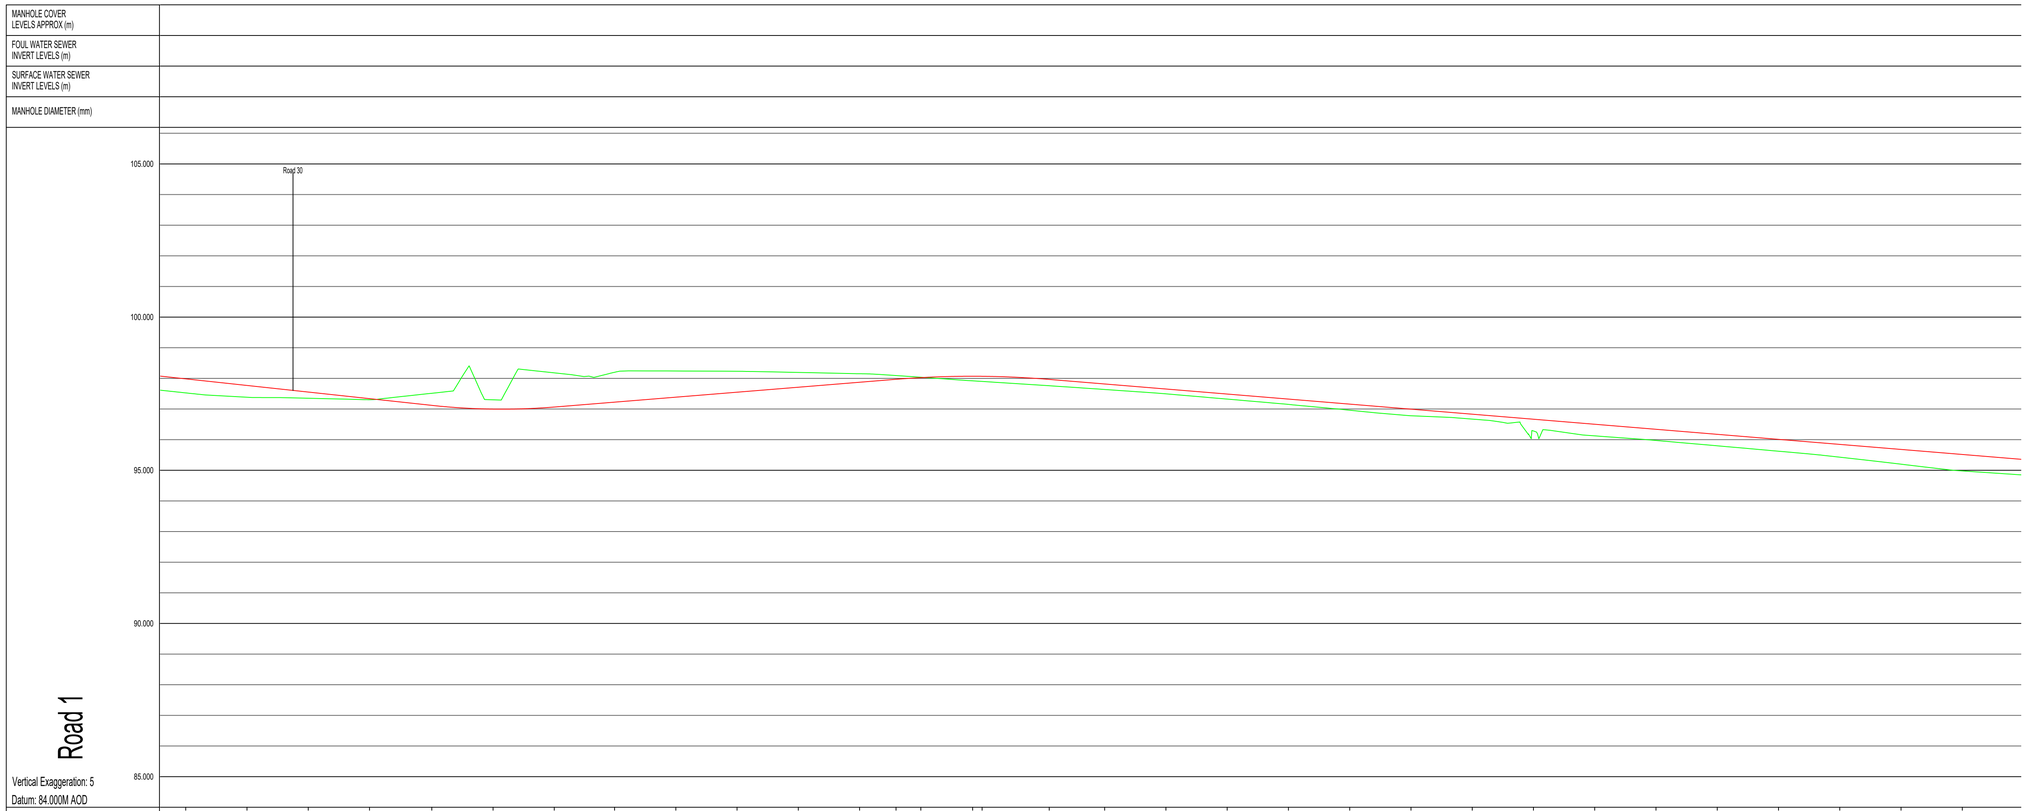

MANHOLE COVER LEVELS APPROX (m)	
FOUL WATER SEWER INVERT LEVELS (m)	
SURFACE WATER SEWER INVERT LEVELS (m)	
MANHOLE DIAMETER (mm)	
CHAINAGE ON CENTRELINE (m)	260.000, 270.000, 280.000, 290.000, 300.187, 310.187, 320.187, 330.000, 340.000, 350.000, 360.000, 370.000, 375.548, 380.000, 388.448, 390.000, 400.548, 410.000, 420.000, 430.000, 440.000, 450.000, 460.000, 470.000, 480.000, 490.000, 500.000, 510.000, 520.000, 530.000, 540.000, 550.000
LEVELS ON LEFT HAND CHANNEL (m)	97.000, 97.085, 97.489, 97.253, 97.054, 96.913, 96.861, 97.140, 97.302, 97.464, 97.626, 97.789, 97.885, 97.940, 97.985, 97.984, 97.882, 97.733, 97.589, 97.465, 97.240, 97.076, 96.912, 96.747, 96.583, 96.419, 96.254, 96.090, 95.925, 95.761, 95.597, 95.432, - - -
LEVELS ON RIGHT HAND CHANNEL (m)	97.300, 97.085, 97.489, 97.253, 97.054, 96.913, 96.861, 97.140, 97.302, 97.464, 97.626, 97.789, 97.885, 97.940, 97.984, 97.984, 97.882, 97.733, 97.589, 97.465, 97.240, 97.076, 96.912, 96.747, 96.583, 96.419, 96.254, 96.090, 95.925, 95.761, 95.597, 95.432, - - -
VERTICAL DESIGN ON CARRIAGEWAY CENTRELINE	SAG CURVE R = 529.537 L = 20.000; GRADIENT 1.6% (1 in 62) LENGTH = 55.78 m; HOG CURVE R = 765.758 L = 25.000
HORIZONTAL DESIGN ON CARRIAGEWAY CENTRELINE	CURVE R = 360.000 L = 128.638; CURVE R = 120.000 L = 107.662
EXISTING LEVELS (m)	97.526, 97.384, 97.302, 97.303, 97.214, 97.300, 96.161, 96.199, 96.241, 96.222, 96.194, 96.152, 96.092, 96.037, 97.010, 97.003, 97.760, 97.658, 97.495, 97.324, 97.150, 96.961, 96.779, 96.671, 96.203, 96.123, 95.974, 95.799, 95.622, 95.438, 95.199, 94.979, - - -

NOTES:

1. Do not scale from this drawing.
2. All dimensions are in metres unless otherwise stated.
3. Brookbanks consulting ltd has prepared this drawing for the sole use of the client. the drawing may not be relied upon by any other party without the express agreement of the client and Brookbanks consulting ltd. where any data supplied by the client or from other sources has been used, it has been assumed that the information is correct. no responsibility can be accepted by Brookbanks consulting ltd for inaccuracies in the data supplied by any other party. the drawing has been produced based on the assumption that all relevant information has been supplied by those bodies from whom it was requested.
4. No part of this drawing may be copied or duplicated without the express permission of Brookbanks consulting ltd.
5. All dimensions and all levels in metres unless noted otherwise.
6. Any discrepancies noted on site are to be reported to the engineer immediately.
7. Section 278 agreement highway works to carried out in strict accordance with Swindon Borough council's requirements.
8. All works within existing public highway, including any temporary works or traffic management measures, are subject to the approval of Swindon Borough Council. when works are required on the public highway, the contractor shall liaise with and obtain all statutory approvals from Swindon Borough Council, before commencing these works. these approvals include, but are not limited to, approval of traffic management measures, issue of works commencement notices, road opening notices, temporary traffic regulation orders etc.
9. All traffic management shall comply with the requirements as set out in chapter 8 of the traffic signs manual. warning signs may be erected outside the indicated boundaries. any obstructions to traffic or pedestrians shall be properly signed and protected with barriers, cones, signs, and lamps.
10. All planting in visibility splays to be agreed and approved by Swindon Borough Council and in all cases no planting to be above 600mm in height above the carriageway. also no obstructions of any kind within the visibility splay areas.
11. All tactile areas to be laid in accordance with detr "guidance on the use of tactile paving surfaces".
12. All traffic signs and road markings are to be in accordance with the 'Traffic Signs Regulations and General Directions 2016'.
13. Any damage caused to existing footways, roads or other third party property to be made good to the county engineers requirements.
14. Temporary works associated with the construction of the works shall be the responsibility of the contractor.

F	Revised with latest long sections for tender	CDW	CM	SM	11.02.25
E	Updated following SBC highways comments	CDW	CM	SM	08.01.25
D	Updated following TW comment 12/04	MA	CM	SM	03.05.24
C	Long-sections updated	MA	CM	SM	09.04.24
B	Key added to long-sections	CM	CM	SM	08.02.23
A	Updated to include under-drained swales	CM	CM	SM	16.01.23
-	First Issue	CM	SM	SM	12.12.22

BROOKBANKS

6150 Knights Court, Solihull Parkway, Birmingham, B37 7WY
T +44 (0)203 958 5400 E mail@brookbanks.com
W brookbanks.com

Swindon EDA Consortium

Proposed Development
Swindon EV

South Marston Primary Street
Long-section Sheet 2 of 5

Status		Status Date
Approval		Dec' 2022
Drawn	Checked	Date
CM	SM	12.12.2022
Scale	Number	Rev
1:500	1335-SMPS-800-104	F

0 10 20 30 40 50
METRES

UNTIL TECHNICAL APPROVAL HAS BEEN OBTAINED FROM THE RELEVANT LOCAL AUTHORITIES, IT SHOULD BE UNDERSTOOD THAT ALL DRAWINGS ARE ISSUED AS PRELIMINARY AND NOT FOR CONSTRUCTION. SHOULD THE CONTRACTOR COMMENCE SITE WORK PRIOR TO APPROVAL BEING GIVEN, IT IS ENTIRELY AT HIS OWN RISK.

© Brookbanks Consulting Limited 2025

P:\1335\CAD\BCL\Current Drawings\S38- South Marston Primary Street\1335-SMPS-800-103F-107F South Marston Primary Street Long-Section 1-500.dwg