1335-DR-04

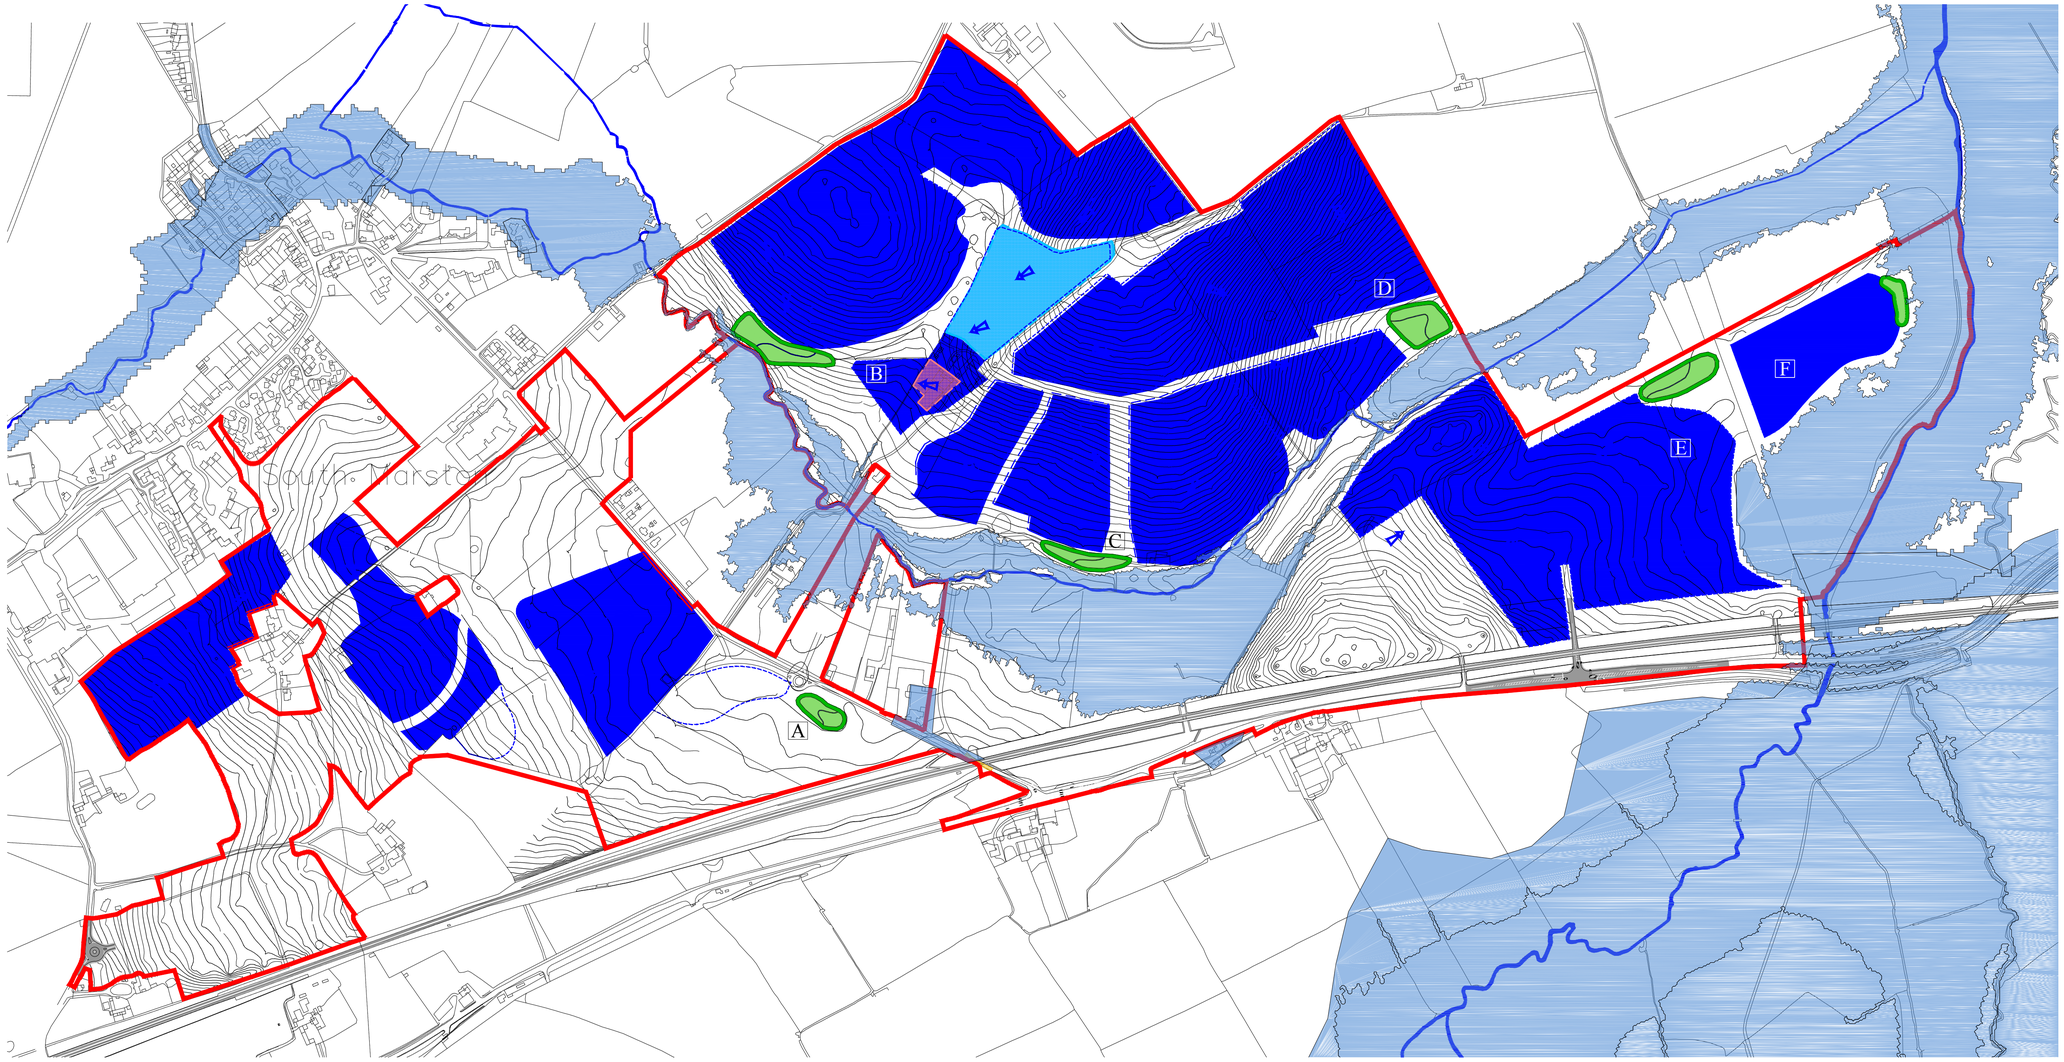

Notes:

1) Do not scale from this drawing.
2) The Data contained within this survey has been collected by a third party. Brookbanks Consulting Ltd accept no responsibility for the accuracy of this data.
3) The locations of the features shown on this plan are conceptual and subject to amendments during detailed design.

KEY

- Site Boundary
- River Cole
- South Marston Brook
- Tertiary Catchment
- Tertiary Catchment Label
- Proposed Storage Basin
- EA Flood Zone 2

N

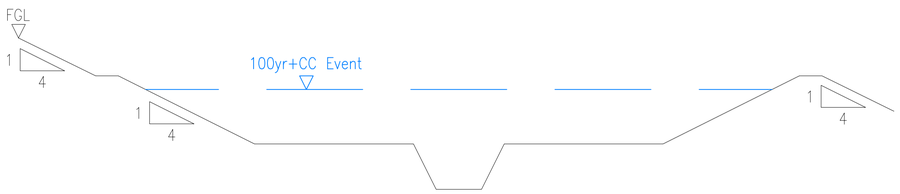

ILLUSTRATIVE ATTENUATION BASIN SECTION

Catchment	Impermeable Area (ha)	1 in 100 Year Run-off (l/s)	Detention Volume (m3)
A	6.94	24.60	2,061
B	8.80	40.40	4,475
C	4.49	32.10	2,687
D	5.99	29.40	3,945
E	7.80	29.50	3,975
F	1.63	7.10	1,074
Total Storage Volume			18217

Rev.	Revision Details	Drawn	Checked	Approved	Date
C	Includes Flood extent	SO	NO	PAB	06.9.17
C	Amended red line boundary and pond added.	JI	NO	PAB	19.1.17
B	Changed red line boundary	SO	DS	DS	10/15

Issue Status	Approved	Date
PRELIMINARY	PAB	03.04.13

Drawn CA Checked DW Date APR 13

Brookbanks Consulting

6150 Knights Court Solihull Parkway Birmingham B37 7WY
Tel (0121) 329 4330 Fax (0121) 329 4331
www.brookbanks.com

Swindon eDA Consortium

Proposed Development
Swindon EV Phase 1

Conceptual Drainage Plan
Sheet 3 of 3

0 100 200 300 400 500
METRES

Original Drawing Size A1

© Brookbanks Consulting Limited 2015

Scale at A1	Drawing No.	Rev.
1:5,000	1335-DR-04	D