This drawing is the property of FPCR Environment and Design Ltd and is issued on the condition it is not reproduced, retained or disclosed to any unauthorised person, either wholly or in part without written consent of FPCR Environment and Design Ltd.

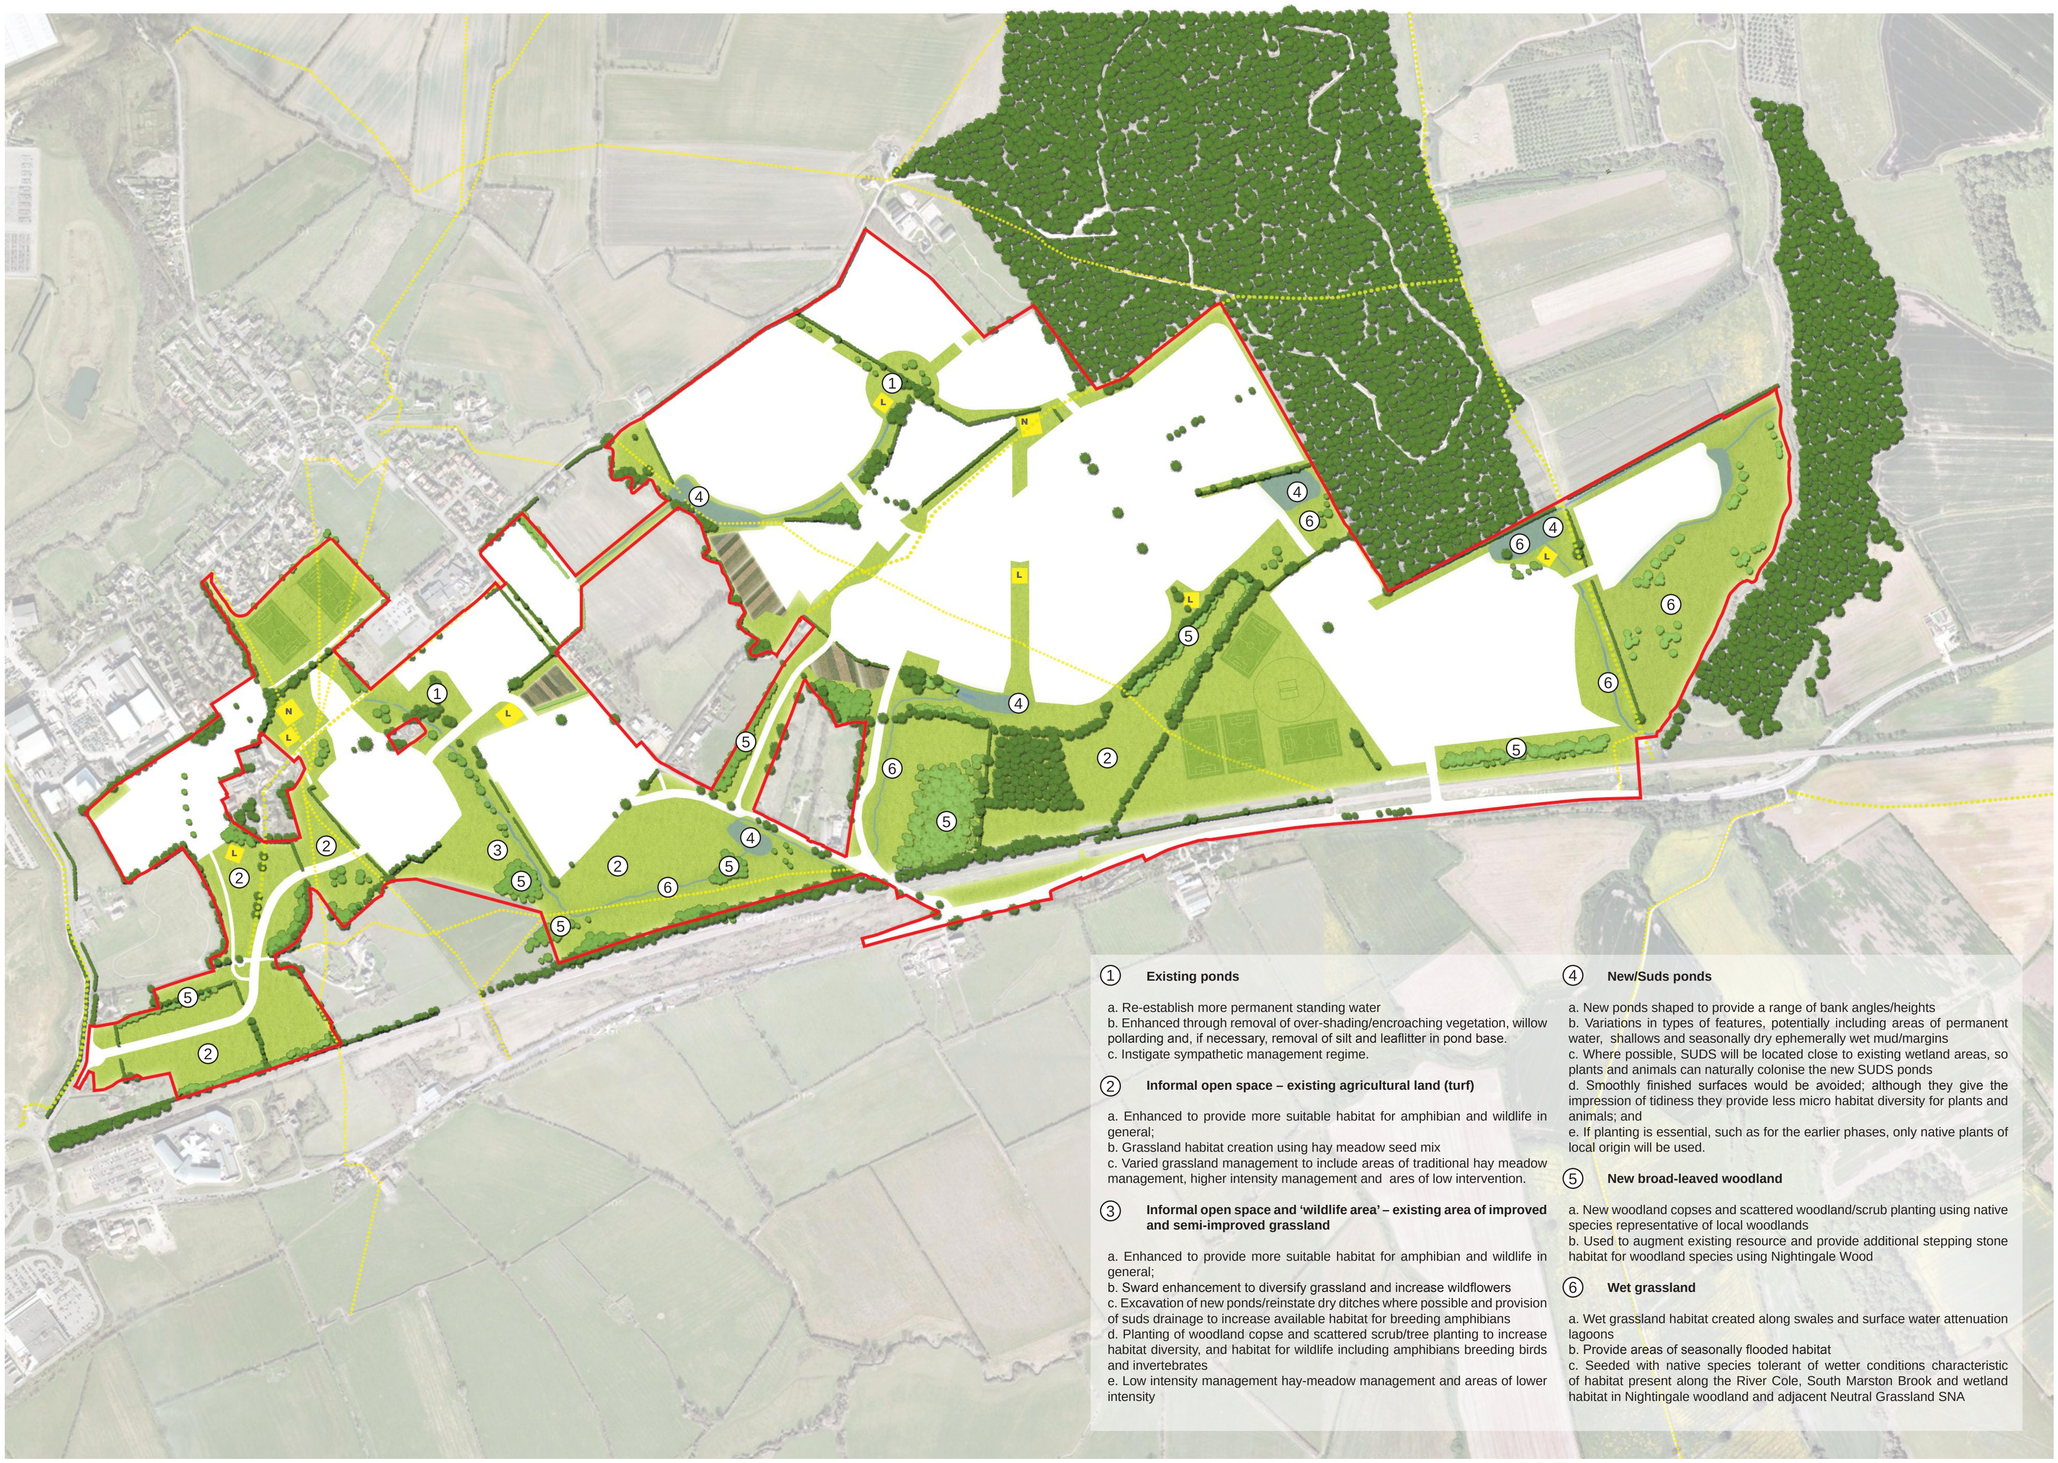

- Site Boundary
- Existing Vegetation (Woodland, Hedges and Trees)
- Existing Public Footpath and Bridleway
- Proposed New Woodland, Hedgerow and Tree Planting
- Proposed Green Space
- Proposed Allotments
- Proposed Sports
- Proposed SUDs / Drainage Ditches
- Proposed LEAPs
- Proposed NEAPs

Final layout and design of the green infrastructure to be reserved, providing significant flexibility to allow the creation of a range of different habitats, the detail of which will be provided in consultation with interested parties including statutory and non-statutory nature conservation organisations

1 Existing ponds

a. Re-establish more permanent standing water
b. Enhanced through removal of over-shading/encroaching vegetation, willow pollarding and, if necessary, removal of silt and leaflitter in pond base.
c. Instigate sympathetic management regime.

2 Informal open space – existing agricultural land (turf)

a. Enhanced to provide more suitable habitat for amphibian and wildlife in general;
b. Grassland habitat creation using hay meadow seed mix
c. Varied grassland management to include areas of traditional hay meadow management, higher intensity management and ares of low intervention.

3 Informal open space and 'wildlife area' – existing area of improved and semi-improved grassland

a. Enhanced to provide more suitable habitat for amphibian and wildlife in general;
b. Sward enhancement to diversify grassland and increase wildflowers
c. Excavation of new ponds/reinstate dry ditches where possible and provision of suds drainage to increase available habitat for breeding amphibians
d. Planting of woodland copse and scattered scrub/tree planting to increase habitat diversity, and habitat for wildlife including amphibians breeding birds and invertebrates
e. Low intensity management hay-meadow management and areas of lower intensity

4 New/Suds ponds

a. New ponds shaped to provide a range of bank angles/heights
b. Variations in types of features, potentially including areas of permanent water, shallows and seasonally dry ephemerally wet mud/margins
c. Where possible, SUDS will be located close to existing wetland areas, so plants and animals can naturally colonise the new SUDS ponds
d. Smoothly finished surfaces would be avoided; although they give the impression of tidiness they provide less micro habitat diversity for plants and animals; and
e. If planting is essential, such as for the earlier phases, only native plants of local origin will be used.

5 New broad-leaved woodland

a. New woodland copses and scattered woodland/scrub planting using native species representative of local woodlands
b. Used to augment existing resource and provide additional stepping stone habitat for woodland species using Nightingale Wood

6 Wet grassland

a. Wet grassland habitat created along swales and surface water attenuation lagoons
b. Provide areas of seasonally flooded habitat
c. Seeded with native species tolerant of wetter conditions characteristic of habitat present along the River Cole, South Marston Brook and wetland habitat in Nightingale woodland and adjacent Neutral Grassland SNA

N

Scale: 1:5000 @ A1

0 100 200 300 400 500m

S:\1700\1796\Green Infrastructure Strategy\1796-L-03B OUTLINE BIODIVERSITY ENHANCEMENT OTIONS.indd

Hallam Land Management, Taylor Wimpey & Hannick Homes
East Swindon
Wiltshire

OUTLINE BIODIVERSITY ENHANCEMENT OPTIONS

1:5000@A1
08 February 2017 GJH / PH
1796-L-03 rev. **C**

masterplanning
environmental assessment
landscape design
urban design
ecology
architecture
arboriculture

FPCR Environment and Design Ltd
Lockington Hall
Lockington
Derby DE74 2RH

t: 01509 672772
f: 01509 674565
e: mail@fpcr.co.uk
w: www.fpcr.co.uk