1335/HL/57

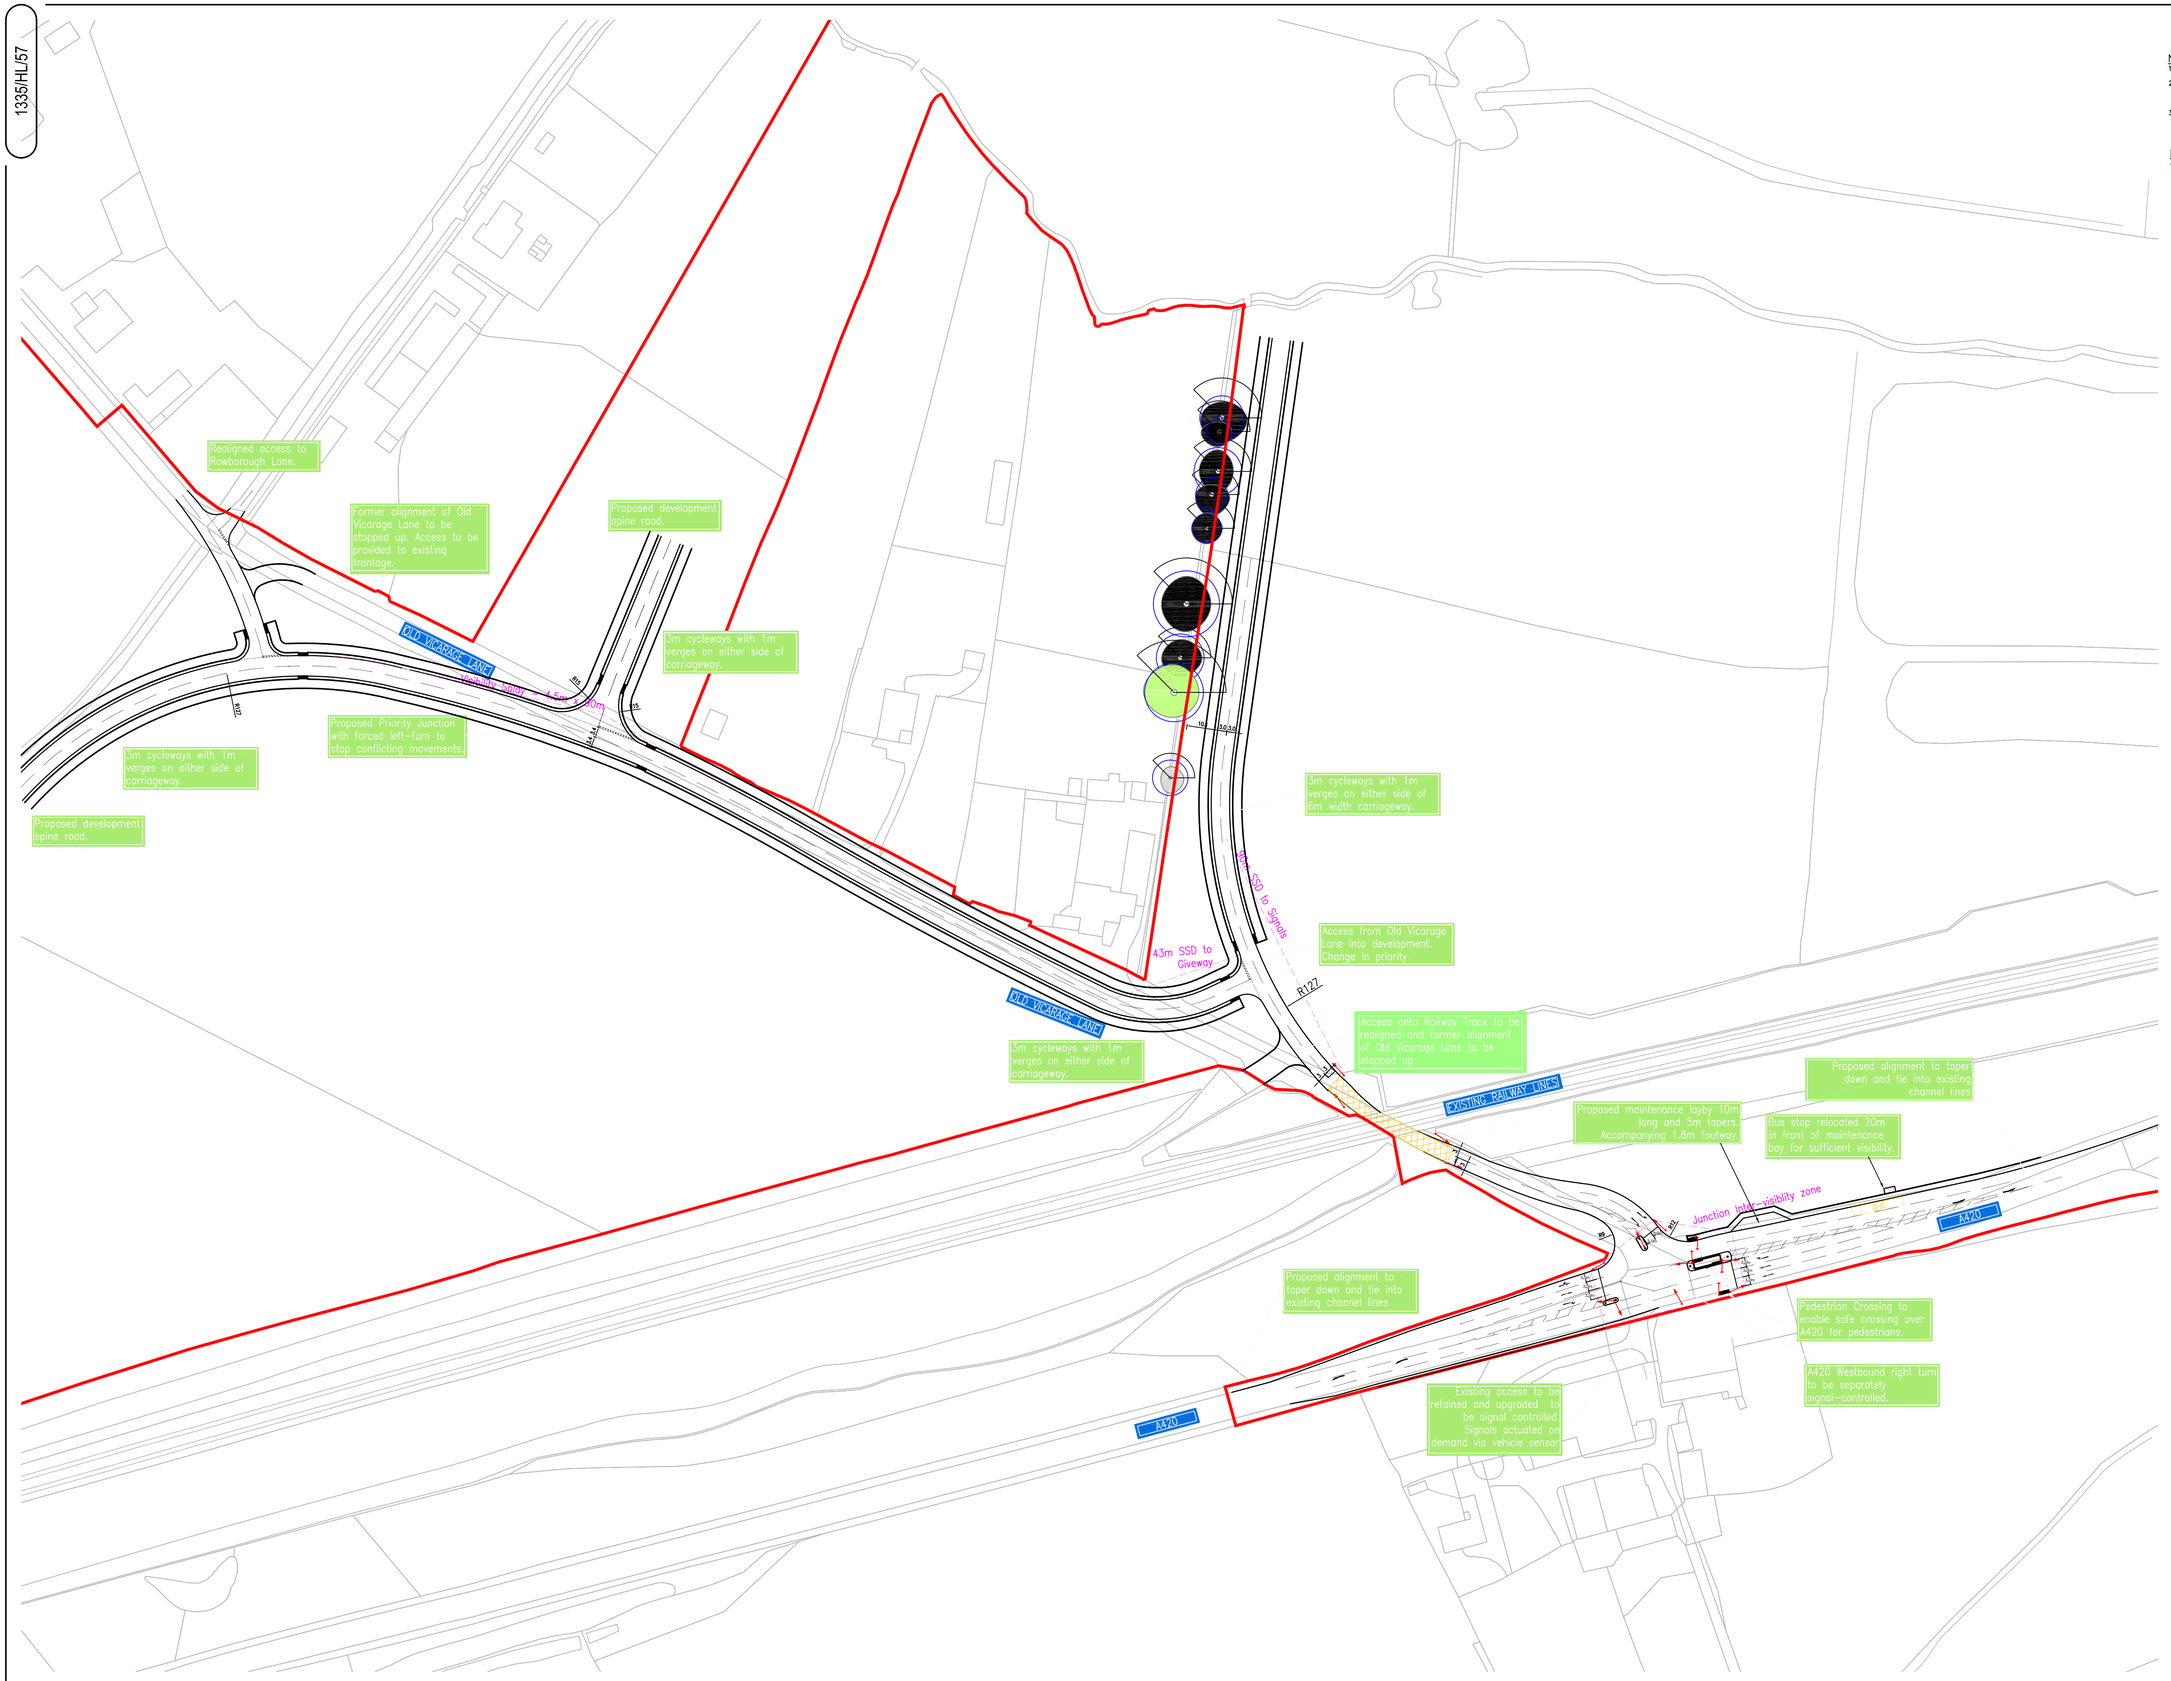

NOTES:

1. Do not scale from this drawing.
2. This drawing has been based on survey data provided by a third party. Brookbanks Consulting Ltd cannot be held responsible for the accuracy of this data.
3. Details shown are for information only and subject to change following completion of the detailed design.

KEY:

Existing Highway Boundary

Traffic Signal

N

Rev.	Revision Details	Drawn	Checked	Approved	Date
I/J	Amendments in response to SBC request	MM	DS	PB	05.10.1
H	Amendments in response to SBC request	DN	DS	PB	01.11.1
G	Amendments in response to RSA	DN	DS	PB	01.02.1

Issue Status		Approved	Date
Drawn 1:1000	Checked AE	Date	OCT 13

Brookbanks Consulting

6150 Knights Court Solihull Parkway Birmingham B37 7WY
Tel (0121) 329 4330 Fax (0121) 329 4331
www.brookbanks.com

Swindon EDAG

Swindon EDA

VICARAGE LANE IMPROVEMENT
PROPOSED JUNCTION

Scale at A1	Drawing No.	Rev.
1:1000	1335/HL/57	J

Original Drawing Size A1

© Brookbanks Consulting Limited 2013