1335/HL/54

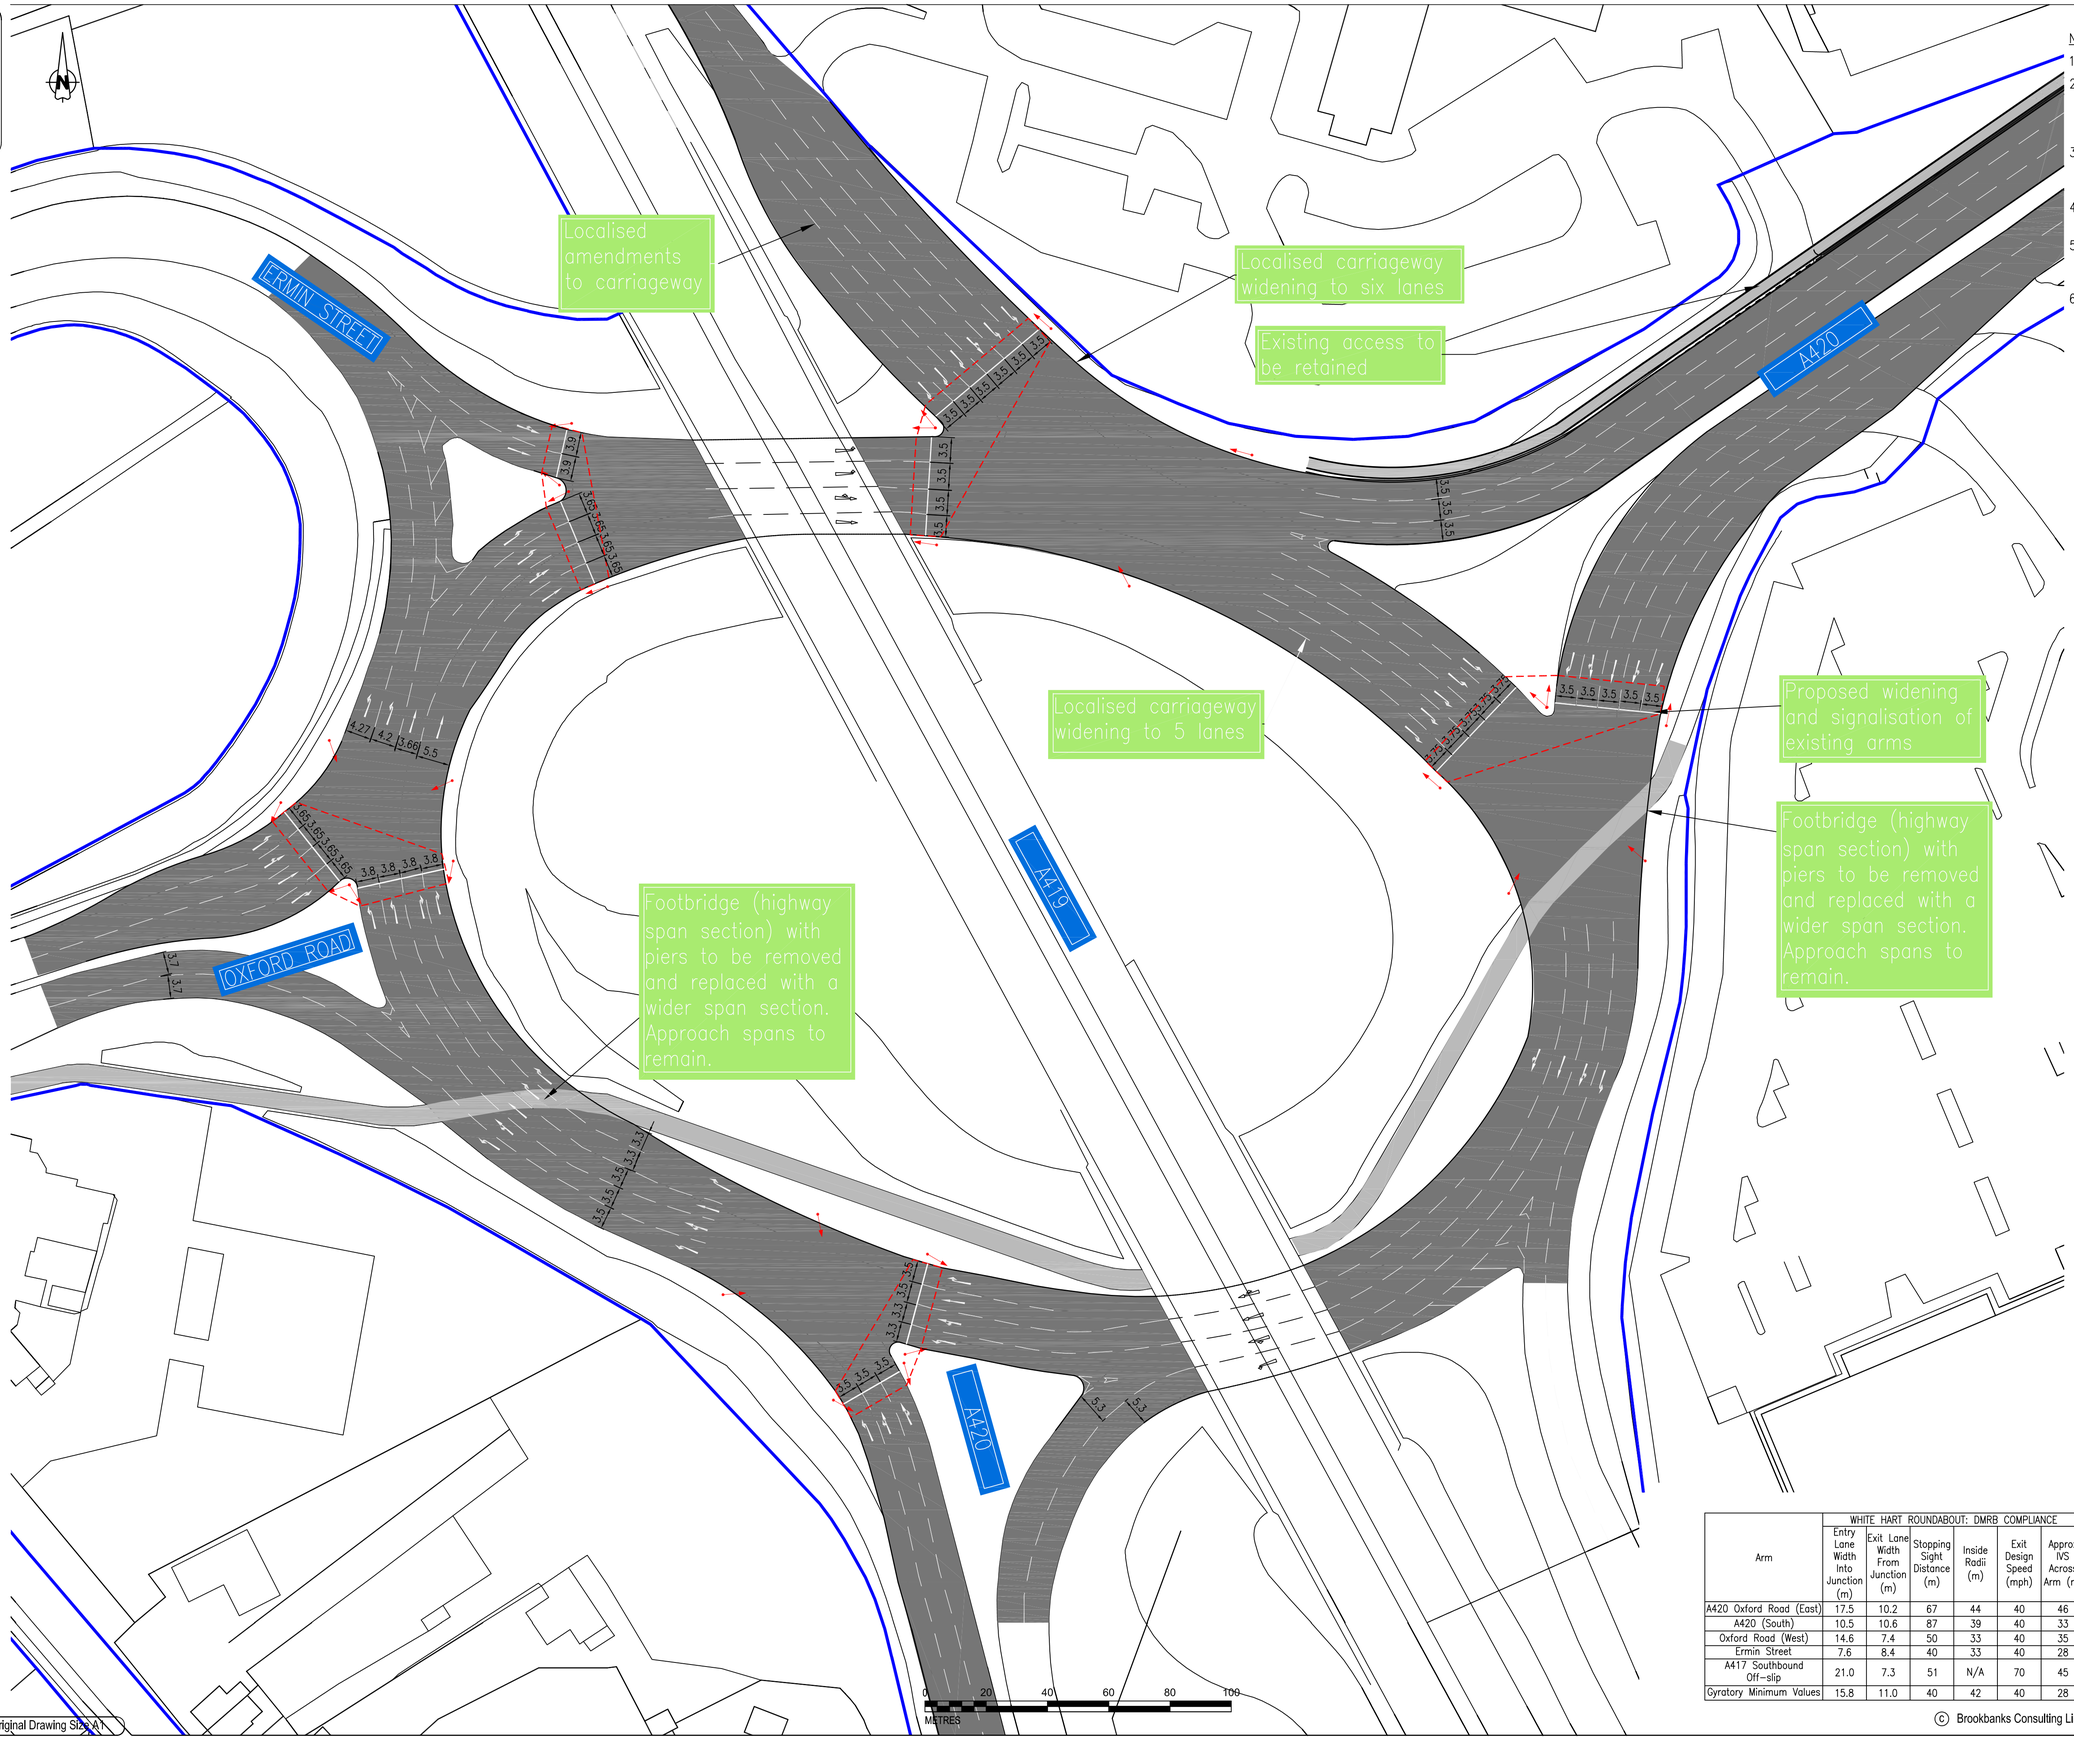

Notes:

1. Do not scale from this drawing.
2. This drawing has been based on survey data provided by a third party. Brookbanks Consulting Ltd cannot be held responsible for the accuracy of this information.
3. The roundabout and links have been designed in accordance with the relevant DMRB standards TD 9/93 and TD 16/07.
4. The markings have been designed in accordance with the Traffic Signs Manual Chapter 5.
5. The road signs have been designed and positioned in accordance with the Traffic Signs Manual Chapters 3 and 7. To be placed at 400mm min. from kerb.
6. The signalised roundabout has been designed in accordance with TD 50/04 The Geometric Layout of Signal Controlled Junctions and Signalised Roundabouts. The table below represents the design's compliance with the standard.

Arm	WHITE HART ROUNDABOUT: DMRB COMPLIANCE					
	Entry Lane Width Into Junction (m)	Exit Lane Width From Junction (m)	Stopping Sight Distance (m)	Inside Radii (m)	Exit Design Speed (mph)	Approx IVS Across Arm (m)
A420 Oxford Road (East)	17.5	10.2	67	44	40	46
A420 (South)	10.5	10.6	87	39	40	33
Oxford Road (West)	14.6	7.4	50	33	40	35
Ermin Street	7.6	8.4	40	33	40	28
A417 Southbound Off-slip	21.0	7.3	51	N/A	70	45
Gyratory Minimum Values	15.8	11.0	40	42	40	28

© Brookbanks Consulting Limited 2015

Rev.	Revision Details	Drawn	Checked	Approved	Date
	FOR PRELIMINARY REVIEW	PAB			11.06.15

Issue Status			Approved	Date
Drawn	MDM	Checked	AE	Date JUN 15

Brookbanks Consulting

6150 Knights Court Solihull Parkway Birmingham B37 7WY
Tel (0121) 329 4330 Fax (0121) 329 4331
www.brookbanks.com

Swindon EDAG

Swindon EDA

WHITE HART SIGNALISATION PROPOSED LAYOUT

Scale at A1	Drawing No.	Rev.
1:500	1335/HL/54	-

Original Drawing Size: A1