FRONT ELEVATION

SIDE ELEVATION

REAR ELEVATION

* OBSCURE GLAZED WINDOW

SIDE ELEVATION

* OBSCURE GLAZED WINDOW

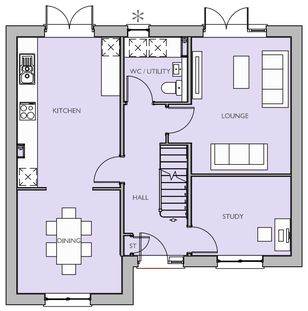

GROUND FLOOR PLAN

* OBSCURE GLAZED WINDOW

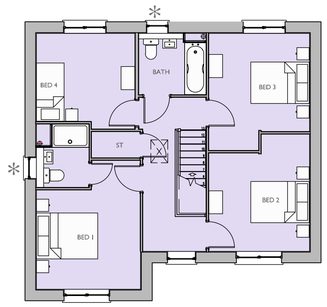

FIRST FLOOR PLAN

* OBSCURE GLAZED WINDOW

Housetype Name:	EMA47		
Occupancy:	4 BED / 7 PERSON		
Gross Area ft²:	Gross Area m²:	Net Area ft²:	Net Area m²:
1472.9	136.8	1454.3	135.1

For Colours of Material See External Finishes Layout CB_86_263_R8-R9_008

Primary Material:	STRETCHER BOND MASONRY BRICKWORK.
Feature Material:	
Architectural Detail:	PROJECTING STRING STRETCHER COURSE
Window & Door Frames:	UPVC CASEMENT WINDOW, WITH GLAZING BARS. COMPOSITE FRONT DOOR. UPVC FRENCH DOOR.
Fascia, Soffit & Bargeboard:	UPVC BOXED EAVES ROOFING SYSTEM.
Architectural Ornaments:	PREFABRICATED GRP BRICK SLIP REPLICA CHIMNEY STACK.
Guttering & Drainage:	BLACK UPVC DRAINAGE SYSTEM.

Plot Numbers:

12 (AS)

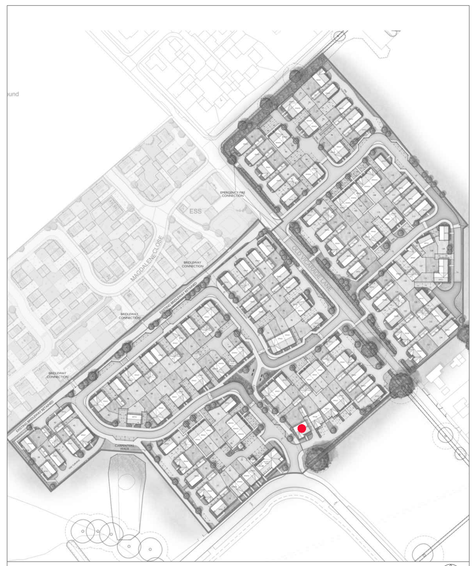

Location Plan (Not to Scale)

North

Scale @ A1:

0 1 2 3 4 5m

Scale 1:100

Rev	Date	Drawn	Checked
A	26.07.24	TW	BB

ALL ELEVATIONS UPDATED WITH PROJECTING BRICK DETAIL.

Date: DECEMBER 2023

Drawn by : KL

Checked by : BB

Drg No: CB_86_263_R8-R9_PS_EMA47_01

Rev: A

Project:

WOODLANDS, PARCELS R8 & R9
LAND NORTH OF A420, SWINDON

Title:

PS_EMA47
ELEVATIONS AND FLOORPLANS

Client:

Taylor Wimpey

COOPERBAILLIE

Please note these drawings are not for construction but for concept design and planning applications purposes only.
Cooper Baillie Limited - Connaught House, 24 Guildford Road, Bagshot, Surrey GU19 5JN - Telephone 01276 450039 - www.cooperbaillie.co.uk
This drawing and the works depicted are the copyright of Cooper Baillie Ltd. and may not be reproduced or amended except by written permission. No liability will be accepted for amendments made by other persons.

FRONT ELEVATION

* OBSCURE GLAZED WINDOW

SIDE ELEVATION

REAR ELEVATION

SIDE ELEVATION

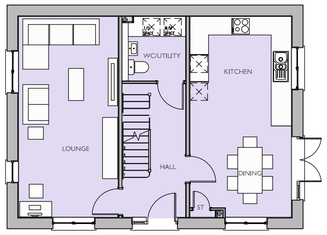

GROUND FLOOR PLAN

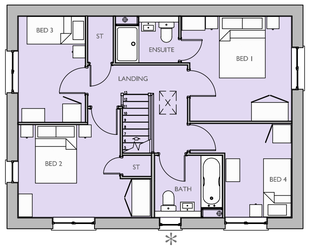

FIRST FLOOR PLAN

* OBSCURE GLAZED WINDOW

Housetype Name:	EMT41		
Occupancy:	4 BED / 6 PERSON		
Gross Area ft²:	Gross Area m²:	Net Area ft²:	Net Area m²:
1272.6	118.2	1255.9	116.7

For Colours of Material See External Finishes Layout CB_86_263_R8-R9_008	
Primary Material:	STRETCHER BOND MASONRY BRICKWORK.
Feature Material:	
Architectural Detail:	PROJECTING STRING STRETCHER COURSE.
Window & Door Frames:	UPVC CASEMENT WINDOW, WITH GLAZING BARS. COMPOSITE FRONT DOOR. UPVC FRENCH DOOR.
Fascia, Soffit & Bargeboard:	UPVC BOXED EAVES ROOFING SYSTEM.
Architectural Ornaments:	PREFABRICATED GRP BRICK SLIP REPLICA CHIMNEY STACK.
Guttering & Drainage:	BLACK UPVC DRAINAGE SYSTEM.

Plot Numbers:

18 (AS)

Location Plan (Not to Scale)

North

Scale @ A1:

0 1 2 3 4 5m

Scale 1:100

Rev	Date	Drawn	Checked
A	26.07.24	TW	BB

ALL ELEVATIONS UPDATED WITH PROJECTING BRICK DETAIL.

Project:

WOODLANDS, PARCELS R8 & R9
LAND NORTH OF A420, SWINDON

Title:

PS_EMT41
ELEVATIONS AND FLOORPLANS

Client:

Taylor Wimpey

Date: DECEMBER 2023

Drawn by : KL

Checked by : BB

Drg No: CB_86_263_R8-R9_PS_EMT41_01

Rev: A

COOPERBAILLIE

Please note these drawings are not for construction but for concept design and planning applications purposes only.
Cooper Baillie Limited - Connaught House, 24 Guildford Road, Bagshot, Surrey GU19 5JN - Telephone 01276 450039 - www.cooperbaillie.co.uk
This drawing and the works depicted are the copyright of Cooper Baillie Ltd. and may not be reproduced or amended, except by written permission. No liability will be accepted for amendments made by other persons.

FRONT ELEVATION

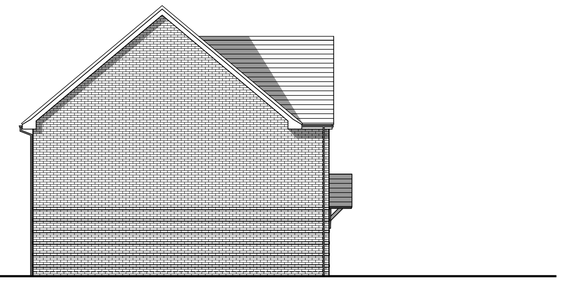

SIDE ELEVATION

REAR ELEVATION

* OBSCURE GLAZED WINDOW

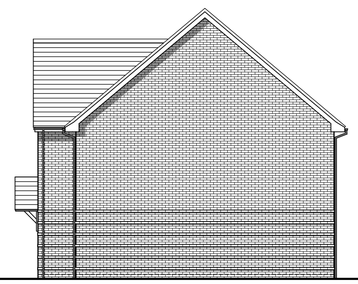

SIDE ELEVATION

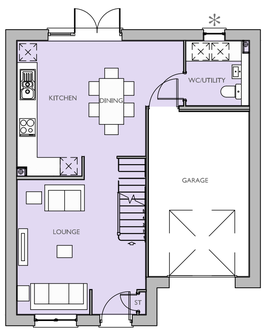

GROUND FLOOR PLAN

* OBSCURE GLAZED WINDOW

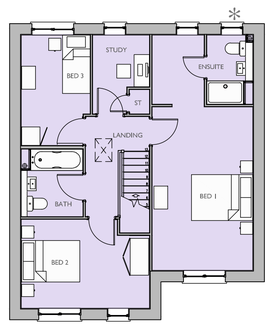

FIRST FLOOR PLAN

* OBSCURE GLAZED WINDOW

Housetype Name:	EMG31		
Occupancy:	3 BED / 5 PERSON		
Gross Area ft²:	Gross Area m²:	Net Area ft²:	Net Area m²:
1175.5	109.2	1157.8	107.6

For Colours of Material See External Finishes Layout CB_86_263_R8-R9_008	
Primary Material:	STRETCHER BOND MASONRY BRICKWORK.
Feature Material:	
Architectural Detail:	PROJECTING STRING STRETCHER COURSE
Window & Door Frames:	UPVC CASEMENT WINDOW. COMPOSITE FRONT DOOR. UPVC FRENCH DOOR.
Fascia, Soffit & Bargeboard:	UPVC BOXED EAVES ROOFING SYSTEM.
Architectural Ornaments:	
Guttering & Drainage:	BLACK UPVC DRAINAGE SYSTEM.

Plot Numbers:

13 (AS), 14 (OPP)

Location Plan (Not to Scale)

North

Scale @ A1:

0 1 2 3 4 5m

Scale 1:100

Rev	Date	Drawn	Checked
A	26.07.24	TW	BB

ALL ELEVATIONS UPDATED WITH PROJECTING BRICK DETAIL.

Date: DECEMBER 2023

Drawn by : KL

Checked by : BB

Drg No: CB_86_263_R8-R9_PS_EMG31_01

Rev: A

Project:

WOODLANDS, PARCELS R8 & R9
LAND NORTH OF A420, SWINDON

Title:

PS_EMG31
ELEVATIONS AND FLOORPLANS

Client:

Taylor Wimpey

COOPERBAILLIE

Please note these drawings are not for construction but for concept design and planning applications purposes only.

Cooper Baillie Limited - Connaught House, 24 Guildford Road, Bagshot, Surrey GU19 5JN - Telephone 01276 450039 - www.cooperbaillie.co.uk

This drawing and the works depicted are the copyright of Cooper Baillie Ltd. and may not be reproduced or amended, except by written permission. No liability will be accepted for amendments made by other persons.

FRONT ELEVATION

* OBSCURE GLAZED WINDOW

SIDE ELEVATION

REAR ELEVATION

SIDE ELEVATION

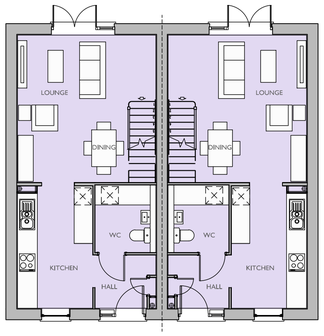

GROUND FLOOR PLAN

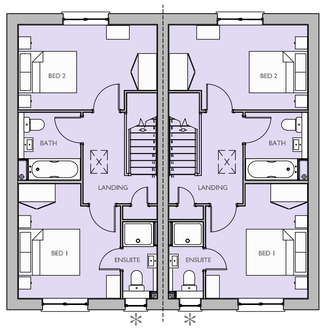

FIRST FLOOR PLAN

* OBSCURE GLAZED WINDOW

Housetype Name:	EMA23		
Occupancy:	2 BED / 4 PERSON		
Gross Area ft²:	Gross Area m²:	Net Area ft²:	Net Area m²:
880.8	81.8	866.3	80.5

For Colours of Material See External Finishes Layout CB_86_263_R8-R9_008	
Primary Material:	STRETCHER BOND MASONRY BRICKWORK.
Feature Material:	
Architectural Detail:	PROJECTING STRING STRETCHER COURSE
Window & Door Frames:	UPVC CASEMENT WINDOW. COMPOSITE FRONT DOOR. UPVC FRENCH DOOR.
Fascia, Soffit & Bargeboard:	UPVC BOXED EAVES ROOFING SYSTEM.
Architectural Ornaments:	
Guttering & Drainage:	BLACK UPVC DRAINAGE SYSTEM.

Plot Numbers:

15-16 (AS)

Location Plan (Not to Scale)

North

Scale @ A1:

0 1 2 3 4 5m

Scale 1:100

Rev	Date	Drawn	Checked
A	26.07.24	TW	BB

ALL ELEVATIONS UPDATED WITH PROJECTING BRICK DETAIL.

Date: DECEMBER 2023

Drawn by : KL

Checked by : BB

Drg No: CB_86_263_R8-R9_PS_EMA23_01

Rev: A

Project:

WOODLANDS, PARCELS R8 & R9
LAND NORTH OF A420, SWINDON

Title:

PS_EMA23
ELEVATIONS AND FLOORPLANS

Client:

Taylor Wimpey

COOPERBAILLIE

Please note these drawings are not for construction but for concept design and planning applications purposes only.
Cooper Baillie Limited - Connaught House, 24 Guildford Road, Bagshot, Surrey GU19 5JN - Telephone 01276 450039 - www.cooperbaillie.co.uk
This drawing and the works depicted are the copyright of Cooper Baillie Ltd. and may not be reproduced or amended, except by written permission. No liability will be accepted for amendments made by other persons.

FRONT ELEVATION

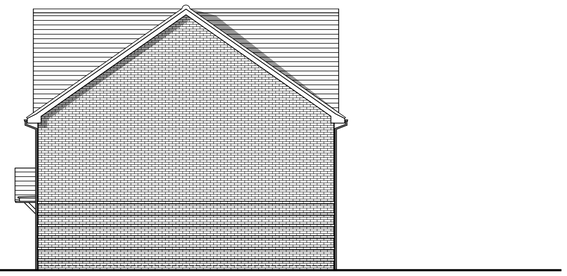

SIDE ELEVATION

REAR ELEVATION

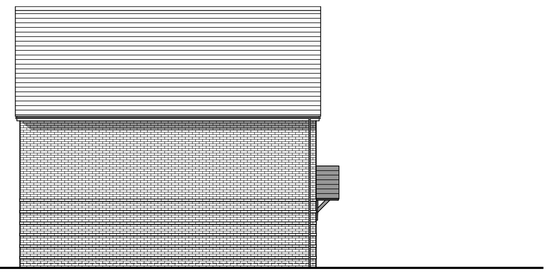

SIDE ELEVATION

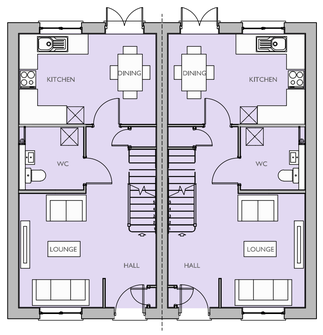

GROUND FLOOR PLAN

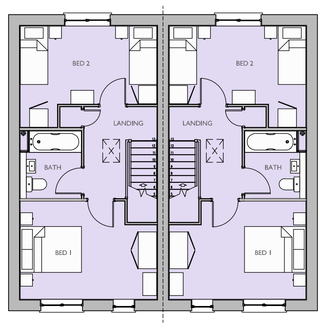

FIRST FLOOR PLAN

Housetype Name:	EMAP22		
Occupancy:	2 BED / 4 PERSON		
Gross Area ft²:	Gross Area m²:	Net Area ft²:	Net Area m²:
869.9	80.8	855.5	79.5

For Colours of Material See External Finishes Layout CB_86_263_R8-R9_008	
Primary Material:	STRETCHER BOND MASONRY BRICKWORK.
Feature Material:	
Architectural Detail:	PROJECTING STRING STRETCHER COURSE
Window & Door Frames:	UPVC CASEMENT WINDOW. COMPOSITE FRONT DOOR. UPVC FRENCH DOOR.
Fascia, Soffit & Bargeboard:	UPVC BOXED EAVES ROOFING SYSTEM.
Architectural Ornaments:	
Guttering & Drainage:	BLACK UPVC DRAINAGE SYSTEM.

Plot Numbers:

19-20 (AS) & 21-22 (OPP)

Location Plan (Not to Scale)

North

Scale @ A1:

0 1 2 3 4 5m

Scale 1:100

Rev	Date	Drawn	Checked
A	26.07.24	TW	BB

ALL ELEVATIONS UPDATED WITH PROJECTING BRICK DETAIL.

Date: DECEMBER 2023

Drawn by : KL

Checked by : BB

Drg No: CB_86_263_R8-R9_PS_EMAP22_01

Rev: A

Project:

WOODLANDS, PARCELS R8 & R9
LAND NORTH OF A420, SWINDON

Title:

PS_EMAP22
ELEVATIONS AND FLOORPLANS

Client:

Taylor Wimpey

COOPERBAILLIE

Please note these drawings are not for construction but for concept design and planning applications purposes only.
Cooper Baillie Limited - Connaught House, 24 Guildford Road, Bagshot, Surrey GU19 5JN - Telephone 01276 450039 - www.cooperbaillie.co.uk
This drawing and the works depicted are the copyright of Cooper Baillie Ltd. and may not be reproduced or amended, except by written permission. No liability will be accepted for amendments made by other persons.

FRONT ELEVATION

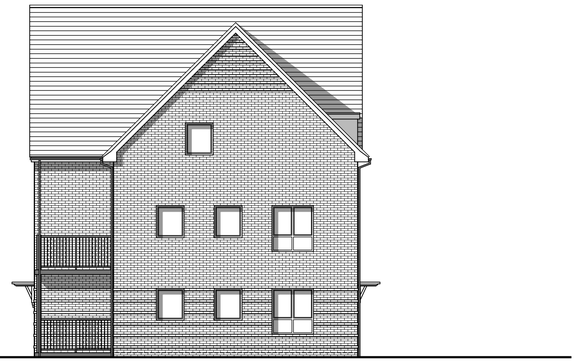

SIDE ELEVATION

REAR ELEVATION

* OBSCURE GLAZED WINDOW

SIDE ELEVATION

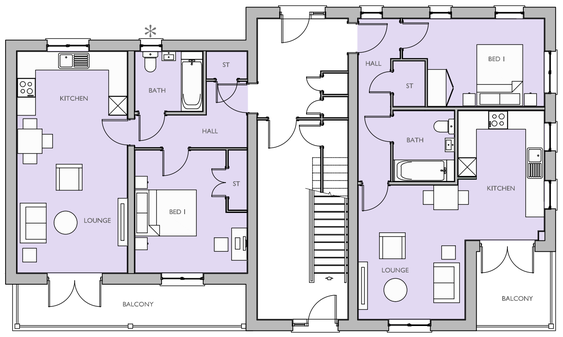

GROUND FLOOR PLAN

* OBSCURE GLAZED WINDOW

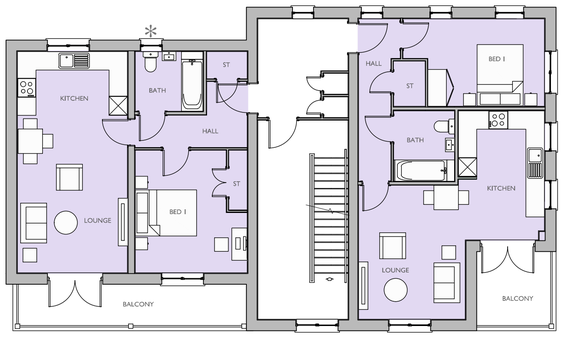

FIRST FLOOR PLAN

* OBSCURE GLAZED WINDOW

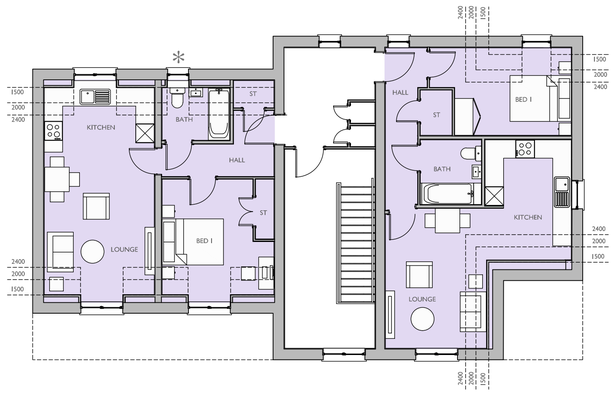

SECOND FLOOR PLAN

* OBSCURE GLAZED WINDOW

Housetype Name:	BLOCK A		
Occupancy:	1 BED / 2 PERSON		
Gross Area ft²:	Gross Area m²:	Net Area ft²:	Net Area m²:
576.2 590.2	53.5 54.8	567.6 582.3	52.7 54.1

For Colours of Material See External Finishes Layout CB_86_263_R8-R9_008

Primary Material:	STRETCHER BOND MASONRY BRICKWORK.
Feature Material:	
Architectural Detail:	PROJECTING STRING STRETCHER COURSE
Window & Door Frames:	UPVC CASEMENT WINDOW. COMPOSITE FRONT DOOR. UPVC FRENCH DOOR.
Fascia, Soffit & Bargeboard:	UPVC BOXED EAVES ROOFING SYSTEM.
Architectural Ornaments:	
Guttering & Drainage:	BLACK UPVC DRAINAGE SYSTEM.

Plot Numbers:

23-28 (AS)

Location Plan (Not to Scale)

North

Scale @ A1:

0 1 2 3 4 5m

Scale 1:100

Rev	Date	Drawn	Checked
A	26.07.24	TW	BB

UPDATED MATERIALS TO MATCH EXTERNAL FINISHES.

Project:

WOODLANDS, PARCELS R8 & R9
LAND NORTH OF A420, SWINDON

Title:

PS_BLOCK A
ELEVATIONS AND FLOORPLANS

Client:

Taylor Wimpey

Date: DECEMBER 2023

Drawn by : KL

Checked by : BB

Drg No: CB_86_263_R8-R9_PS_A_01

Rev: A

COOPERBAILLIE

Please note these drawings are not for construction but for concept design and planning applications purposes only.

Cooper Baillie Limited - Connaught House, 24 Guildford Road, Bagshot, Surrey GU19 5JN - Telephone 01276 450039 - www.cooperbaillie.co.uk

This drawing and the works depicted are the copyright of Cooper Baillie Ltd. and may not be reproduced or amended except by written permission. No liability will be accepted for amendments made by other persons.