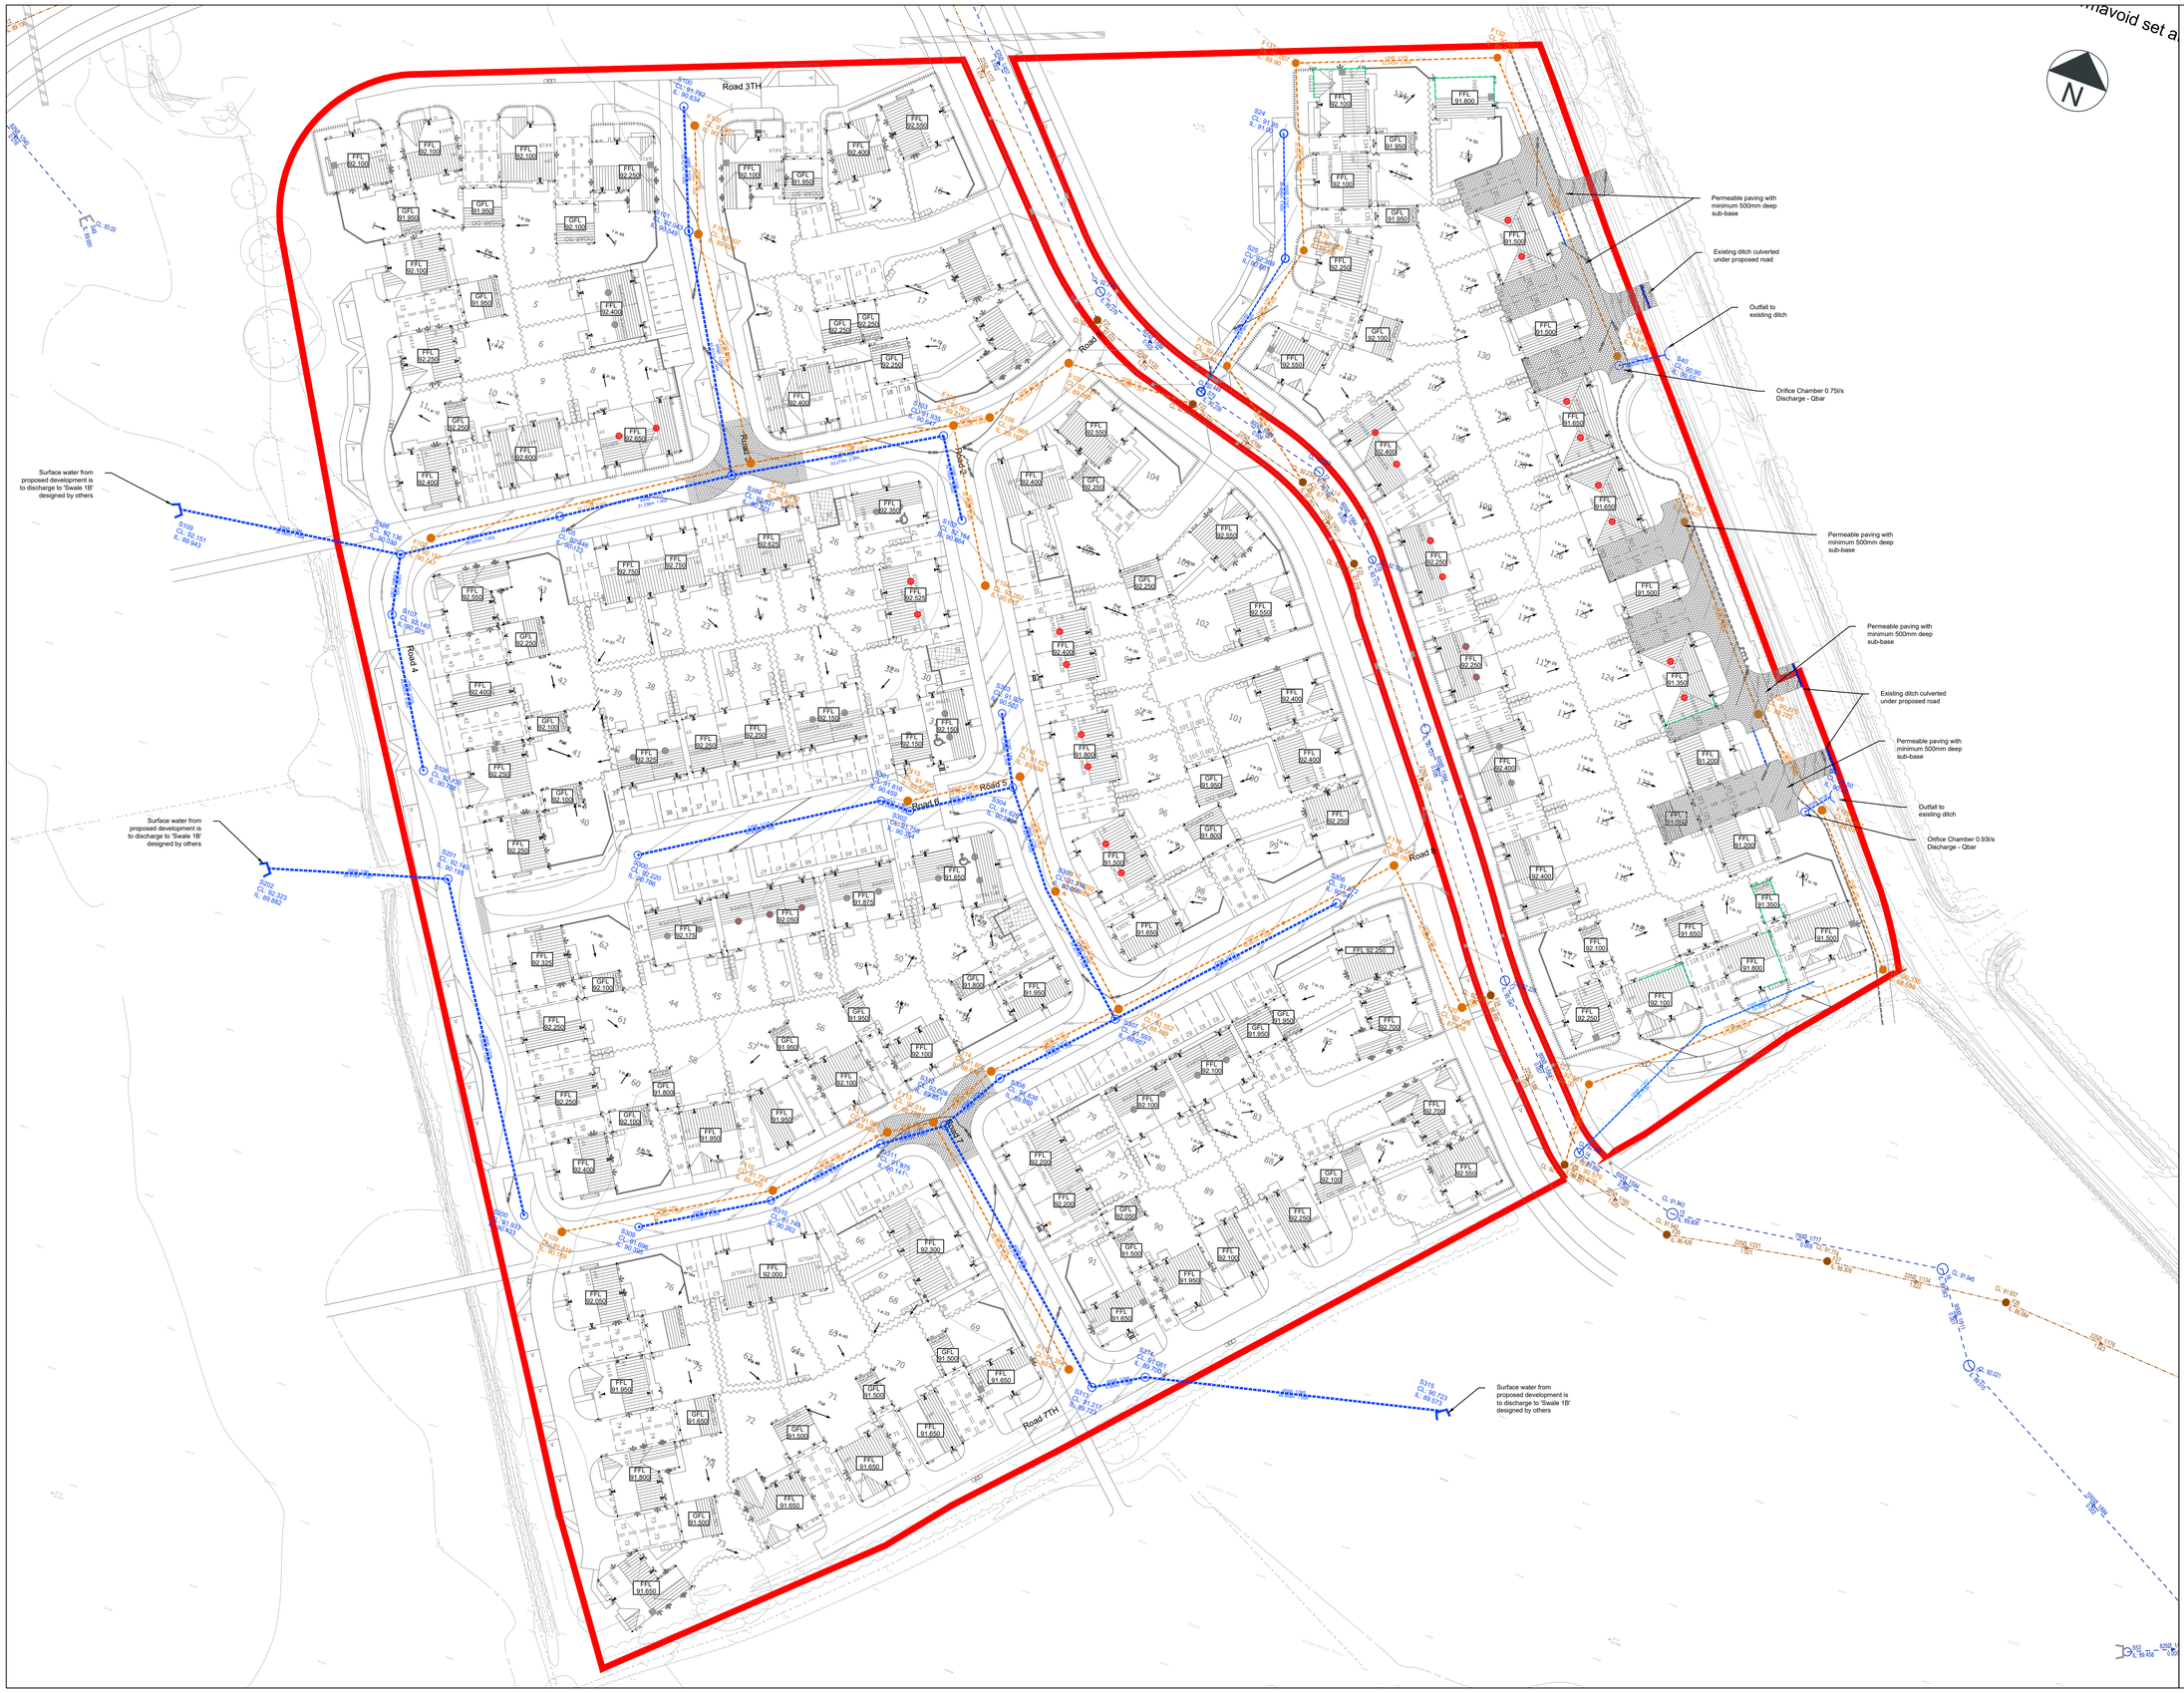

Notes:

1. Do not scale from this drawing. All dimensions are in metres, unless stated otherwise.
2. This drawing is based on the Architect's layout.
3. Ordnance Survey, (c) Crown Copyright 2023. All rights reserved. Licence number 100022432.
4. Drawing to be read in conjunction with all other drawings. Any discrepancies are to be reported to the engineer 5 working days in advance of undertaking any work.
5. Final tolerance on FFL's and GFL's subject to detailed design and may vary by +/- 300mm

Key:

- Redline Boundary
- 123.50 Major Contour (0.5m)
- Minor Contour (0.1m)
- FFL 123.500 Plot Finished Floor Level
- GFL 123.500 Garage Finished Floor Level
- 72.71 + Proposed Spot Level
- 1 in 41 Slope and Gradient
- Underbuild — Shown where of significance
- Steps
- Proposed Adopted Foul Water Sewer
- Proposed Adopted Foul Water Manhole
- Proposed Adopted Stormwater Sewer
- Proposed Adopted Stormwater Manhole
- Proposed Private Stormwater Drainage
- Headwall
- Proposed 'Swindon NEV' Foul Sewer — Main infrastructure drainage designed by others
- Proposed 'Swindon NEV' Storm Sewer — Main infrastructure drainage designed by others
- Proposed Permeable Paving

Rev	Date	Details	By	Chkd
P02	11.10.24	Updated to revised planning layout	KR	RS
P01	05.08.24	First Issue	EB	RS

rappor

rappor.co.uk

CLIENT:
Vistry Group

PROJECT:
Woodlands
South Marston

TITLE:
Engineering Layout

SCALE @ A1:	DATE:	DRAWN:	CHECKED:	APPROVED:
1:500	23.07.24	EB	RS	RS

STATUS: PLANNING

DRAWING NO: 240616-RAP-XX-XX-DR-C-0100

REVISION: P02

RESERVED COPYRIGHT