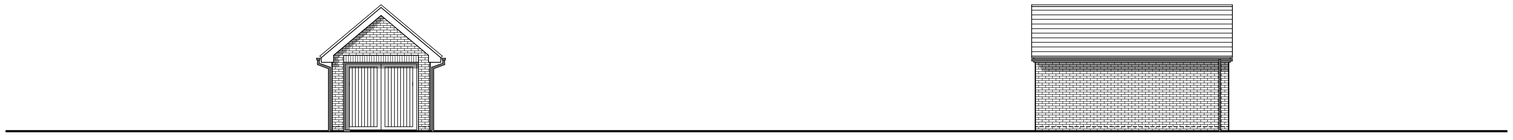

FRONT ELEVATION

SIDE ELEVATION

REAR ELEVATION

SIDE ELEVATION

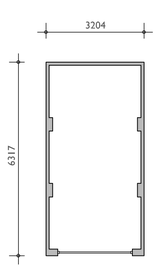

FLOOR PLAN

Housetype Name:	GARAGE		
Occupancy:			
Gross Area ft²:	Gross Area m²:	Net Area ft²:	Net Area m²:

For Colours of Material See External Finishes Layout CB_86_263_R8-R9_008	
Primary Material:	STRETCHER BOND MASONRY BRICKWORK.
Feature Material:	
Architectural Detail:	BRICK HEADERS
Window & Door Frames:	
Fascia, Soffit & Bargeboard:	UPVC BOXED EAVES ROOFING SYSTEM.
Architectural Ornaments:	
Guttering & Drainage:	BLACK UPVC DRAINAGE SYSTEM.

Plot Numbers:

1, 2, 3, 11, 12, 17, 18, 38, 39, 42, 43, 44, 48, 68, 69, 72, 73, 81, 82, 83, 84, 101, 98, 97, 111, 112, 113, 118, 119, 120, 121, 122, 125, 134

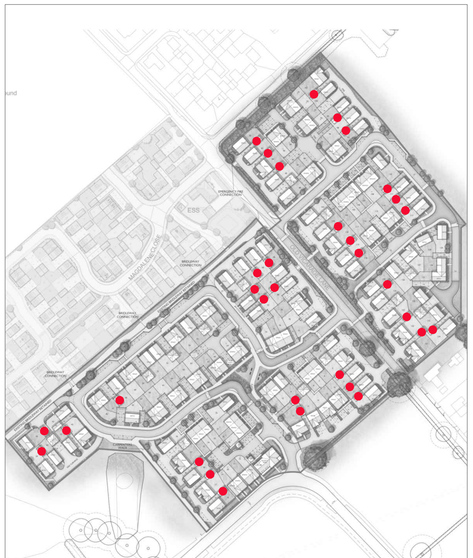

Location Plan (Not to Scale)

North

Scale @ A1:

0 1 2 3 4 5m

Scale 1:100

Rev	Date	Drawn	Checked
A	26.07.24	KL	BB

PLOT 51 & 52 REMOVED

Date: DECEMBER 2023

Drawn by : KL

Checked by : BB

Drg No: CB_86_263_R8-R9_GAR_01

Rev: A

Project:

WOODLANDS, PARCELS R8 & R9
LAND NORTH OF A420, SWINDON

Title:

GARAGE
ELEVATIONS AND FLOORPLANS

Client:

Taylor Wimpey

COOPERBAILLIE

Please note these drawings are not for construction but for concept design and planning applications purposes only.

Cooper Baillie Limited - Connaught House, 24 Guildford Road, Bagshot, Surrey GU19 5JN - Telephone 01276 450039 - www.cooperbaillie.co.uk

This drawing and the works depicted are the copyright of Cooper Baillie Ltd. and may not be reproduced or amended except by written permission. No liability will be accepted for amendments made by other persons.

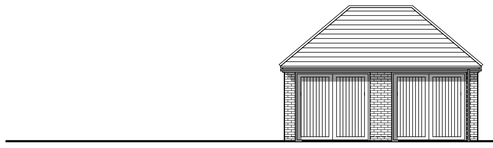

FRONT ELEVATION

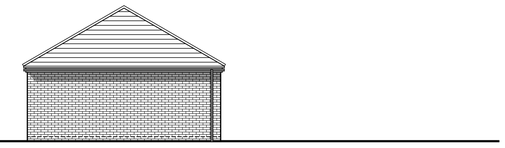

SIDE ELEVATION

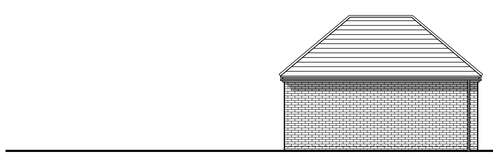

REAR ELEVATION

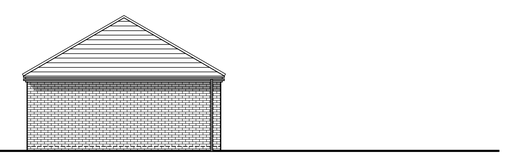

SIDE ELEVATION

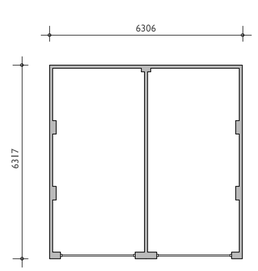

FLOOR PLAN

Housetype Name:	GARAGE		
Occupancy:			
Gross Area ft²:	Gross Area m²:	Net Area ft²:	Net Area m²:

For Colours of Material See External Finishes Layout CB_86_263_R8-R9_008	
Primary Material:	STRETCHER BOND MASONRY BRICKWORK.
Feature Material:	
Architectural Detail:	BRICK HEADERS
Window & Door Frames:	
Fascia, Soffit & Bargeboard:	UPVC BOXED EAVES ROOFING SYSTEM.
Architectural Ornaments:	
Guttering & Drainage:	BLACK UPVC DRAINAGE SYSTEM.

Plot Numbers:

4-5, 9-10, 36-37, 40-41, 50-51, 52-53, 55-56, 70-71, 85-86, 102-103, 123-124, 126-127, 132-133

Location Plan (Not to Scale)

North

Scale @ A1:

0 1 2 3 4 5m

Scale 1:100

Rev	Date	Drawn	Checked
A	26.07.24	KL	BB

PLOTS 50-53 ADDED

Date: DECEMBER 2023

Drawn by : KL Checked by : BB

Drg No: CB_86_263_R8-R9_GAR_02 Rev: A

Project:

WOODLANDS, PARCELS R8 & R9
LAND NORTH OF A420, SWINDON

Title:

GARAGE
ELEVATIONS AND FLOORPLANS

Client:

Taylor Wimpey

COOPERBAILLIE

Please note these drawings are not for construction but for concept design and planning applications purposes only.

Cooper Baillie Limited - Connaught House, 24 Guildford Road, Bagshot, Surrey GU19 5JN - Telephone 01276 450039 - www.cooperbaillie.co.uk

This drawing and the works depicted are the copyright of Cooper Baillie Ltd. and may not be reproduced or amended except by written permission. No liability will be accepted for amendments made by other persons.

FRONT ELEVATION

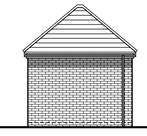

SIDE ELEVATION

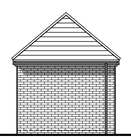

REAR ELEVATION

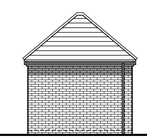

SIDE ELEVATION

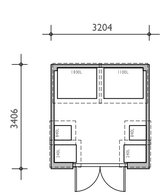

FLOOR PLAN

Housetype Name:	BIN STORAGE		
Occupancy:			
Gross Area ft²:	Gross Area m²:	Net Area ft²:	Net Area m²:

For Colours of Material See External Finishes Layout CB_86_263_R8-R9_008	
Primary Material:	STRETCHER BOND MASONRY BRICKWORK.
Feature Material:	
Architectural Detail:	
Window & Door Frames:	
Fascia, Soffit & Bargeboard:	UPVC BOXED EAVES ROOFING SYSTEM.
Architectural Ornaments:	
Guttering & Drainage:	BLACK UPVC DRAINAGE SYSTEM.

Plot Numbers:
23-28

Location Plan (Not to Scale)

North

Scale @ A1:

0 1 2 3 4 5m

Scale 1:100

Rev	Date	Drawn	Checked

Project:
WOODLANDS, PARCELS R8 & R9
LAND NORTH OF A420, SWINDON

Title:
BIN STORAGE
ELEVATIONS AND FLOORPLANS

Client:
Taylor Wimpey

Date: DECEMBER 2023

Drawn by : KL

Checked by : BB

Drg No: CB_86_263_R8-R9_BIN_01

Rev:

COOPERBAILLIE

Please note these drawings are not for construction but for concept design and planning applications purposes only.

Cooper Baillie Limited - Connaught House, 24 Guildford Road, Bagshot, Surrey GU19 5JN - Telephone 01276 450039 - www.cooperbaillie.co.uk

This drawing and the works depicted are the copyright of Cooper Baillie Ltd, and may not be reproduced or amended except by written permission. No liability will be accepted for amendments made by other persons.

FRONT ELEVATION

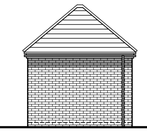

SIDE ELEVATION

REAR ELEVATION

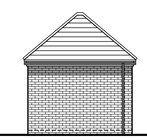

SIDE ELEVATION

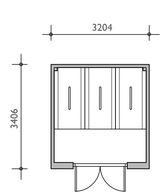

FLOOR PLAN

Housetype Name:	CYCLE STORAGE		
Occupancy:			
Gross Area ft²:	Gross Area m²:	Net Area ft²:	Net Area m²:

For Colours of Material See External Finishes Layout CB_86_263_R8-R9_008

Primary Material:	STRETCHER BOND MASONRY BRICKWORK.
Feature Material:	
Architectural Detail:	
Window & Door Frames:	
Fascia, Soffit & Bargeboard:	UPVC BOXED EAVES ROOFING SYSTEM.
Architectural Ornaments:	
Guttering & Drainage:	BLACK UPVC DRAINAGE SYSTEM.

Plot Numbers:

23-28

Location Plan (Not to Scale)

North

Scale @ A1:

0 1 2 3 4 5m

Scale 1:100

Rev	Date	Drawn	Checked

Project:

WOODLANDS, PARCELS R8 & R9
LAND NORTH OF A420, SWINDON

Title:

CYCLE STORAGE
ELEVATIONS AND FLOORPLANS

Client:

Taylor Wimpey

Date: DECEMBER 2023

Drawn by : KL

Checked by : BB

Drg No: CB_86_263_R8-R9_CYC_01

Rev:

COOPERBAILLIE

Please note these drawings are not for construction but for concept design and planning applications purposes only.

Cooper Baillie Limited - Connaught House, 24 Guildford Road, Bagshot, Surrey GU19 5JN - Telephone 01276 450039 - www.cooperbaillie.co.uk

This drawing and the works depicted are the copyright of Cooper Baillie Ltd, and may not be reproduced or amended, except by written permission. No liability will be accepted for amendments made by other persons.