Original Drawing Size A1

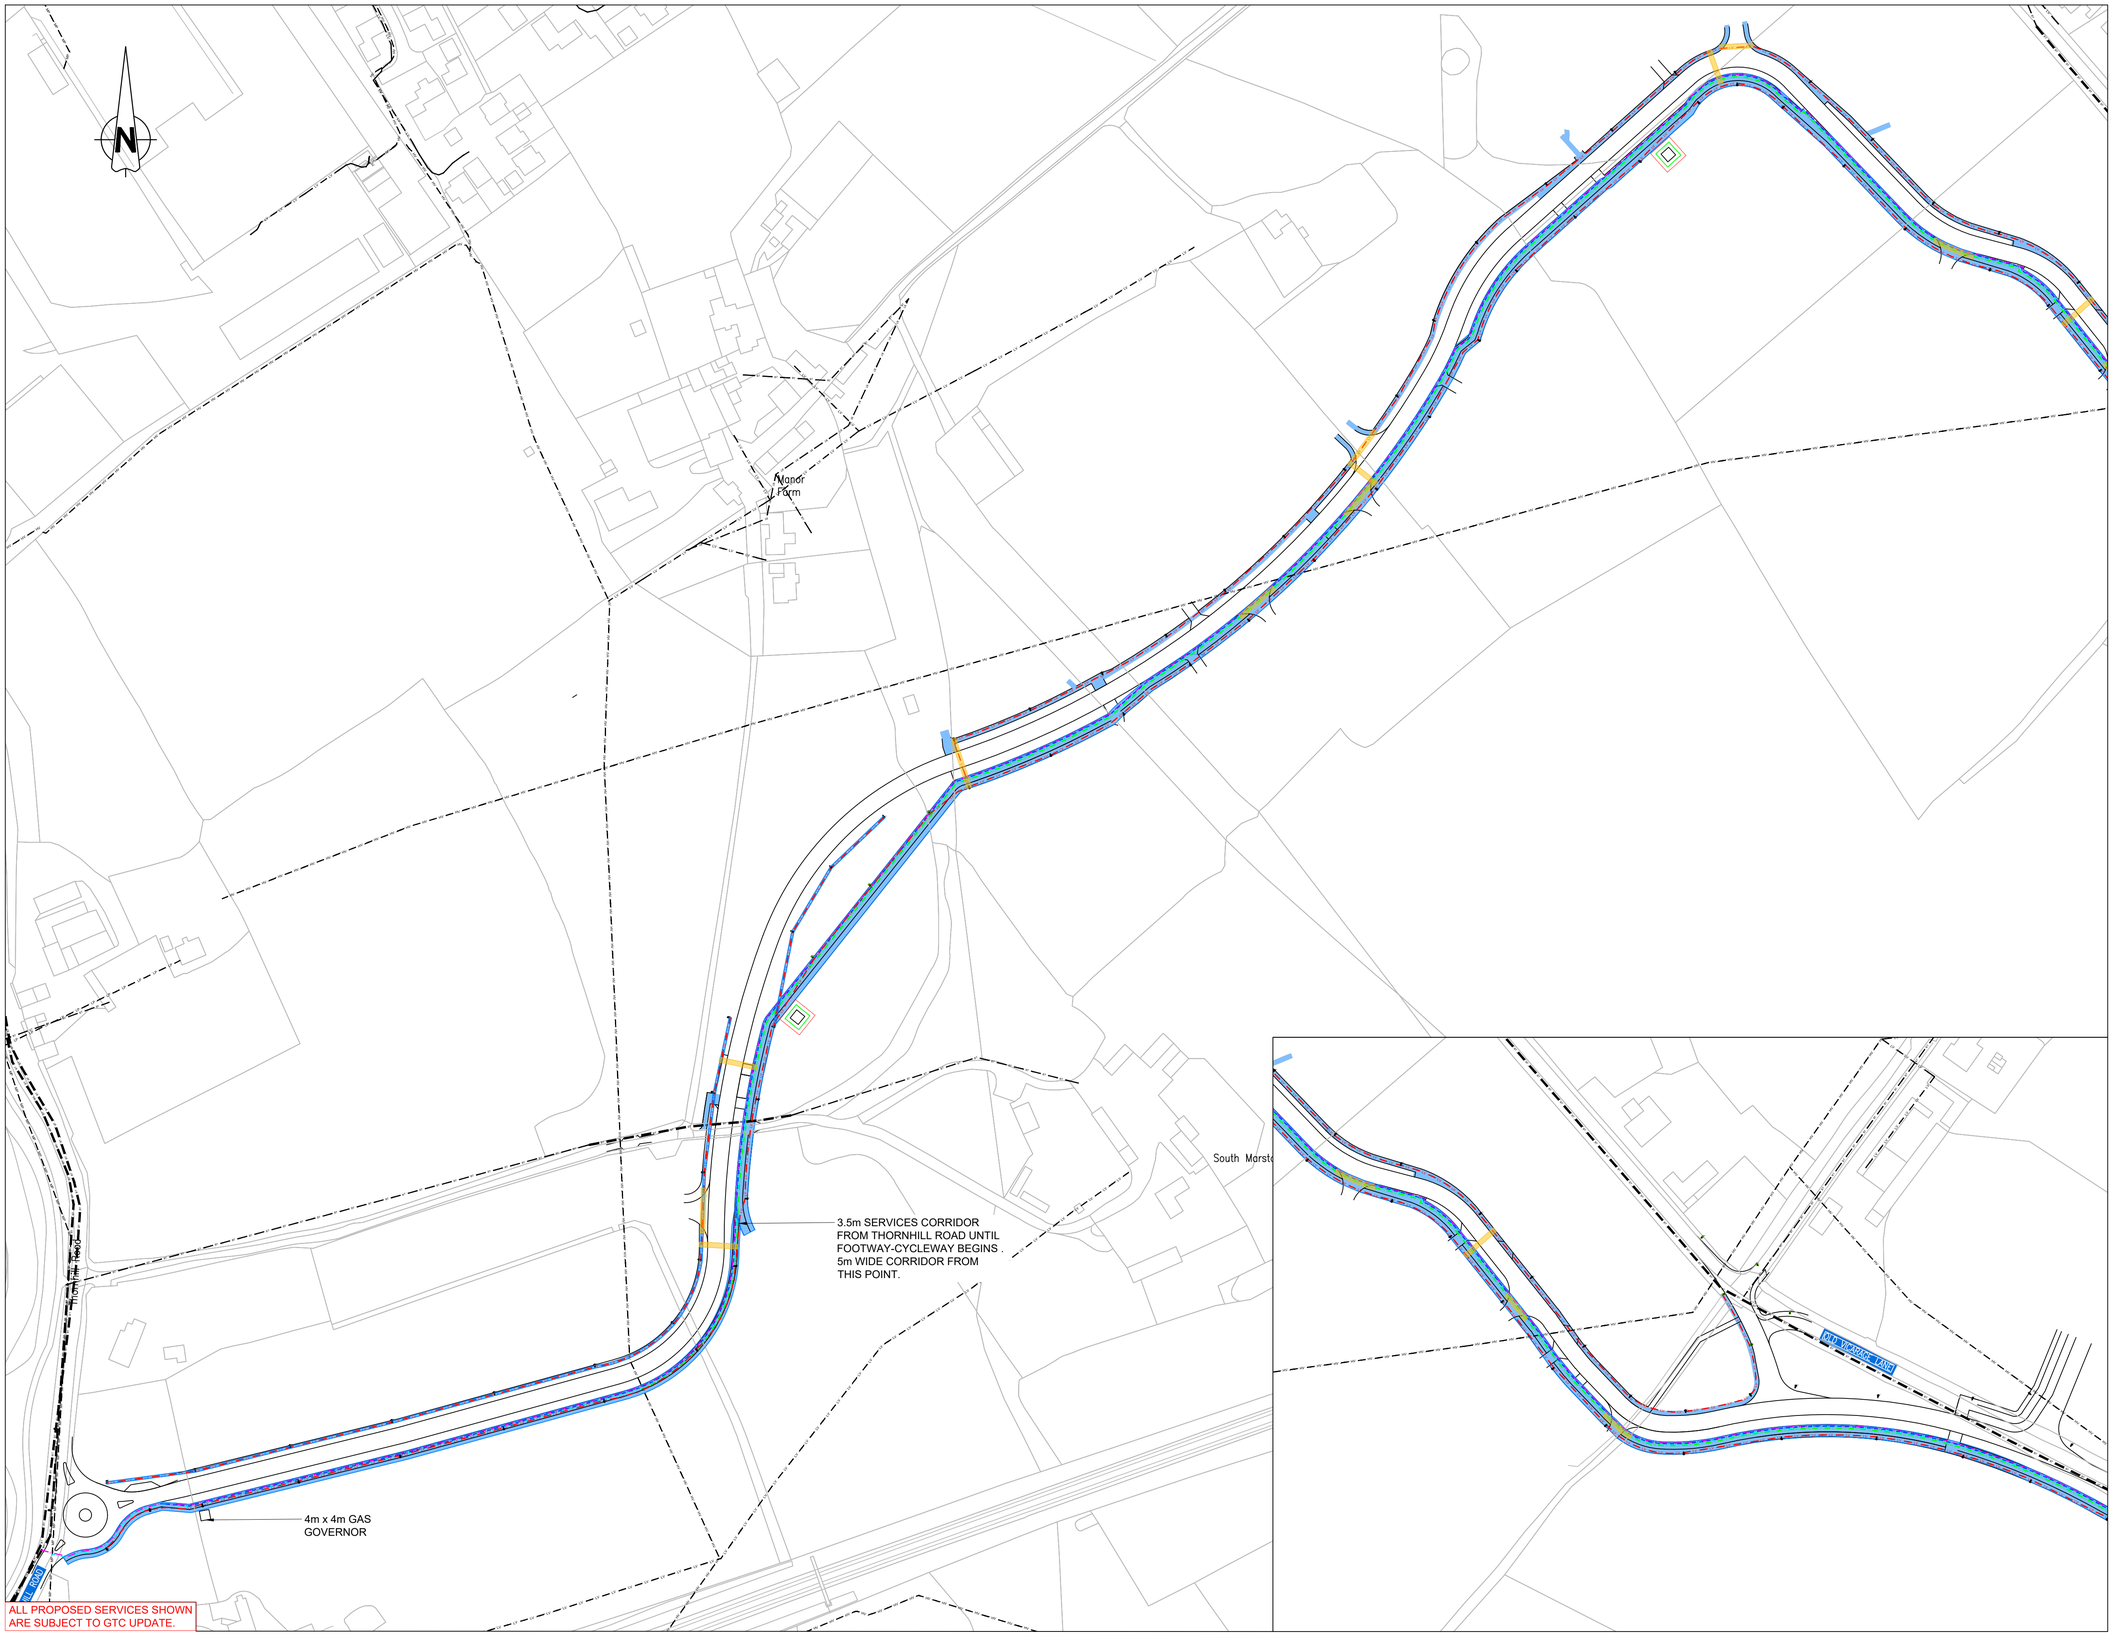

Construction Design and Management (CDM)

Key Residual Risks

Contractors entering the site should gain permission from the relevant land owners and/or principle contractor working on site at the time of entry. Contractors shall be responsible for carrying out their own risk assessments and for liaising with the relevant services companies and authorities. Listed below are Site Specific key risks associated with the project.

1) Overhead and underground services
2) Street Lighting Cables
3) Working adjacent to water courses and flood plain
4) Soft ground conditions
5) Working adjacent to live highways and railway line
6) Unchartered services
7) Existing buildings with potential asbestos hazards

NOTES:

1. Do not scale from this drawing.
2. All dimensions are in metres unless otherwise stated.
3. Brookbanks consulting ltd has prepared this drawing for the sole use of the client. the drawing may not be relied upon by any other party without the express agreement of the client and Brookbanks consulting ltd. where any data supplied by the client or from other sources has been used, it has been assumed that the information is correct. no responsibility can be accepted by Brookbanks consulting ltd for inaccuracies in the data supplied by any other party. the drawing has been produced based on the assumption that all relevant information has been supplied by those bodies from whom it was requested.
4. No part of this drawing may be copied or duplicated without the express permission of Brookbanks consulting ltd.
5. All dimensions and all levels in metres unless noted otherwise.
6. Lighting design subject to swale and FPCR design.

KEY:

- HV — EXISTING SSE HV
- LV — EXISTING SSE LV
- BT — EXISTING BT OVERHEAD
- BT — EXISTING BT UNDERGROUND
- LP — EXISTING WALES & WESTERN UTILITIES LOW PRESSURE GAS
- MP — EXISTING WALES & WESTERN UTILITIES MEDIUM PRESSURE GAS
- PROPOSED WATER MAIN
- MP — PROPOSED GAS
- BT — PROPOSED BT/TELECOMS
- HV — PROPOSED SSE HV
- LV — PROPOSED SSE LV
- INDICATIVE SUBSTATION LOCATIONS
- SERVICES CORRIDOR
- DUCT CROSSING
- LIGHTING COLUMN TYPE A
- LIGHTING COLUMN TYPE B
- LIGHTING COLUMN TYPE C
- LIGHTING COLUMN TYPE E

A	Updated following TW comment	CM	SM	SM	08.11.22
-	First Issue	CM	SM	SM	04.11.22

BROOKBANKS

6150 Knights Court, Solihull Parkway, Birmingham, B37 7WY
T +44 (0)203 958 5400 E mail@brookbanks.com
W brookbanks.com

Swindon EDA Consortium

Proposed Development
Swindon EV

South Marston Primary Street
Services Corridor

DRAFT

Status		Status Date
Draft		NOV' 2022
Drawn	Checked	Date
CM	SM	04.11.22
Scale	Number	Rev
1:1250	1335-SMPS-100-013	A

0 25 50 75 100 125
METRES

UNTIL TECHNICAL APPROVAL HAS BEEN OBTAINED FROM THE RELEVANT LOCAL AUTHORITIES, IT SHOULD BE UNDERSTOOD THAT ALL DRAWINGS ARE ISSUED AS PRELIMINARY AND NOT FOR CONSTRUCTION. SHOULD THE CONTRACTOR COMMENCE SITE WORK PRIOR TO APPROVAL BEING GIVEN, IT IS ENTIRELY AT HIS OWN RISK.

© Brookbanks Consulting Limited 2022

P:\1335\CAD\BCL\Current Drawings\S38- South Marston Primary Street\1335-SMPS-100-013A Services Corridor.dwg