Scale 1:50

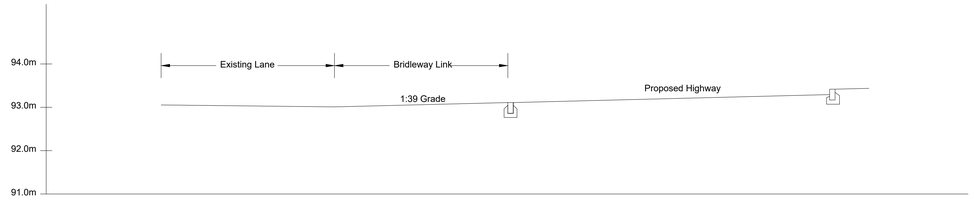

SECTION A-A

Scale 1:50

SECTION C-C

Scale 1:50

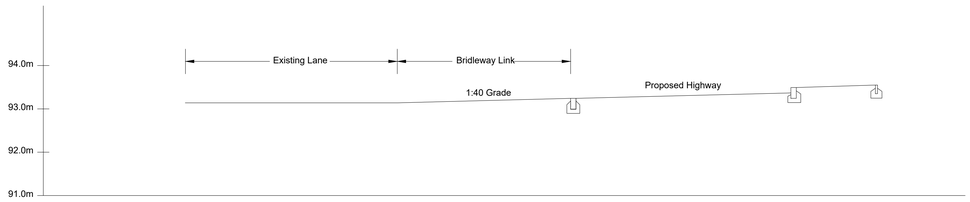

SECTION B-B

Scale 1:200

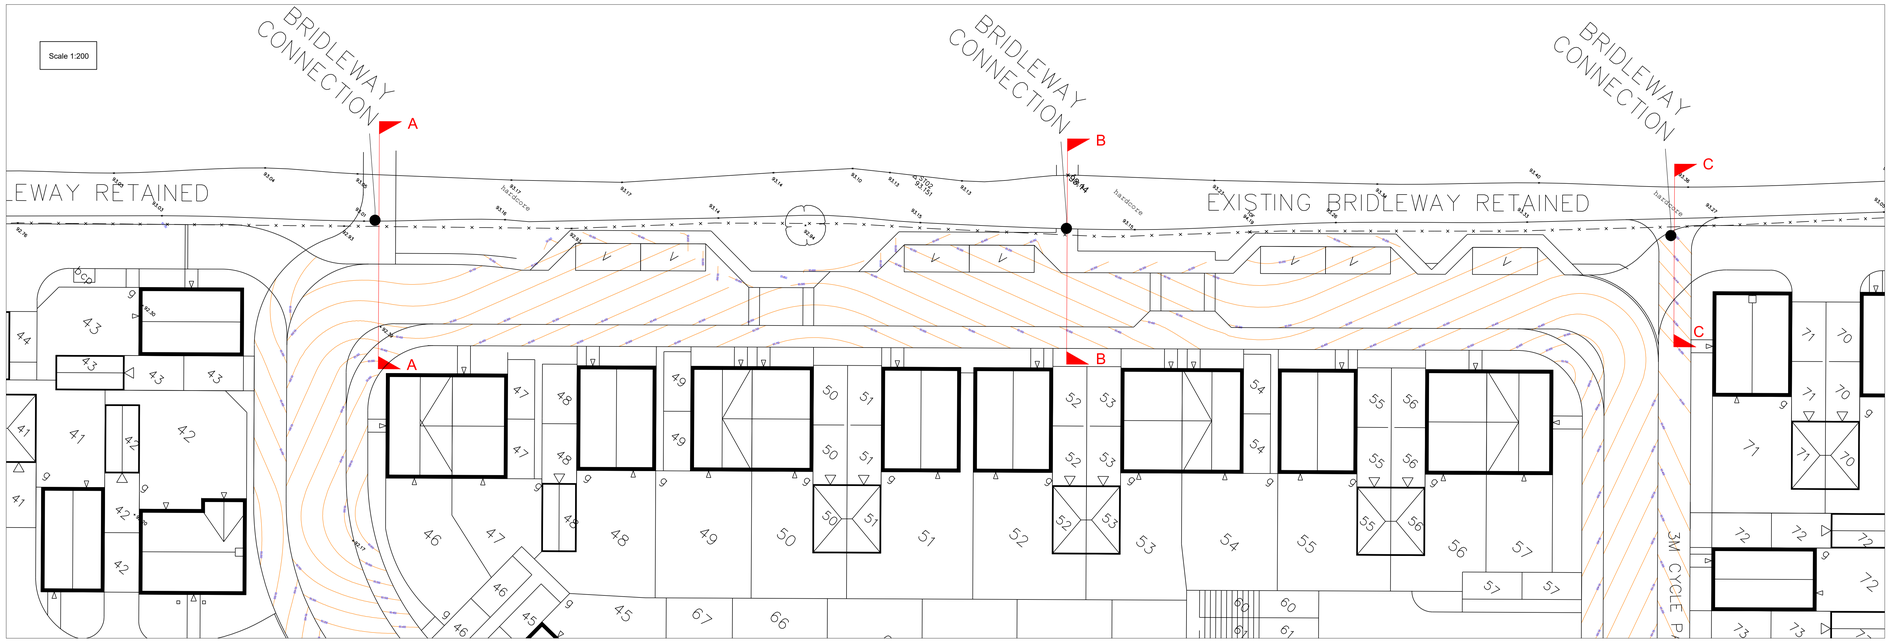

REV	DATE	DESCRIPTION	DRAWN
A	24.10.24	Planning Layout Update	DM

PROJECT Swindon NEV
R8 & R9

TITLE
Bridleway Section

Taylor Wimpey Bristol
Ground Floor
730 Waterside Drive
Aztec West
Almondsbury
Bristol BS31 2AU

T 01454 628400
F 01454 628401
DX 124894 Almondsbury 3

www.taylorwimpey.com
NHBC REG No 76463

Taylor Wimpey

DRN	D Morgan	SCALE	LAND CODE	DRAWING NUMBER	REV
DATE	Oct 24		20933	53-01	A

Paper Size - ISO A0 (841.00 x 1189.00 MM)
C:\Users\DMorgan\Taylor Wimpey\Bristol Technical Team - Documents\General\cur-site\20933 Skylark, Woodlands, NEV Swindon\03-Design\03-Engineering\53-01-Bridleway-X-sections.dwg