1335-DR-03

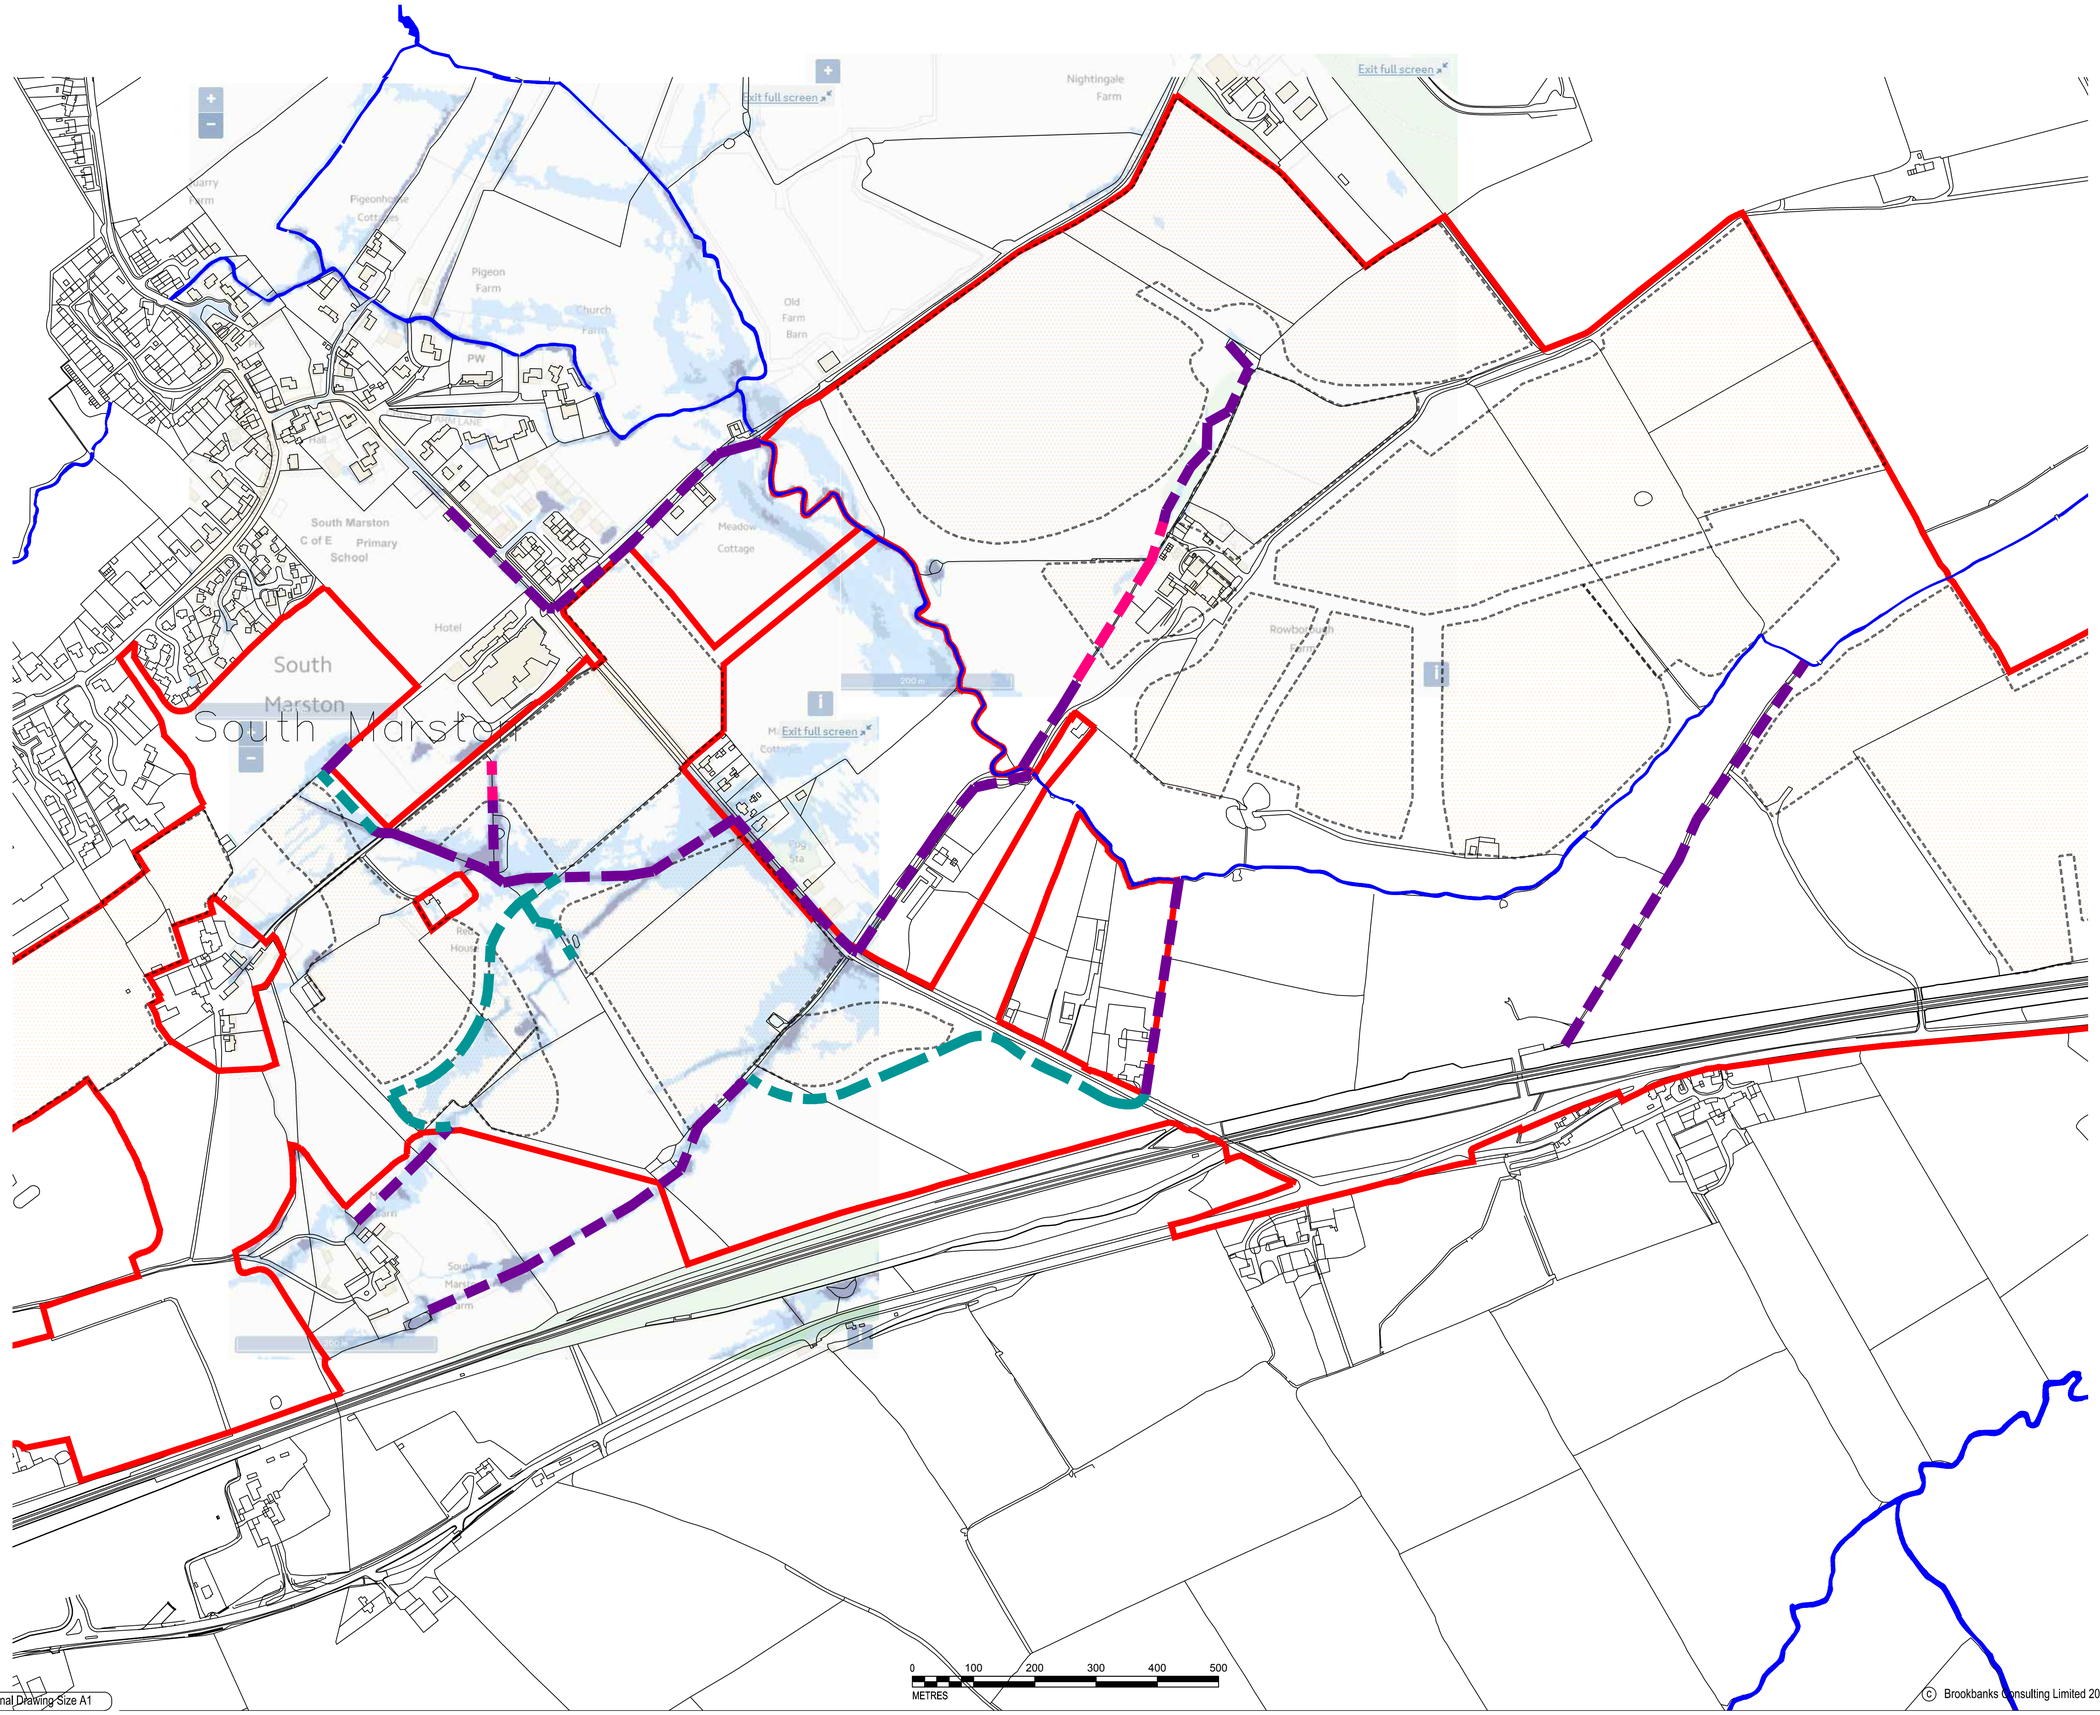

Notes:

1) Do not scale from this drawing.
2) The Data contained within this survey has been collected by a third party. Brookbanks Consulting Ltd accept no responsibility for the accuracy of this data.
3) The locations of the features shown on this plan are conceptual and subject to amendments during detailed design.

KEY

- Site Boundary
- River Cole
- South Marston Brook
- Secondary Catchment
- Existing Surfacewater flow route
- Redirection of Surfacewater route along green route
- Positive drainage system to be placed in parcel to connect natural drainage route.

N

Rev.	Revision Details	Drawn	Checked	Approved	Date
	PRELIMINARY	PAB			09.28.17

Issue Status			Approved	Date
Drawn CA	Checked DW		Date	Sep 17

Brookbanks Consulting

6150 Knights Court Solihull Parkway Birmingham B37 7WY
Tel (0121) 329 4330 Fax (0121) 329 4331
www.brookbanks.com

Swindon eDA Consortium

Proposed Development
Swindon EV Phase 1

Conceptual Drainage Plan
Redirection of Surfacewater route

Scale at A1	Drawing No.	Rev.
1:5,000	1335-DR-03	G

Original Drawing Size A1

© Brookbanks Consulting Limited 2017