1335/HL/58

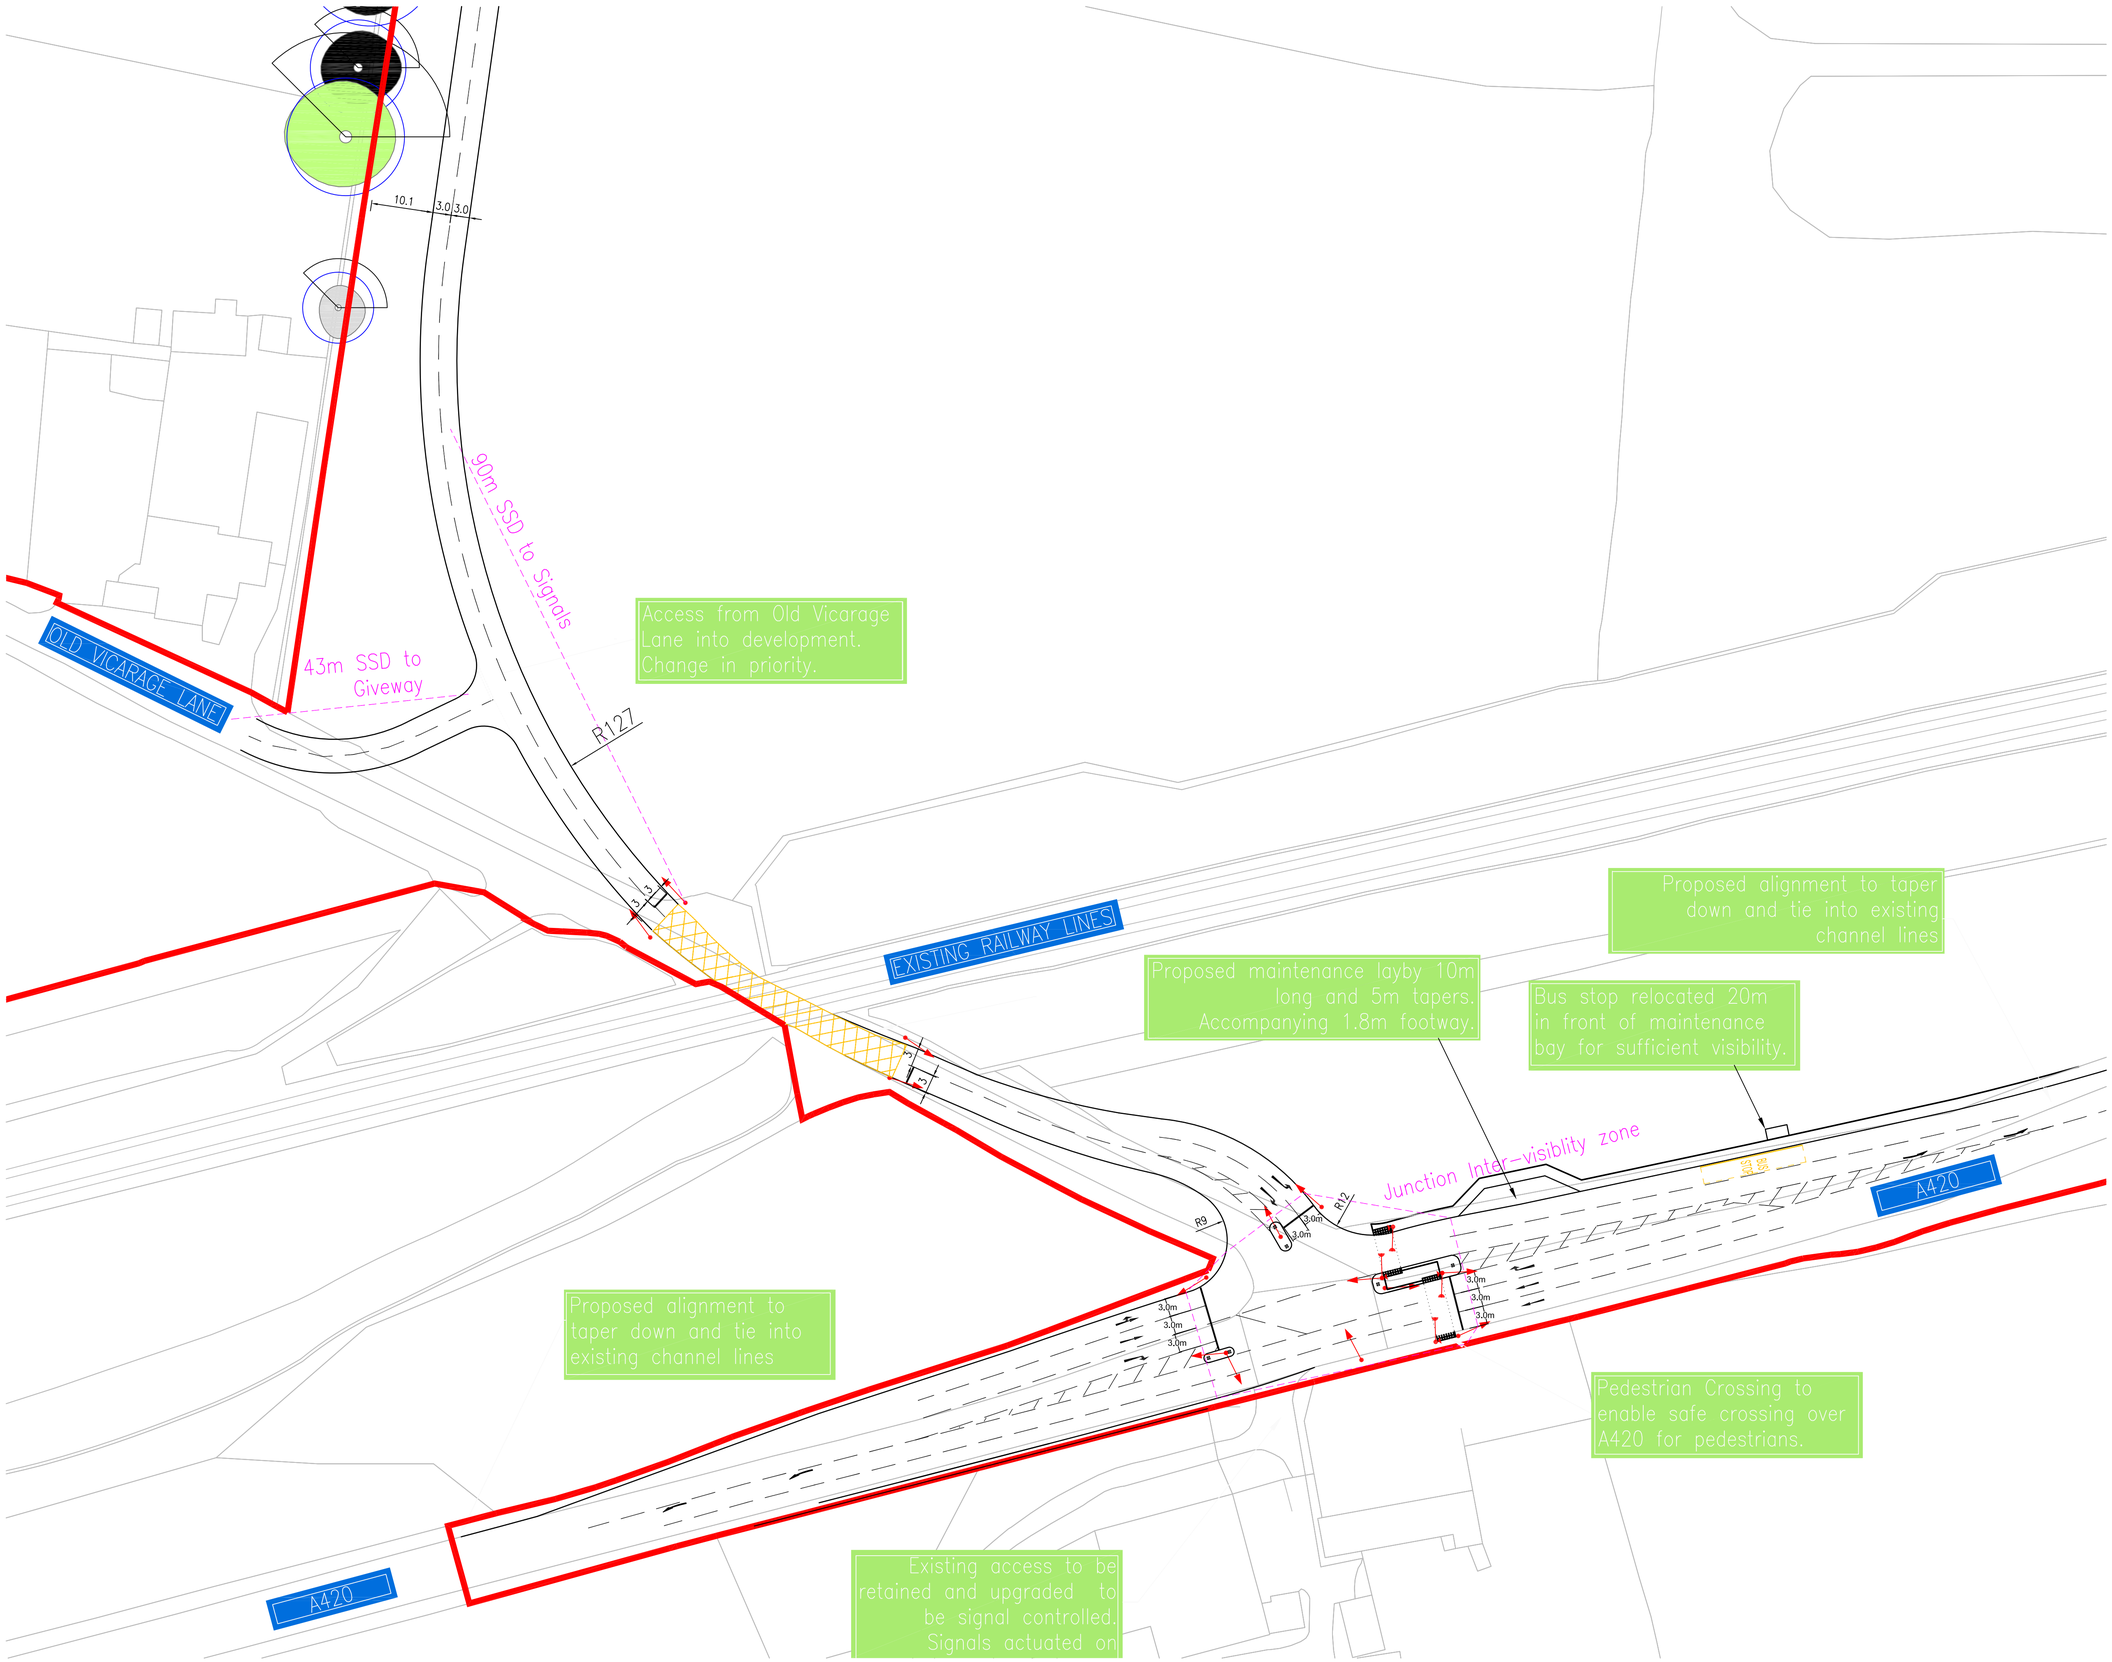

NOTES:
1. Do not scale from this drawing.
2. This drawing has been based on survey data provided by a third party. Brookbanks Consulting Ltd cannot be held respondible for the accuracy of this data.
3. Details shown are for information only and subject to change following completion of the detailed design.

KEY:
Existing Highway Boundary
Traffic Signal

Rev.	Revision Details	Drawn	Checked	Approved	Date
					22.08.16

Issue Status			Approved	Date
Drawn	MDM	Checked DS	Date	AUG 16

Brookbanks Consulting

6150 Knights Court Solihull Parkway Birmingham B37 7WY
Tel (0121) 329 4330 Fax (0121) 329 4331
www.brookbanks.com

Swindon EDAG

Swindon EDA

OPTION 3 (WITH CROSSING)
PROPOSED JUNCTION WITH A420

Scale at A1	Drawing No.	Rev.
1:500	1335/HL/72	B

Original Drawing Size A1

© Brookbanks Consulting Limited 2013