1335/HL/58

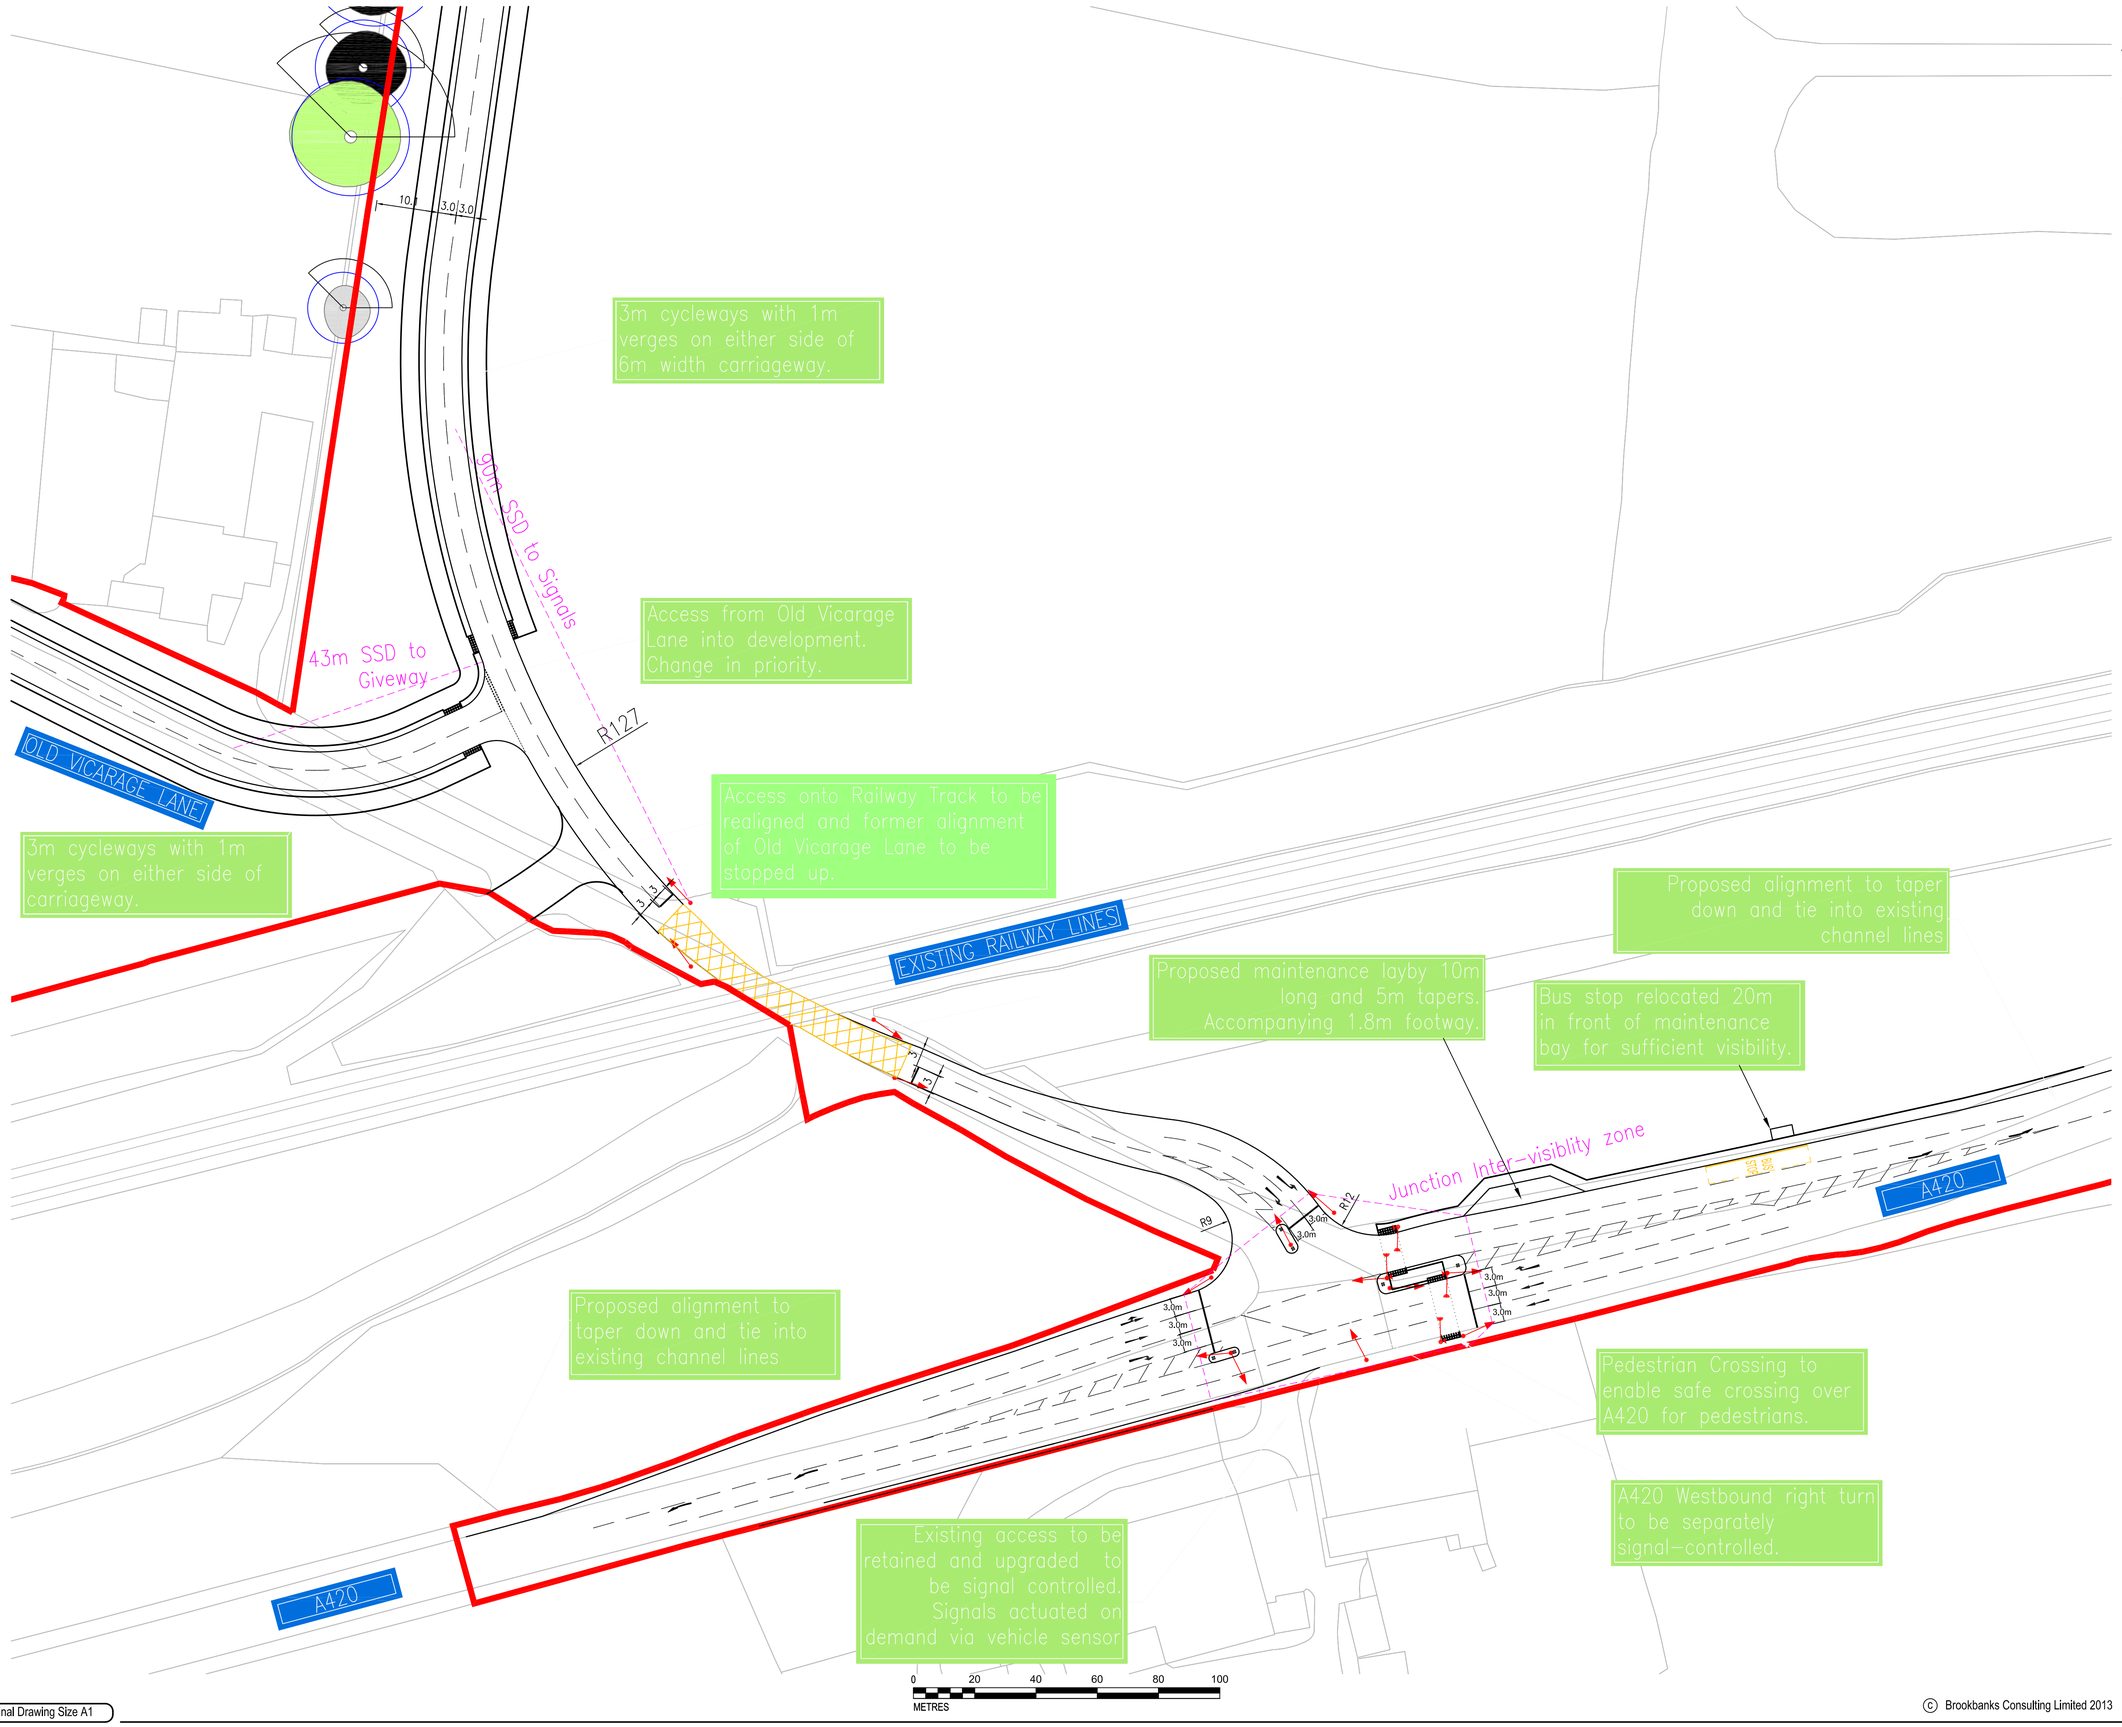


NOTES:
1. Do not scale from this drawing.
2. This drawing has been based on survey data provided by a third party. Brookbanks Consulting Ltd cannot be held responsible for the accuracy of this data.
3. Details shown are for information only and subject to change following completion of the detailed design.

KEY:
Existing Highway Boundary
Traffic Signal

| Rev. | Revision Details | Drawn | Checked | Approved | Date |
|---|---|---|---|---|---|
| | | | | | 22.08.16 |

| Issue Status | | | Approved | Date |
|---|---|---|---|---|
| Drawn | MDM | Checked DS | Date | AUG 16 |

Brookbanks Consulting

6150 Knights Court Solihull Parkway Birmingham B37 7WY
Tel (0121) 329 4330 Fax (0121) 329 4331
www.brookbanks.com

Swindon EDAG

Swindon EDA

OPTION 3 (WITH CROSSING)
PROPOSED JUNCTION WITH A420

| Scale at A1 | Drawing No. | Rev. |
|---|---|---|
| 1:500 | 1335/HL/72 | C |

Original Drawing Size A1

© Brookbanks Consulting Limited 2013