Plant Schedule

Trees					
Number	Abbreviation	Species	Height	Girth	Specification
10	AIRH	Amelanchier lamarckii 'Robin Hill'	250-300cm	12-14cm	Heavy Standard ,Clear Stem min. 200 ,RB
8	Bn	Betula nigra	350-425cm	14-16cm	Heavy Standard ,Clear Stem min. 200 ,RB
13	Bpu	Betula pubescens	350-425cm	14-16cm	Heavy Standard ,Clear Stem min. 200 ,RB
20	Cbe	Carpinus betulus	400-450cm	16-18cm	Extra Heavy Standard ,Clear Stem min. 200 ,RB
3	CbL	Carpinus betulus 'Lucas'	350-425cm	14-16cm	Heavy Standard ,Clear Stem min. 200 ,RB
20	Ccol	Corylus colurna	350-425cm	14-16cm	Heavy Standard ,Clear Stem min. 200 ,RB
1	Ls	Liquidambar styraciflua	350-425cm	16-18cm	Extra Heavy Standard ,Clear Stem min. 200 ,RB
8	IPP	Prunus 'Pandora'	350-425cm	14-16cm	Heavy Standard ,Clear Stem min. 200 ,RB
2	Pav	Prunus avium	400-450cm	16-18cm	Extra Heavy Standard ,Clear Stem min. 200 ,RB
3	Pv	Prunus yedoensis	400-450cm	16-18cm	Extra Heavy Standard ,Clear Stem min. 200 ,RB
2	PCc	Pyrus calleryana 'Chanticleer'	400-450cm	16-18cm	Extra Heavy Standard ,Clear Stem min. 200 ,RB
10	SaLu	Sorbus aria 'Lutescens'	350-425cm	12-14cm	Heavy Standard ,Clear Stem min. 200 ,RB
4	Sau	Sorbus aucuparia	350-425cm	14-16cm	Heavy Standard ,Clear Stem min. 200 ,RB
9	SaCR	Sorbus aucuparia 'Cardinal Royal'	350-425cm	12-14cm	Heavy Standard ,Clear Stem min. 200
Total :111					

Shrubs						
Number	Abbreviation	Species	Specification	Height	Pot Size	Density
14	EfEG	Euonymus fortunei 'Emerald Gaiety'	Bushy ,BR	30-40cm	3L	4/m²
46	PtGB	Pittosporum tenuifolium 'Golf Ball'	Bushy ,BR	20-30cm	3L	4/m²
33	VtEP	Viburnum tinus 'Eve Price'	Bushy ,BR	30-40cm	3L	4/m²
Total :93						

Herbaceous					
Number	Abbreviation	Species	Specification	Pot Size	Density
61	NSHG	Nepeta 'Six Hills Giant'	Full Pot	3L	5/m²
Total :61					

Climbers						
Number	Abbreviation	Species	Specification	Height	Pot Size	Density
3	Hp	Hydrangea petiolaris	Several Shoots ,3/5 brks ,Canes	80-100cm	3L	Counted
3	PVe	Parthenocissus tricuspidata 'Veitchii'	Several Shoots ,3/5 brks ,Canes	80-100cm	3L	Counted
Total :6						

Single species hedgerow planting

Number of Plants	Abbreviation	Species	Specification	Height	Pot Size	Density
1296	El	Escallonia 'Iveyi'	Bushy ,C	60-80cm	3L	0.45/Cir Double Staggered at 0.45m offset
835	Gi	Griselinia littoralis	Bushy ,C	60-80cm	3L	0.45/Cir Double Staggered at 0.45m offset
20	Tb	Taxus baccata	Bushy	60-80cm	3L	0.45/Cir Double Staggered at 0.45m offset
Total :2081						

Native hedgerow mix 01

Number	Abbreviation	Species	Height	Specification	Density	Percentage
68	Ac	Acer campestre	60-80cm	Transplant ,Bushy ,BR	0.45/Cir Double Staggered at 0.45m offset	10%
68	Csa	Cornus sanguinea	60-80cm	Bushy ,BR	0.45/Cir Double Staggered at 0.45m offset	10%
68	Cav	Corylus avellana	60-80cm	Bushy ,BR	0.45/Cir Double Staggered at 0.45m offset	10%
394	C mon	Crataegus monogyna	60-80cm	Transplant ,Bushy ,BR	0.45/Cir Double Staggered at 0.45m offset	60%
68	Eeu	Euonymus europaeus	60-80cm	Transplant ,Bushy ,BR	0.45/Cir Double Staggered at 0.45m offset	10%
Total :666						

Ornamental Plot mix 1

Number	Abbreviation	Species	Specification	Density	Percentage Contribution
1258	BcP	Bergenia cordifolia 'Purpurea'	Full Pot	5/m²	30%
694	Cbuc	Carex buchananii	Full Pot	4/m²	20%
1341	EfEG	Euonymus fortunei 'Emerald Gaiety'	Bushy ,BR	4/m²	40%
369	Lni	Luzula nivea	Full Pot	4/m²	10%
Total :3662					

Ornamental mix 2

Number	Abbreviation	Species	Specification	Density	Percentage Contribution
22	AJR	Aucuba japonica 'Rozannie'	Bushy ,BR	4/m²	15%
44	Cd	Carex Divulsa	Full Pot	6/m²	20%
22	De	Dryopteris erythrosora	Full Pot	4/m²	15%
22	EfSQ	Euonymus fortunei 'Silver Queen'	Bushy ,BR	4/m²	15%
16	Gn	Geranium nervosum	Full Pot	4/m²	10%
45	Lni	Luzula nivea	Full Pot	6/m²	25%
Total :171					

Ornamental Plot mix 3

Number	Abbreviation	Species	Specification	Density	Percentage Contribution
577	Cd	Carex Divulsa	Full Pot	6/m²	20%
577	De	Dryopteris erythrosora	Full Pot	4/m²	30%
393	EfErG	Euonymus fortunei 'Emerald 'n' Gold'	Bushy ,BR	4/m²	20%
577	Gn	Geranium nervosum	Full Pot	4/m²	30%
Total :2124					

Ornamental mix 3

Number	Abbreviation	Species	Specification	Density	Percentage Contribution
154	Ama	Armeria maritima	Full Pot	6/m²	15%
105	Cbuc	Carex buchananii	Full Pot	4/m²	15%
154	EpWS	Echinacea purpurea 'White Swan'	Full Pot	6/m²	15%
72	EfEG	Euonymus fortunei 'Emerald Gaiety'	Bushy ,BR	4/m²	10%
90	GJsB	Geranium ,johnson's Blue'	Full Pot	5/m²	10%
105	LaH	Lavandula angustifolia 'Hidcote'	Bushy ,BR	4/m²	15%
140	Vd	Viburnum davidii	Bushy ,BR	4/m²	20%
Total :820					

Ornamental Plot mix 2

Number	Abbreviation	Species	Specification	Density	Percentage Contribution
184	Cbuc	Carex buchananii	Full Pot	4/m²	20%
262	EfEG	Euonymus fortunei 'Emerald Gaiety'	Bushy ,BR	4/m²	30%
326	HeGG	Hebe 'Green Globe'	Bushy ,BR	5/m²	30%
184	Vd	Viburnum davidii	Bushy ,BR	4/m²	20%
Total :956					

Ornamental Plot mix 4

Number	Abbreviation	Species	Specification	Density	Percentage Contribution
142	Cd	Carex Divulsa	Full Pot	4/m²	25%
171	GRoz	Geranium Rozanne	Full Pot	5/m²	25%
171	Hs	Heuchera sanguinea		5/m²	25%
142	PtSQ	Pittosporum tenuifol. 'Silver Queen'	Bushy ,BR	4/m²	25%
Total :626					

Ornamental Plot mix 5

Number	Abbreviation	Species	Specification	Density	Percentage Contribution
117	Am	Acanthus mollis	Full Pot	4/m²	25%
174	Cd	Carex Divulsa	Full Pot	6/m²	25%
117	EfSQ	Euonymus fortunei 'Silver Queen'	Bushy ,BR	4/m²	25%
117	VtEP	Viburnum tinus 'Eve Price'	Bushy ,BR	4/m²	25%
Total :525					

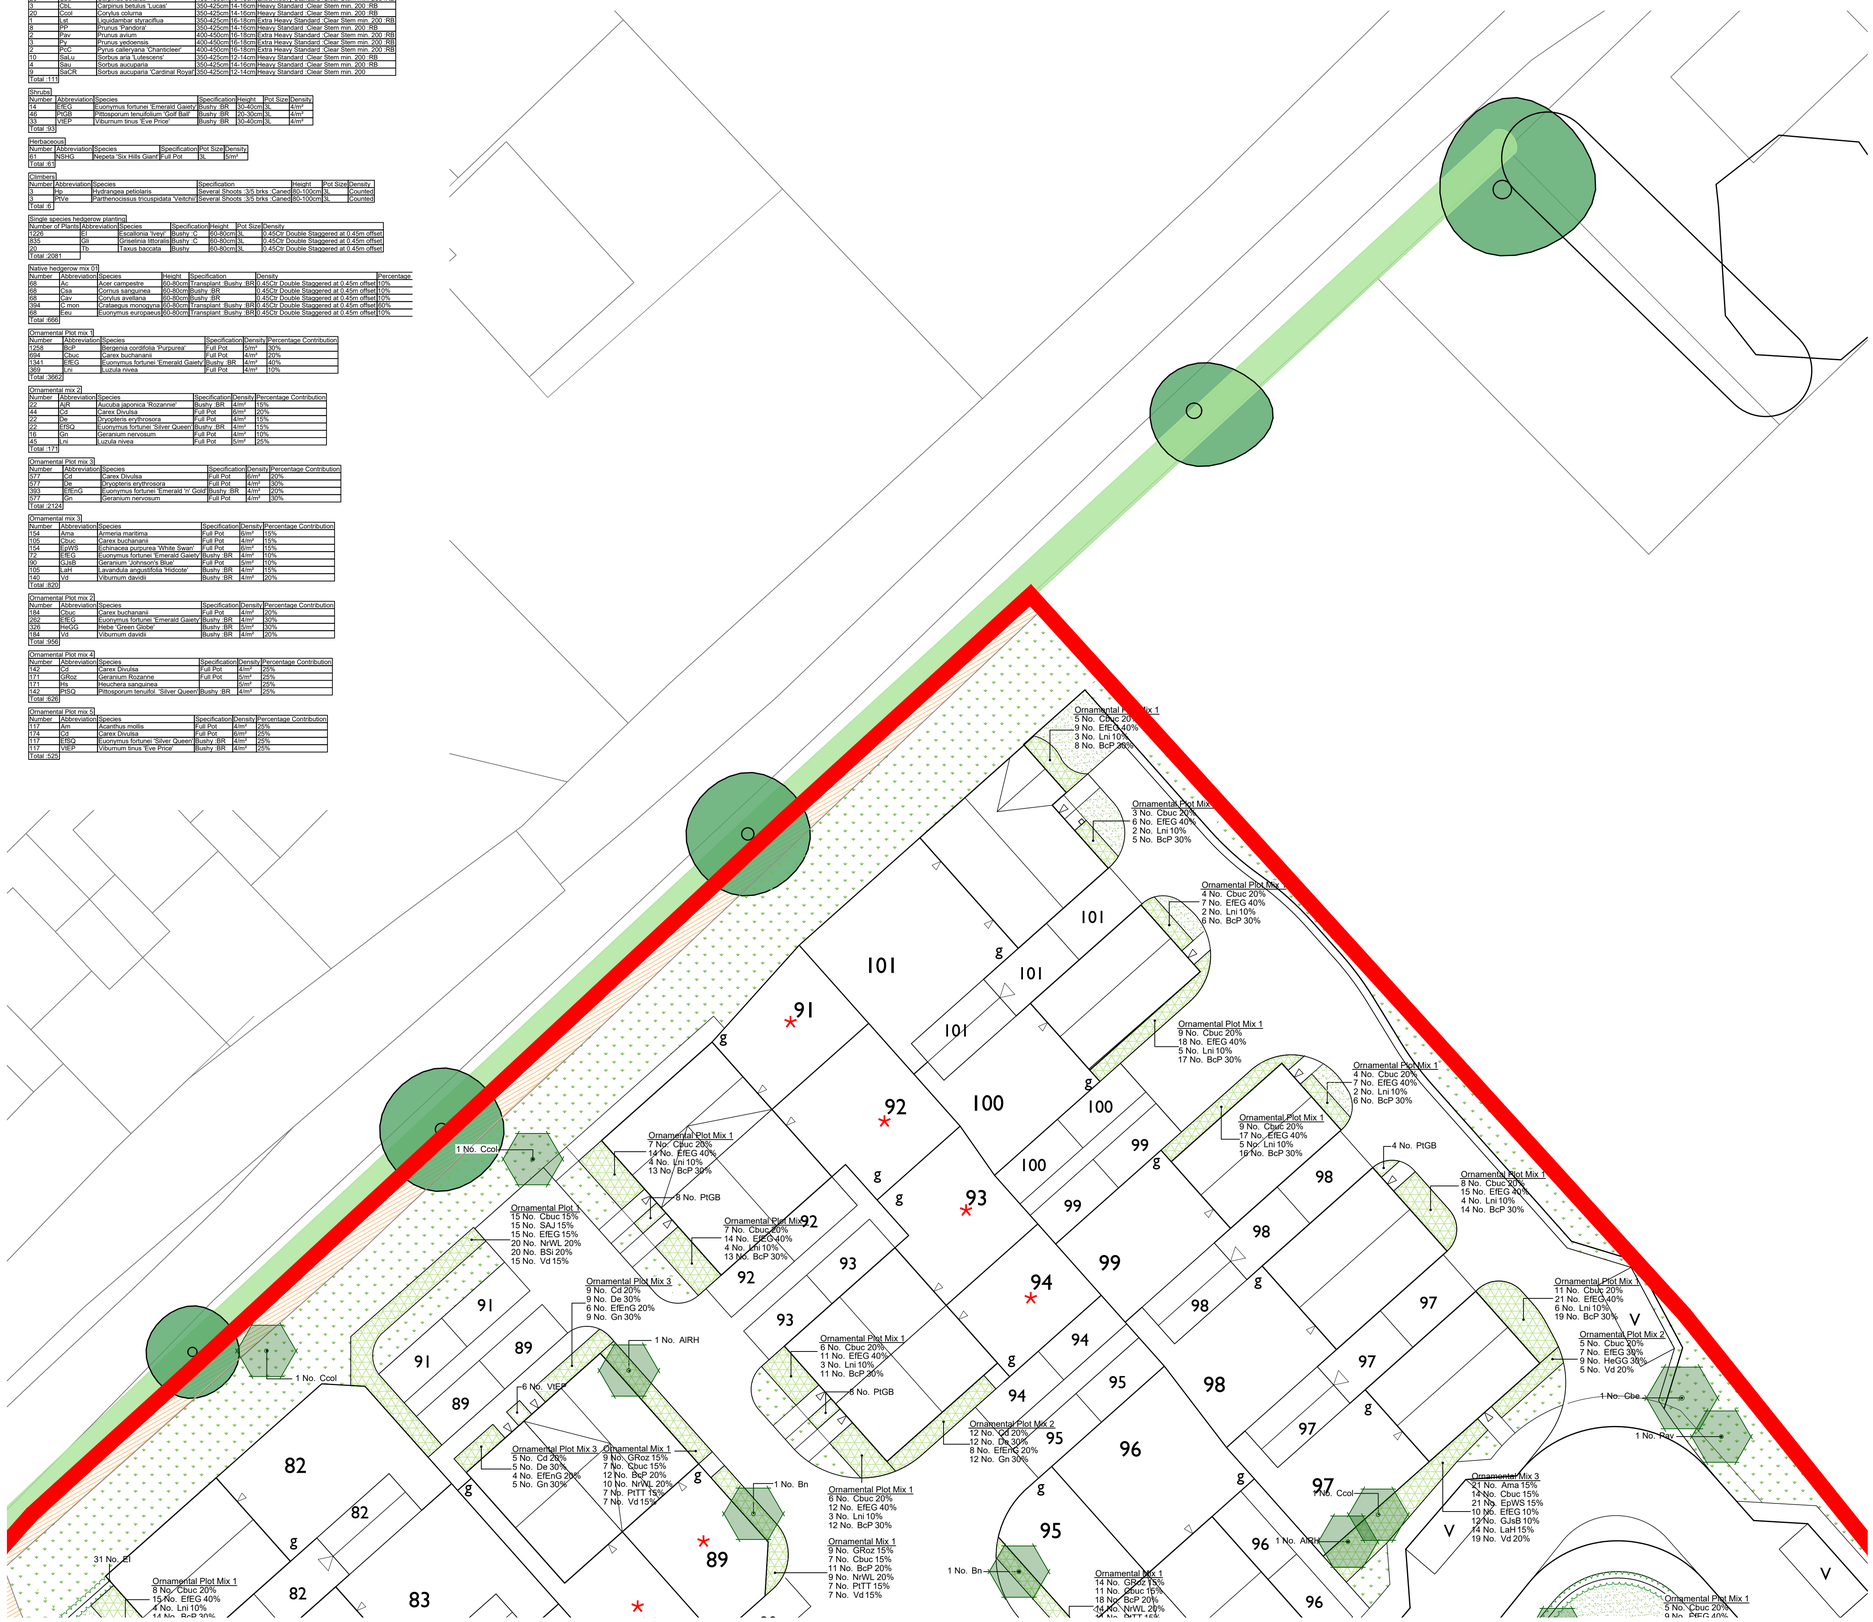

LEGEND

- Site boundary
- Existing tree to be retained and protected. Refer to arboricultural information for further detail
- Existing vegetation and/or hedgerow to be retained and protected. Refer to arboricultural information for further detail
- Existing grassland to be retained and protected. Where disturbed to be seeded in line with proposed grassland seed mix as specified.

Proposed soft landscaping

- Tree planting, refer to detail CB_L_86_263_R8-R9_1700 and 1701
- Ornamental hedge - Double staggered 1.2m high in front gardens and 1.8m high elsewhere
- Double staggered mixed native hedgerow To be planted in groups of 7-9no. of each species
- Ornamental shrub planting single species bed
- Ornamental shrub mix
- Good quality hardwearing lawn
- Mown species rich grassland Verges laid with species rich turf from Wildflower Turf or similar, remaining areas seeded with ELI Flowering Lawn Mixture from Emorsgate or similar seeded at 4g/m2
- Wildflower meadow mix for hedgerow edge EH1 Hedgerow Mixture from Emorsgate or similar seeded at 4g/m2

NOTES:

1. For Planting Schedule refer to drawing CB_L_86_263_R8-R9_1500

To be read in conjunction with:

- Landscape specification CB_L_86_263_R8-R9_1801
- Landscape management plan CB_L_86_263_R8-R9_1802

LOCATION PLAN

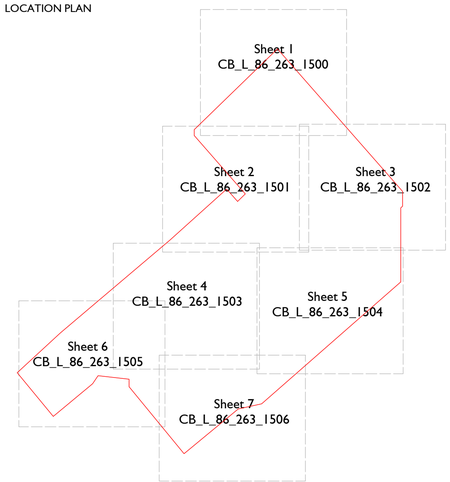

Scale @ A1:
0 1 2 3 4 5 6 7 8 9 10m
Scale 1:200
NORTH

Rev	Date	Drawn	Checked
C	29.07.24	SK	AE
Landscape updated in line with revised layout & comments			
D	06.08.24	SK	AE
Landscape updated in line with comments			

Date: 07.09.22

Drawn by : LM Checked by : AE

Drg No: CB_L_86_263_R8-R9_1500 Rev: D

Project: Woodlands Parcels R8 & R9 Land North of A420, Swindon

Title: Planting Plan Sheet 1

Client: Taylor Wimpey

GREENLANDSCAPE STUDIO

Green Landscape Studio Limited - The Lakeside Centre, Lakeside Country Park, Wide Lane, Eastleigh, Hampshire - Telephone 01276 450039 - www.gl-studio.co.uk
This drawing and the works depicted are the copyright of Green Landscape Studio Ltd. and may not be reproduced or amended except by written permission. No liability will be accepted for amendments made by other persons.