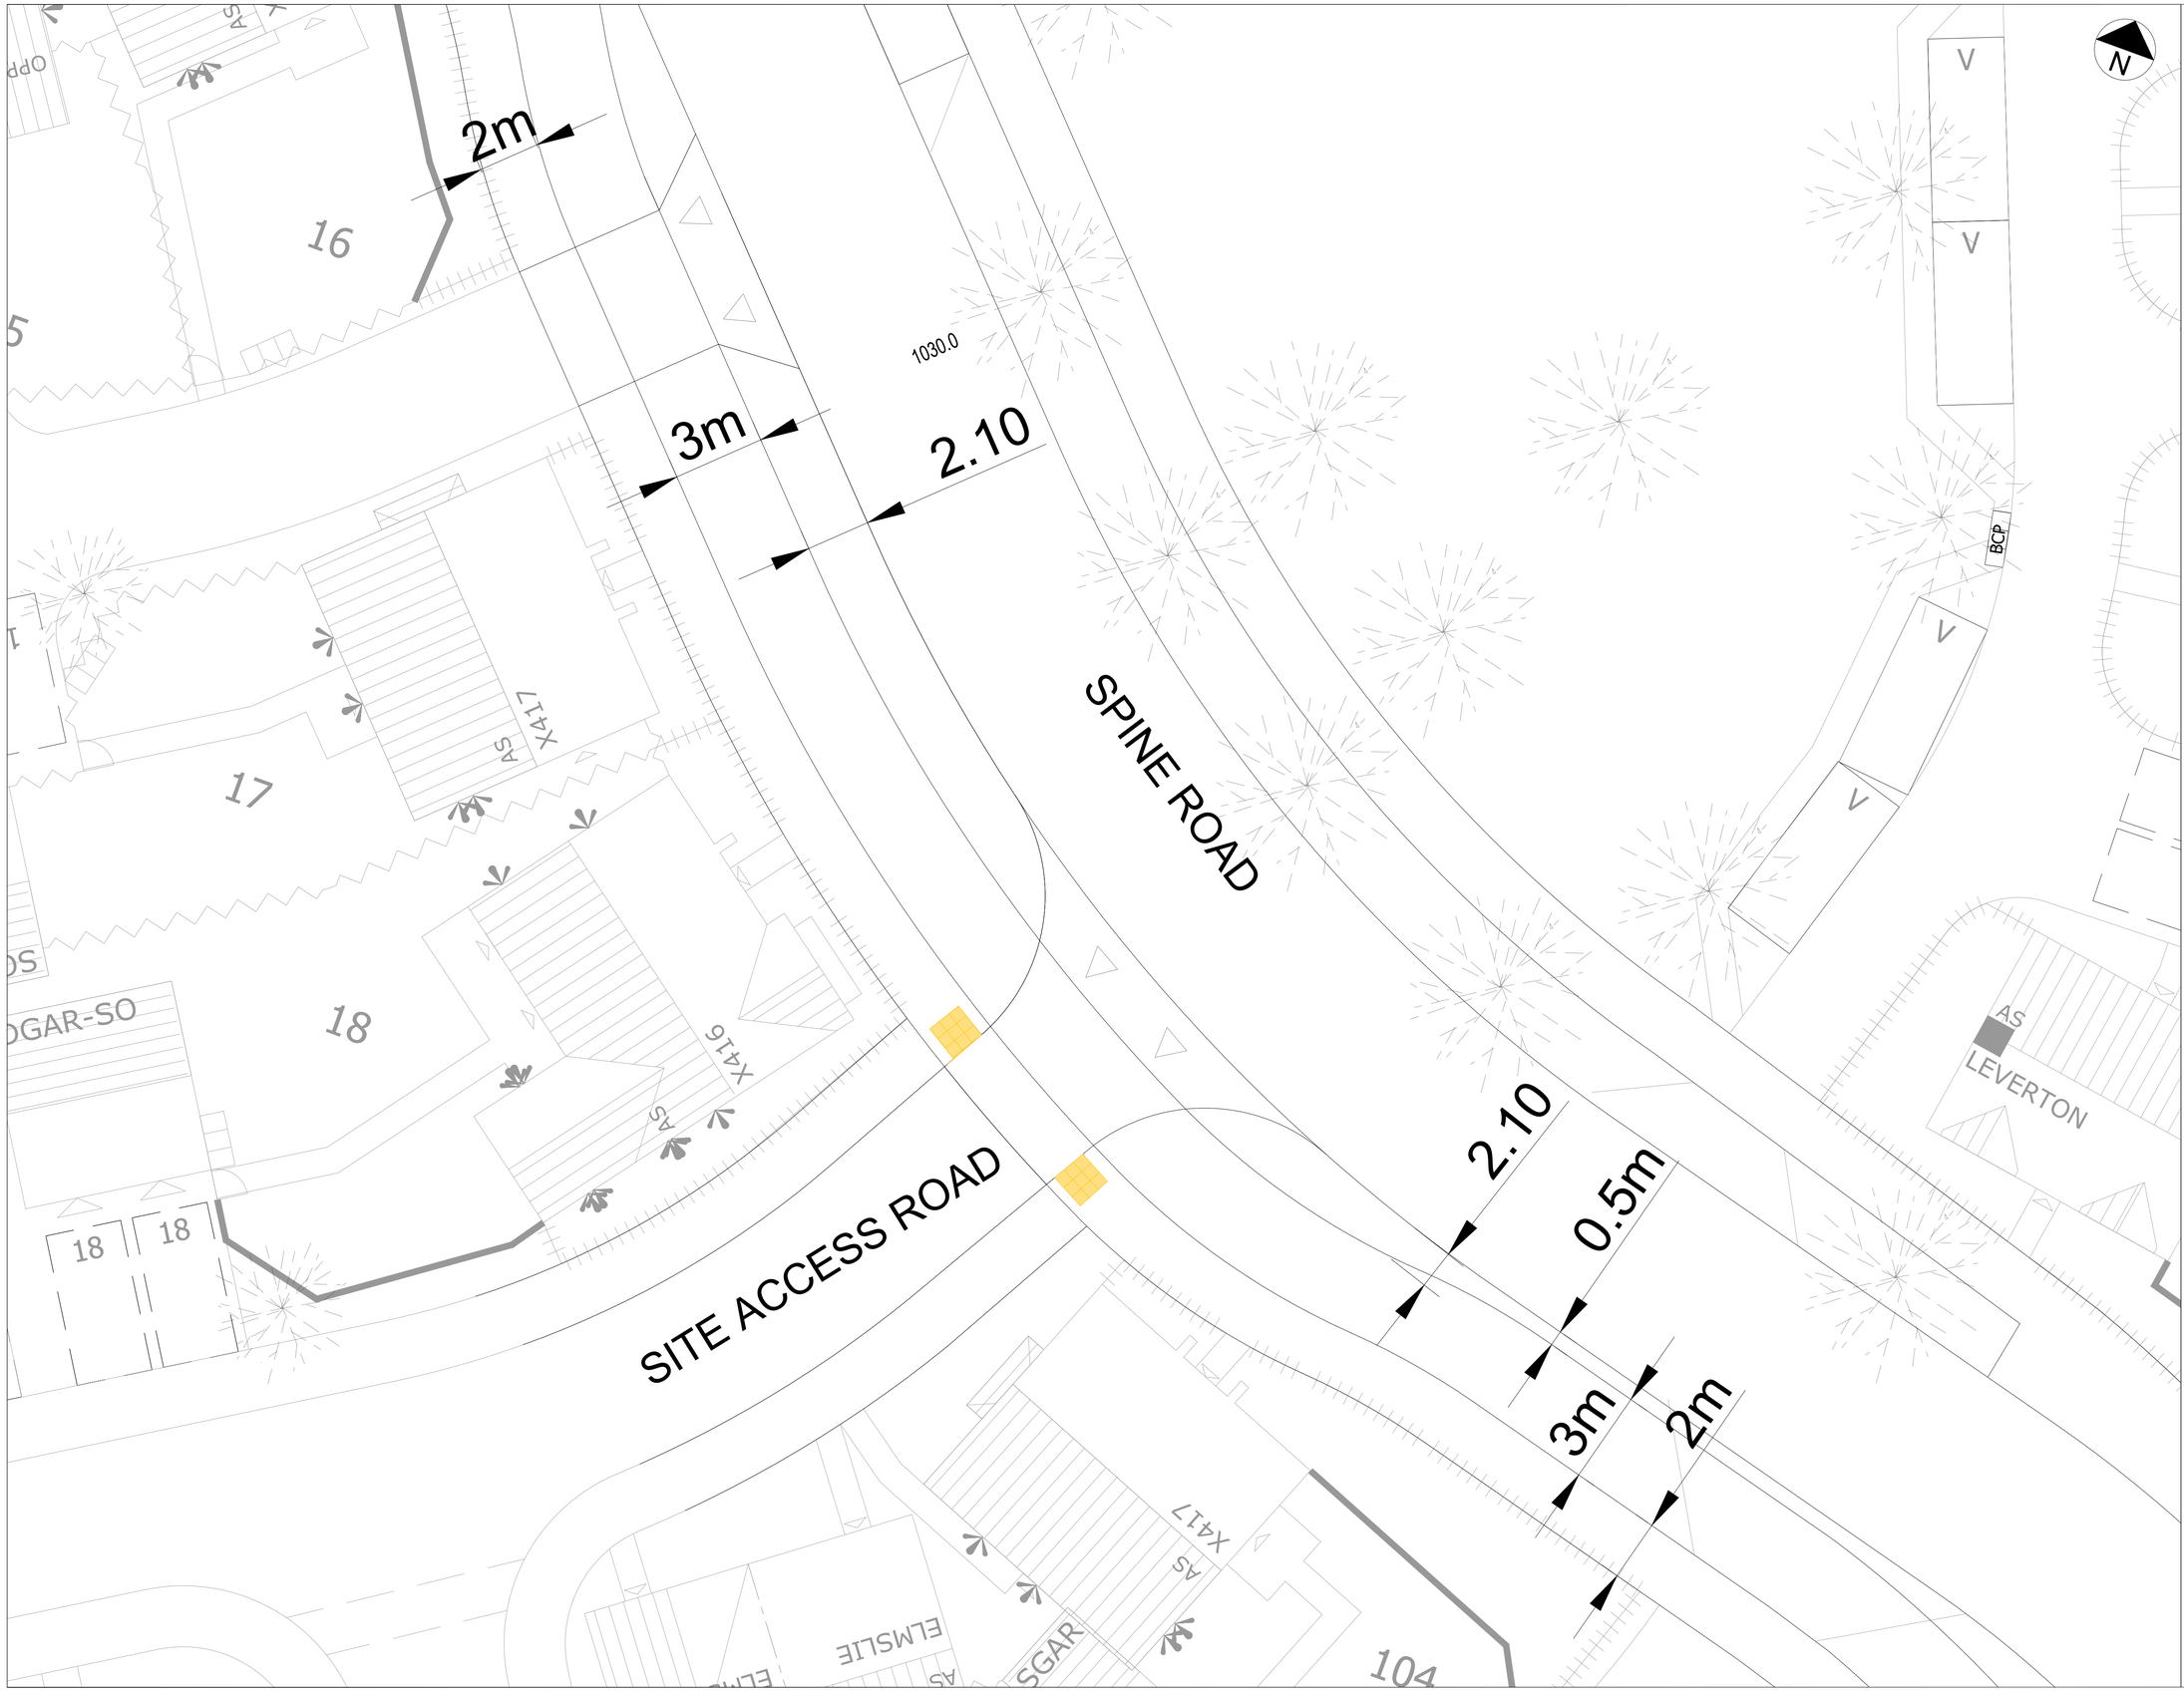

Notes:

1. Do not scale from this drawing. All dimensions are in metres, unless stated otherwise.
2. This drawing is based on the Architect's layout.
3. Ordnance Survey, (c) Crown Copyright 2023. All rights reserved. Licence number 100022432.
4. Drawing to be read in conjunction with all other drawings. Any discrepancies are to be reported to the engineer 5 working days in advance of undertaking any work.
5. Design Subject to S38 Approval.

Rev	Date	Details	By	Chkd
P02	20.11.24	Revised following layout update	DG	JB
P01	15.11.24	First Issue	DG	JB

rappor

rappor.co.uk

CLIENT:
Vistry Homes Ltd.

PROJECT:
Woodlands
South Marston

TITLE:
Cycleway Crossing

SCALE @ A1:	DATE:	DRAWN:	CHECKED:	APPROVED:
1:100	15.11.24	DG	JB	RS

STATUS: PLANNING

DRAWING NO: 240616-RAP-XX-XX-DR-C-0120

REVISION: P02

RESERVED COPYRIGHT