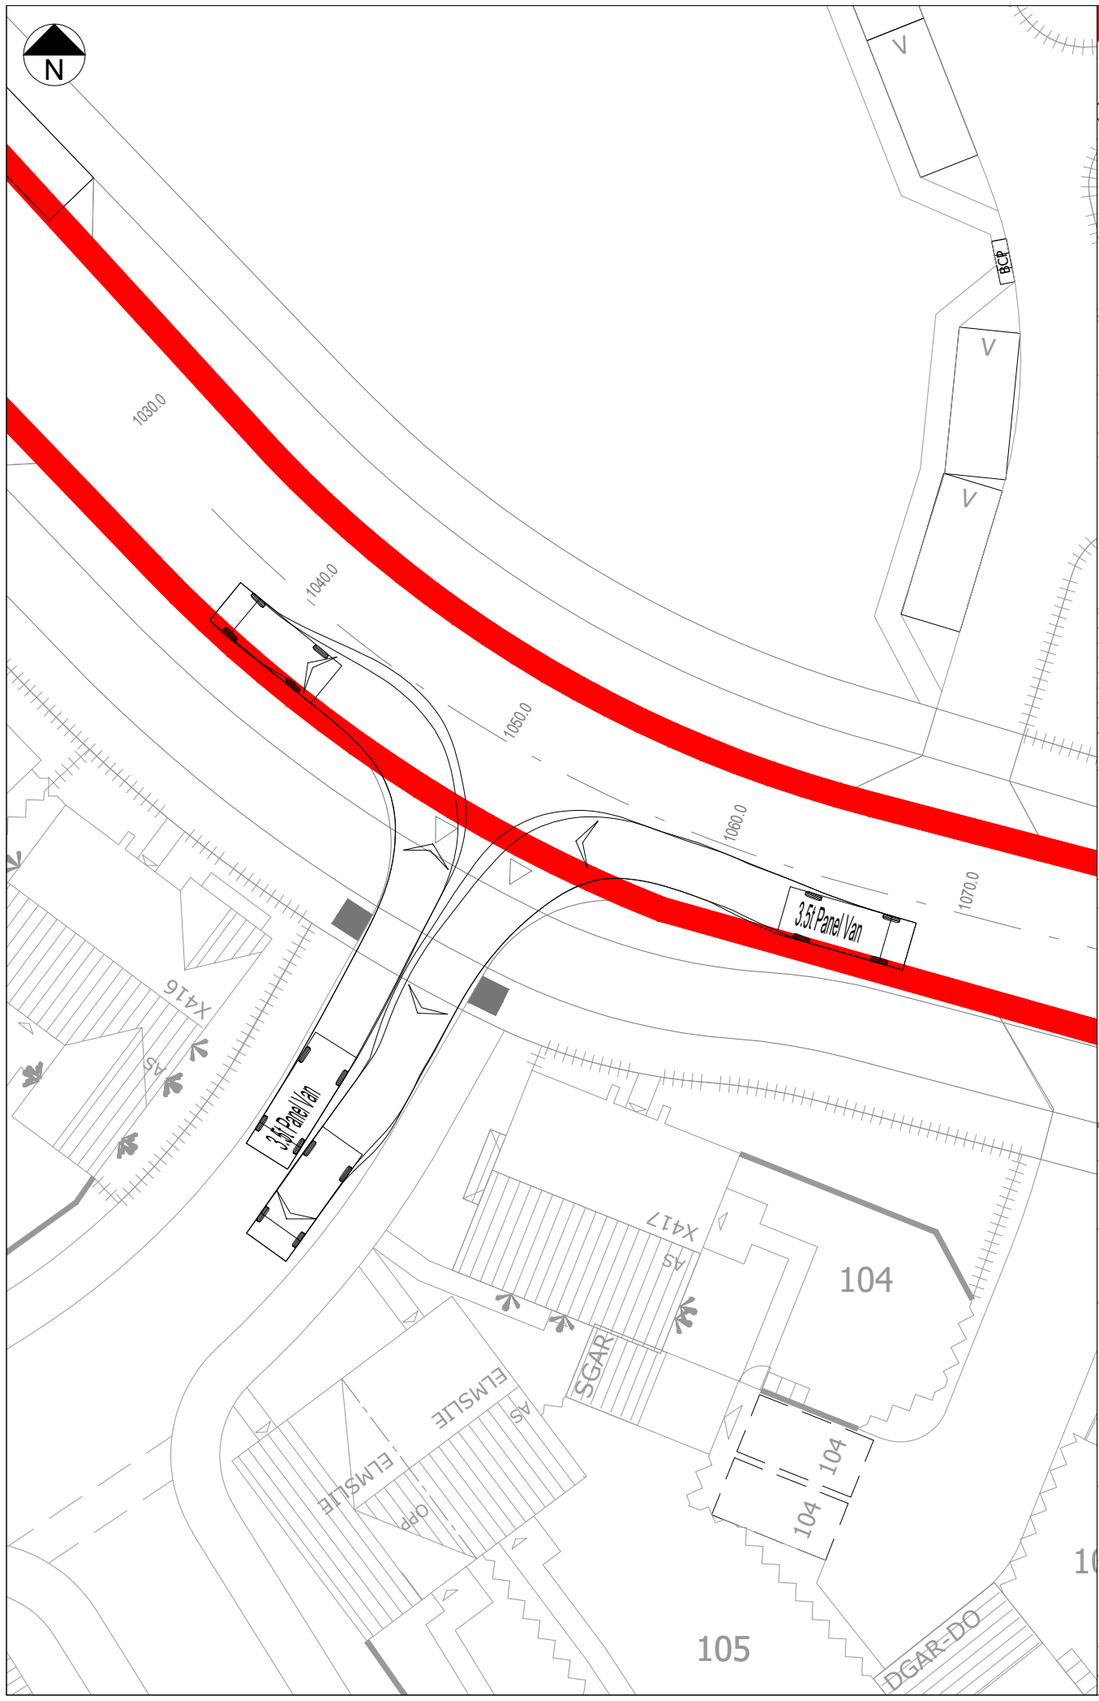

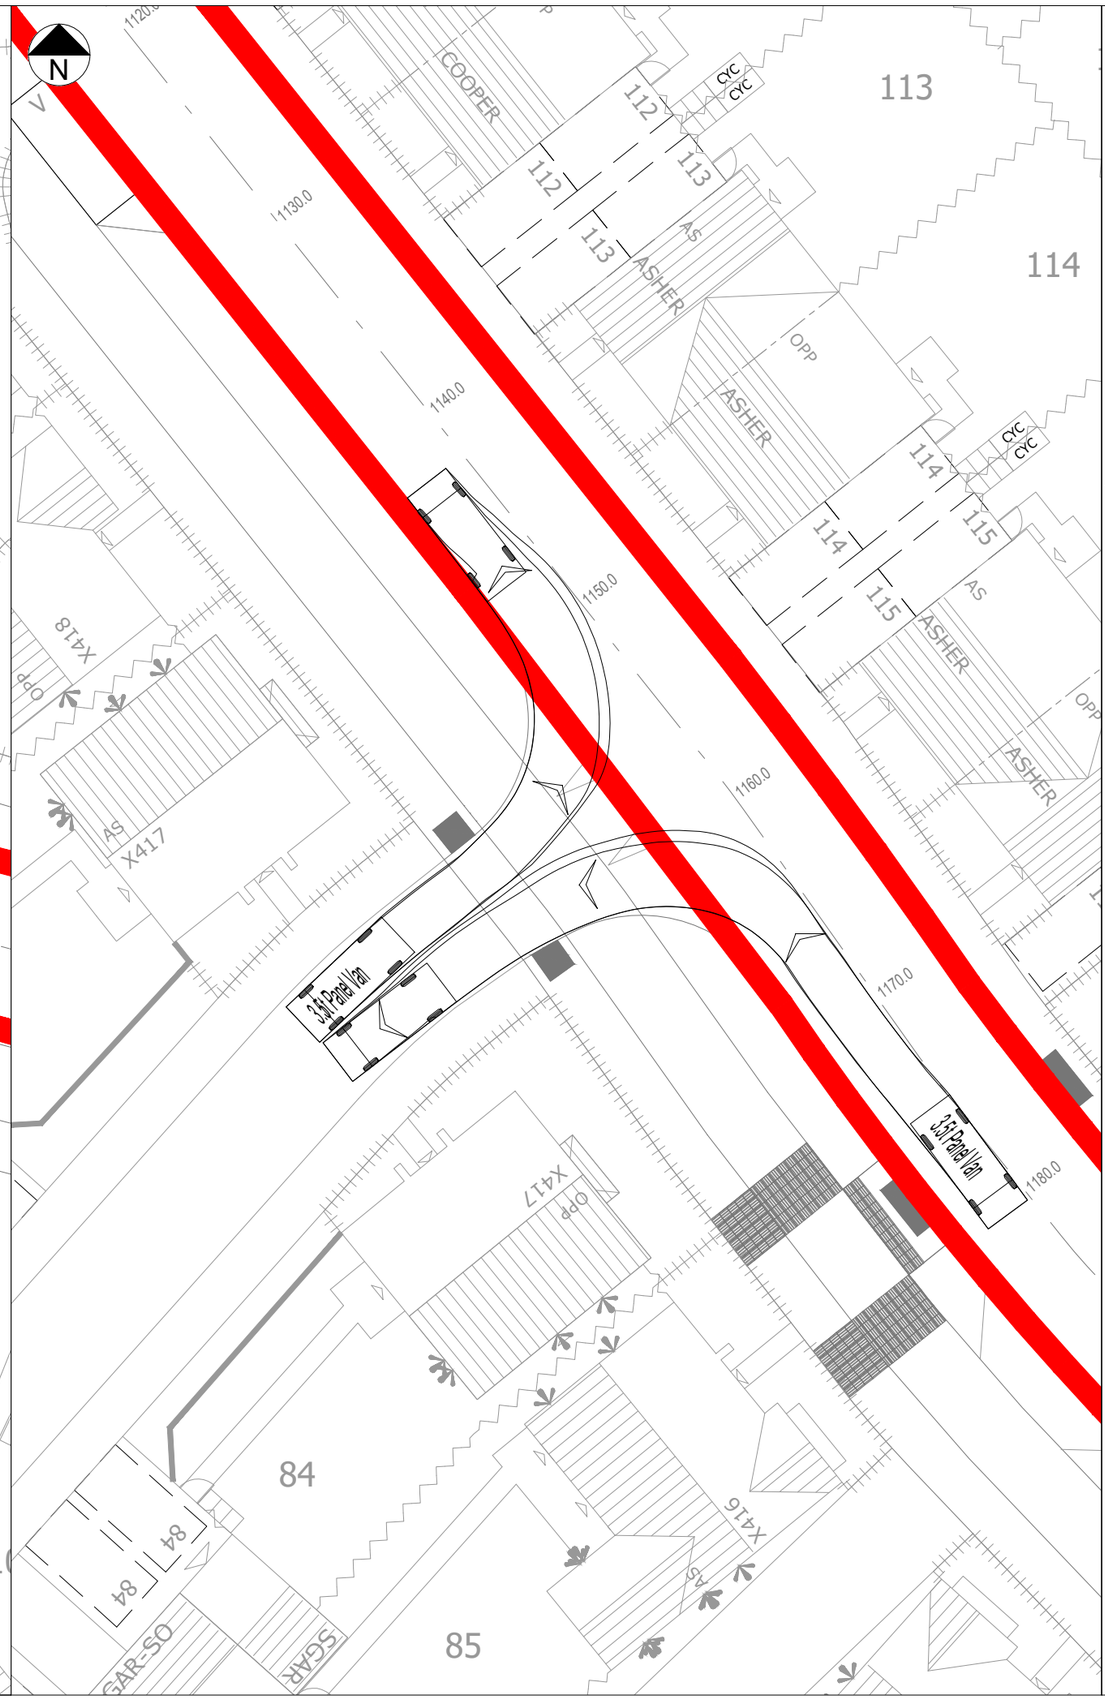

Notes:

1. Do not scale from this drawing. All dimensions are in metres, unless stated otherwise.
2. This drawing is based on the Architect's layout.
3. Ordnance Survey, (c) Crown Copyright 2023. All rights reserved. Licence number 100022432.
4. Drawing to be read in conjunction with all other drawings. Any discrepancies are to be reported to the engineer 5 working days in advance of undertaking any work.

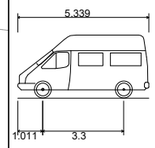

3.5t Panel Van

Overall Length	5.339m
Overall Width	1.986m
Overall Body Height	2.565m
Min Body Ground Clearance	0.338m
Track Width	1.986m
Lock to lock time	4.00s
Kerb to Kerb Turning Radius	6.400m

Rev	Date	Details	By	Chkd
P04	20.11.24	Revised following layout update	DG	JB
P03	14.11.24	New layout added	EB	JB
P02	07.11.24	New layout added	EB	JB
P01	16.10.24	First Issue	RH	RS

rappor

rappor.co.uk

CLIENT:
Vistry Homes Ltd.

PROJECT:
Woodlands
South Marston

TITLE:
Swept Path Analysis
Delivery Van

SCALE @ A3:	DATE:	DRAWN:	CHECKED:	APPROVED:
1:250	16.10.24	RH	RS	RS

STATUS: PLANNING

DRAWING NO: 240616-RAP-XX-XX-DR-C-0104

REVISION: P04

RESERVED COPYRIGHT