Original Drawing Size A1

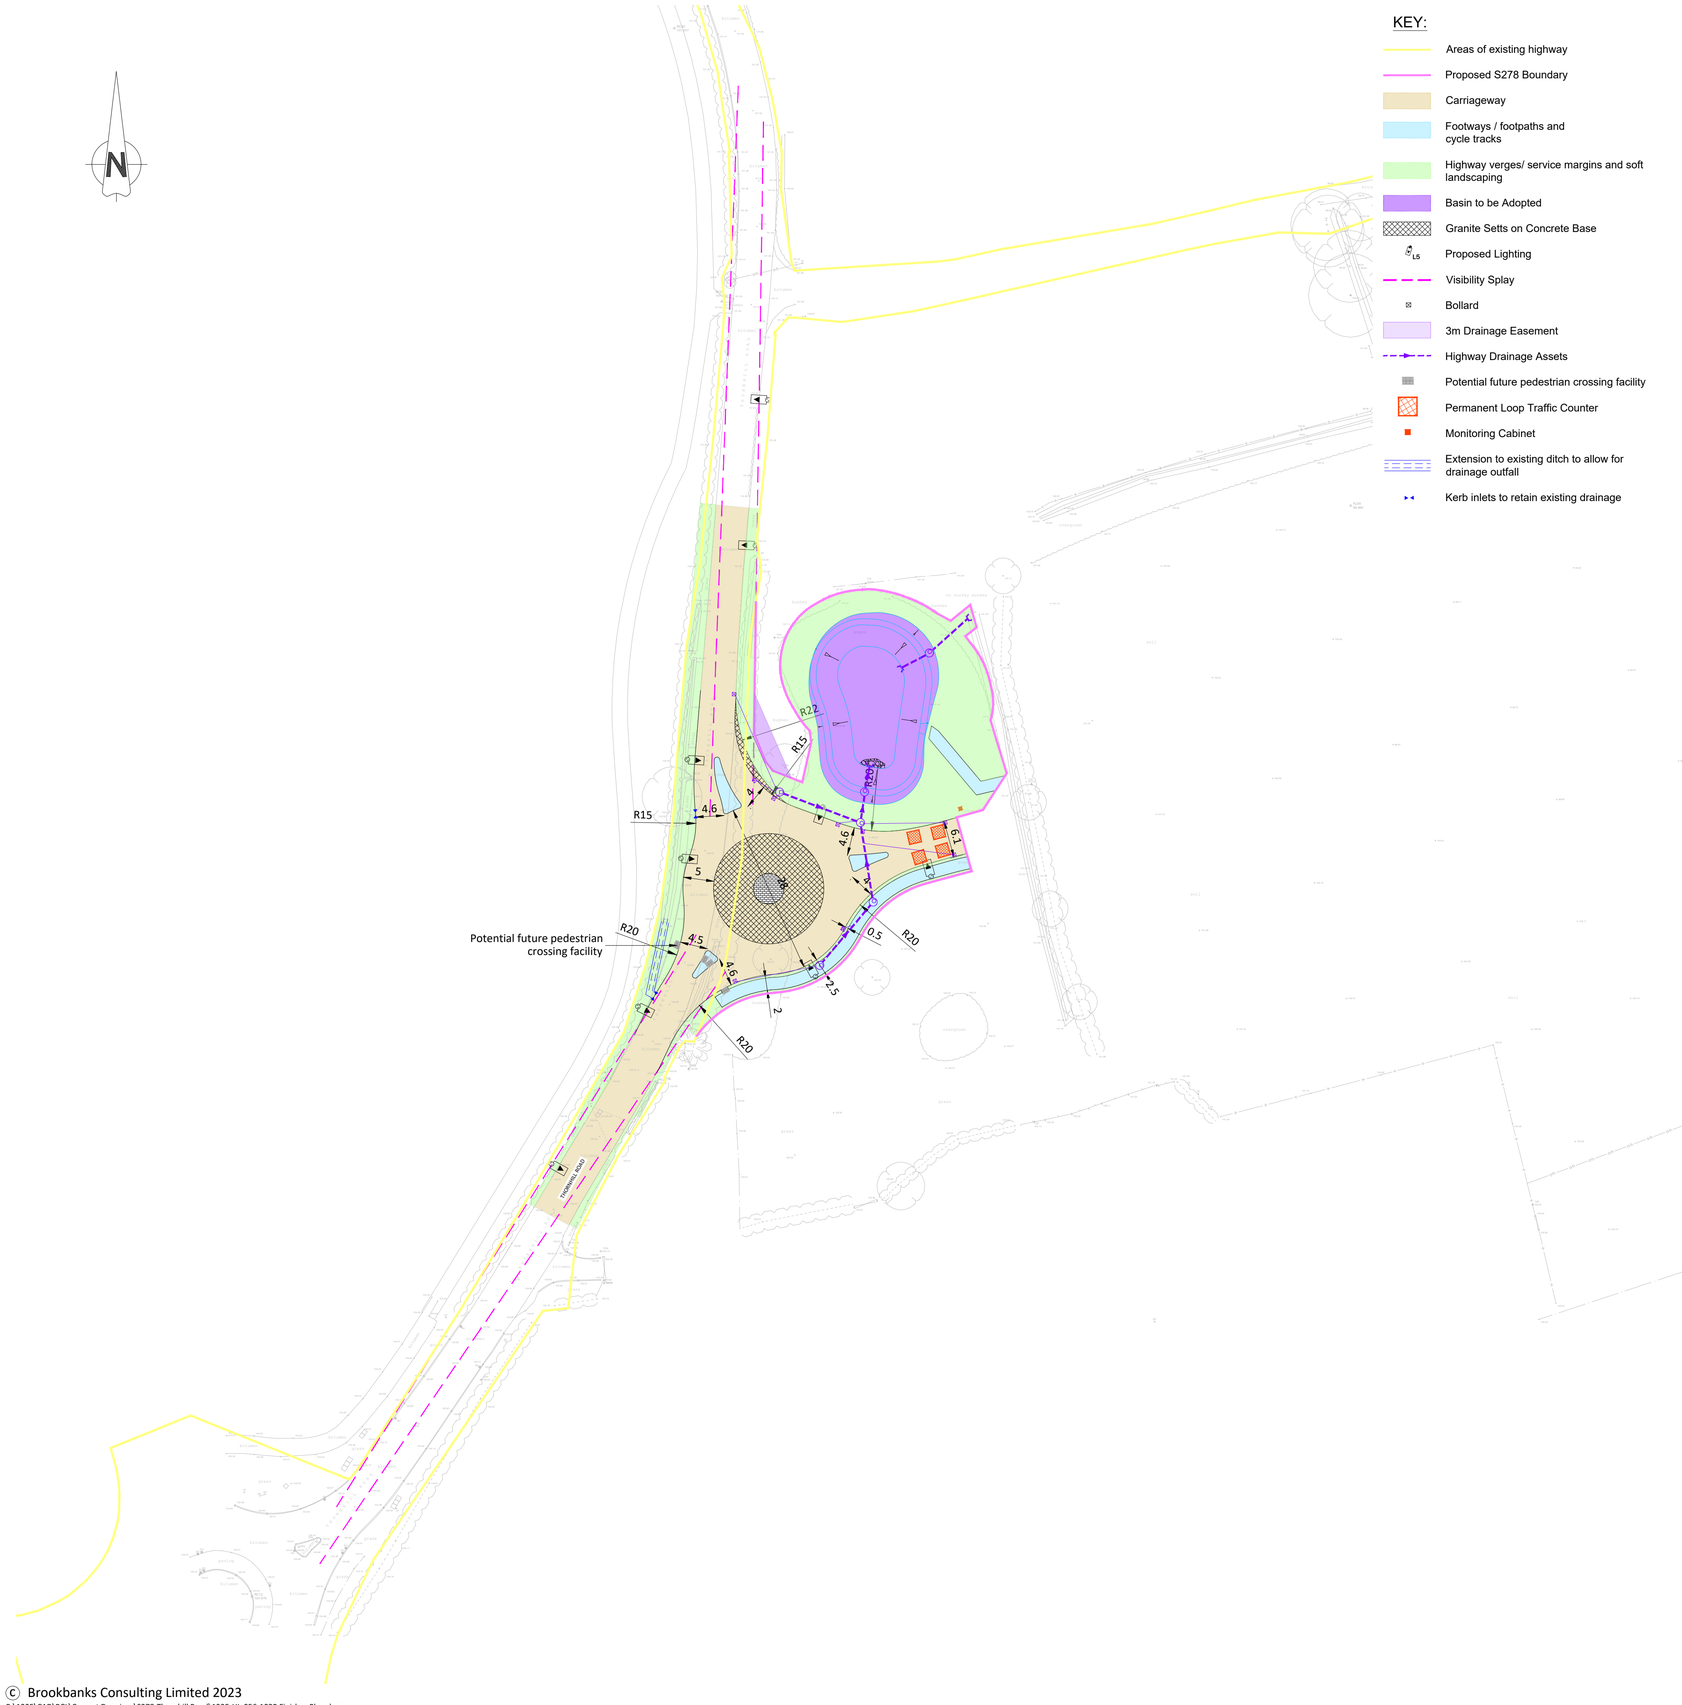

KEY:

- Areas of existing highway
- Proposed S278 Boundary
- Carriageway
- Footways / footpaths and cycle tracks
- Highway verges/ service margins and soft landscaping
- Basin to be Adopted
- Granite Setts on Concrete Base
- Proposed Lighting
- Visibility Splay
- Bollard
- 3m Drainage Easement
- Highway Drainage Assets
- Potential future pedestrian crossing facility
- Permanent Loop Traffic Counter
- Monitoring Cabinet
- Extension to existing ditch to allow for drainage outfall
- Kerb inlets to retain existing drainage

Construction Design and Management (CDM)
Key Residual Risks

Contractors entering the site should gain permission from the relevant land owners and/or principle contractor working on site at the time of entry. Contractors shall be responsible for carrying out their own risk assessments and for liaising with the relevant services companies and authorities. Listed below are Site Specific key risks associated with the project.

1) Overhead and underground services
2) Street Lighting Cables
3) Working adjacent to water courses and flood plain
4) Soft ground conditions
5) Working adjacent to live highways
6) Unchartered services

NOTES:

15. Any areas of existing highway that are affected by the installation of new service trenches/road crossings (including sewers) for any development related purpose are required to be planed and resurfaced, full width (carriageway/footway/cycleway) by the length of the excavation.
16. The Highway Agreement's Clerk of Works is to be present during construction and CBR testing for inspections.
17. All surfacing works shall be completed by machine lay where practical and possible. Including footway and cycleway areas. Hand laying of materials shall be discussed and agreed with SBC in advance of any works being undertaken.
18. Bond coat shall be applied to all new or existing bituminous bound substrate as per MCHW cl.903/6. Bond coat to be C50BP3 applied at a rate of 0.2kg/m2 on newly laid binder/base courses and 0.35kg/m2 on planed surfaces by a metered spray tanker. Bond coat shall comply with BS EN 13808.
19. CBR testing to be undertaken in accordance with BS EN 1377 Part 9 at 25m centres on formation, capping and subbase. Utility and drainage trenches are to also be CBR tested.
20. Where formation CBR results are 2% or less a 500mm to 1000mm capping improvement layer will be required beneath the pavements 600mm capping.
21. CBR Plate Bearing tests shall be carried out on capping materials and shall achieve a minimum of 15%. CBR Plate Bearing tests shall be carried out on type 1 subbase material and shall achieve a minimum of 30%. Where CBR testing is unavailable prior to pavement design an assumed CBR value of 2% is to be used.
22. All capping material shall be 6F5 in accordance with MCHW series 600.All subbase material shall be Type 1 in accordance with MCHW series 800 Cl.803.
23. Noted to be added to the drawing to advise contractor that once the sub-base materials have been compacted and tested no vehicles are permitted on the compacted sub-base or the materials will require re-compacting and re-testing prior laying of macadam layers.
24. All macadam works shall be in accordance with BS594987 & PD6691All macadam materials shall be to BS EN 13108All granular materials used within the works shall be to SHWAll concrete shall be to BS 8500 All construction materials within 450mm of finishes levels shall be non-frost susceptible All macadam testing including nuclear density testing, sample testing and laying records shall be in accordance with TRfD Section 8.2.5.
25. Kerb haunch to finish 90mm below finished levels to enable footway surface and binder courses to be laid to the required depths.
26. Pavement designs for all new/ widened carriageway areas should be fully in accordance with DMRB standards with a minimum required pavement design life of 40 years.
27. Pavement maintenance designs should be undertaken in accordance with the DMRB for all existing pavement areas within the permanent works, to achieve a renewal of the pavement life to match the 40-year design life of the new pavement areas.
28. Tar investigations and management should be undertaken in accordance with current good practice.
29. The Highway Agreement's Clerk of Works is to be present during construction and CBR testing for inspections.
30. All services/utilities effected by the proposed works shall be lowered or relocated in accordance with NJUG requirements. Shallow services may not be protected with concrete cover slabs.

NOTES:

1. Do not scale from this drawing.
2. All dimensions are in metres unless otherwise stated.
3. Brookbanks consulting ltd has prepared this drawing for the sole use of the client. the drawing may not be relied upon by any other party without the express agreement of the client and Brookbanks consulting ltd. where any data supplied by the client or from other sources has been used, it has been assumed that the information is correct. no responsibility can be accepted by Brookbanks consulting ltd for inaccuracies in the data supplied by any other party. the drawing has been produced based on the assumption that all relevant information has been supplied by those bodies from whom it was requested.
4. No part of this drawing may be copied or duplicated without the express permission of Brookbanks consulting ltd.
5. All dimensions and all levels in metres unless noted otherwise.
6. Any discrepancies noted on site are to be reported to the engineer immediately.
7. Section 278 agreement highway works to carried out in strict accordance with Swindon Borough council's requirements.
8. All works within existing public highway, including any temporary works or traffic management measures, are subject to the approval of Swindon Borough Council. when works are required on the public highway, the contractor shall liaise with and obtain all statutory approvals from Swindon Borough Council, before commencing these works. these approvals include, but are not limited to, approval of traffic management measures, issue of works commencement notices, road opening notices, temporary traffic regulation orders etc.
9. All traffic management shall comply with the requirements as set out in chapter 8 of the traffic signs manual. warning signs may be erected outside the indicated boundaries. any obstructions to traffic or pedestrians shall be properly signed and protected with barriers, cones, signs, and lamps.
10. All planting in visibility splays to be agreed and approved by Swindon Borough Council and in all cases no planting to be above 600mm in height above the carriageway. also no obstructions of any kind within the visibility splay areas.
11. All tactile areas to be laid in accordance with detr "guidance on the use of tactile paving surfaces".
12. All traffic signs and road markings are to be in accordance with the 'Traffic Signs Regulations and General Directions 2016'.
13. Any damage caused to existing footways, roads or other third party property to be made good to the county engineers requirements.
14. Temporary works associated with the construction of the works shall be the responsibility of the contractor.

P	Updated with latest lighting layout	CDW	CM	SM	13.11.23
N	Updated following SBC TA4 comment 24/10/23	CM	CM	SM	03.11.23
M	Updated following SBC TA3.1 comment 18/10/23	BM	CM	SM	19.10.23
L	Updated following SBC TA3 comment 12/10	CM	CM	SM	18.10.23
K	Updated following SBC TA2 comment 26/09	CDW	CM	SM	06.10.23
J	Drainage updated following comment	CM	CM	SM	20.09.23
H	Updated following RSA2 comments.	CM	CM	SM	24.08.23
G	Footpath added to southern side	CM	CM	SM	10.07.23
F	Notes Updated	CDW	CM	SM	05.01.23
E	Updated following RSA comment	CM	SM	SM	20.09.22
D	Updated to comments received from SBC June 2022	CDW	SM	RM	01.07.22
C	Footpath North of Roundabout Removed	CM	SM	RM	08.06.22
B	Updated Scale from 1:250 to 1:200	MA	SM	RM	31.03.22
A	Updated S278 Boundary & Drainage Design	CDW	SM	RM	24.02.22
-	First Issue	MP	SM	-	18.01.22

BROOKBANKS

6150 Knights Court, Solihull Parkway, Birmingham, B37 7WY
T +44 (0)203 958 5400 E mail@brookbanks.com
W brookbanks.com

Swindon EDAG

Swindon EDA

Thornhill Road Finishes Plan SBC TA S1055

Status		Status Date
Approval		JAN' 2022
Drawn	**Checked**	**Date**
MP	SM	18.01.22
Scale	**Number**	**Rev**
1:500	1335/HL/56/102	P

0 10 20 30 40 50
METRES

UNTIL TECHNICAL APPROVAL HAS BEEN OBTAINED FROM THE RELEVANT LOCAL AUTHORITIES, IT SHOULD BE UNDERSTOOD THAT ALL DRAWINGS ARE ISSUED AS PRELIMINARY AND NOT FOR CONSTRUCTION. SHOULD THE CONTRACTOR COMMENCE SITE WORK PRIOR TO APPROVAL BEING GIVEN, IT IS ENTIRELY AT HIS OWN RISK.

© Brookbanks Consulting Limited 2023

P:\1335\CAD\BCL\Current Drawings\S278-Thornhill Road\1335-HL-056-102P Finishes Plan.dwg