Original Drawing Size A1

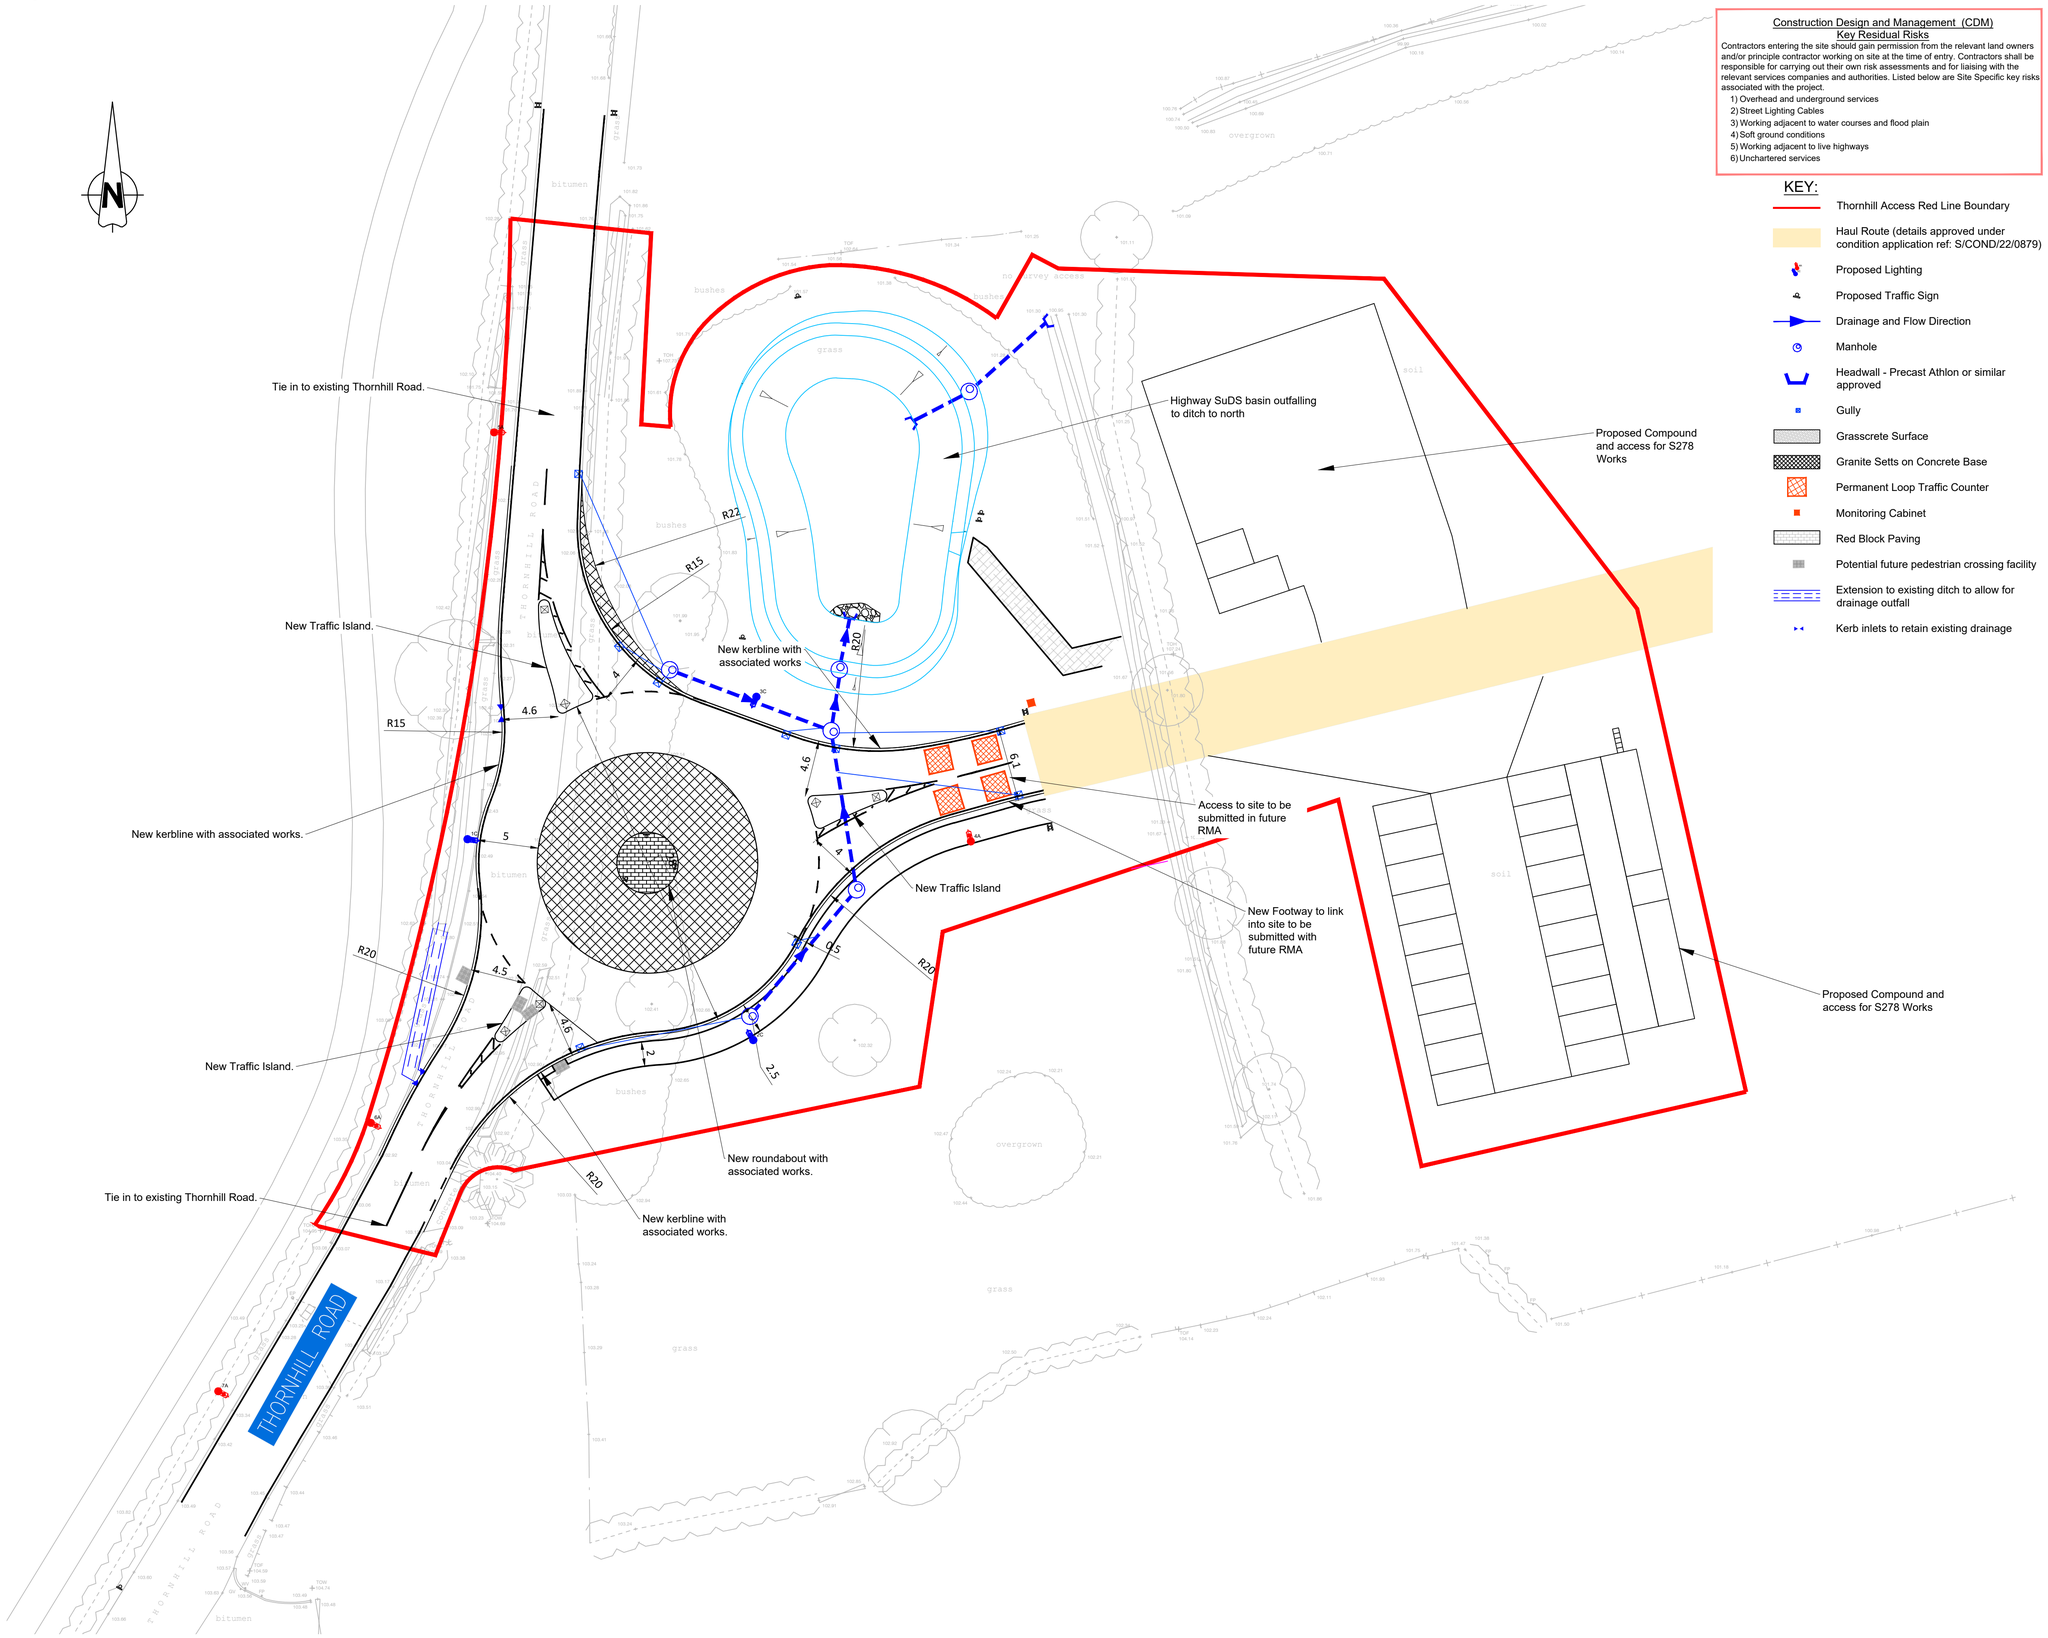

Construction Design and Management (CDM) Key Residual Risks

Contractors entering the site should gain permission from the relevant land owners and/or principle contractor working on site at the time of entry. Contractors shall be responsible for carrying out their own risk assessments and for liaising with the relevant services companies and authorities. Listed below are Site Specific key risks associated with the project.

1) Overhead and underground services
2) Street Lighting Cables
3) Working adjacent to water courses and flood plain
4) Soft ground conditions
5) Working adjacent to live highways
6) Unchartered services

KEY:

- Thornhill Access Red Line Boundary
- Haul Route (details approved under condition application ref: S/COND/22/0879)
- Proposed Lighting
- Proposed Traffic Sign
- Drainage and Flow Direction
- Manhole
- Headwall - Precast Athlon or similar approved
- Gully
- Grasscrete Surface
- Granite Setts on Concrete Base
- Permanent Loop Traffic Counter
- Monitoring Cabinet
- Red Block Paving
- Potential future pedestrian crossing facility
- Extension to existing ditch to allow for drainage outfall
- Kerb inlets to retain existing drainage

NOTES:

1. Do not scale from this drawing.
2. All dimensions are in metres unless otherwise stated.
3. Brookbanks consulting ltd has prepared this drawing for the sole use of the client. the drawing may not be relied upon by any other party without the express agreement of the client and Brookbanks consulting ltd. where any data supplied by the client or from other sources has been used, it has been assumed that the information is correct. no responsibility can be accepted by Brookbanks consulting ltd for inaccuracies in the data supplied by any other party. the drawing has been produced based on the assumption that all relevant information has been supplied by those bodies from whom it was requested.
4. No part of this drawing may be copied or duplicated without the express permission of Brookbanks consulting ltd.
5. All dimensions and all levels in metres unless noted otherwise.
6. Any discrepancies noted on site are to be reported to the engineer immediately.
7. Section 278 agreement highway works to carried out in strict accordance with Swindon Borough council's requirements.
8. All works within existing public highway, including any temporary works or traffic management measures, are subject to the approval of Swindon Borough Council. when works are required on the public highway, the contractor shall liaise with and obtain all statutory approvals from Swindon Borough Council, before commencing these works. these approvals include, but are not limited to, approval of traffic management measures, issue of works commencement notices, road opening notices, temporary traffic regulation orders etc.
9. All traffic management shall comply with the requirements as set out in chapter 8 of the traffic signs manual. warning signs may be erected outside the indicated boundaries. any obstructions to traffic or pedestrians shall be properly signed and protected with barriers, cones, signs, and lamps.
10. All planting in visibility splays to be agreed and approved by Swindon Borough Council and in all cases no planting to be above 600mm in height above the carriageway. also no obstructions of any kind within the visibility splay areas.
11. All tactile areas to be laid in accordance with detr "guidance on the use of tactile paving surfaces".
12. All traffic signs and road markings are to be in accordance with the "Traffic Signs Regulations and General Directions 2016'.
13. Any damage caused to existing footways, roads or other third party property to be made good to the county engineers requirements.
14. Temporary works associated with the construction of the works shall be the responsibility of the contractor.
15. The Highway Agreement's Clerk of works is to be present during construction and CBR testing for inspections.

M	Condition approval added to haul route key	CM	CM	SM	14.12.23
L	Haul route added to drawing	CDW	CM	SM	13.12.23
K	Updated following DLA request 31.10.23 to relocate compound	CM	CM	SM	01.11.23
J	Drainage updated following comment	CM	CM	SM	20.09.23
H	Updated following RSA2 comments	CM	CM	SM	24.08.23
G	Footpath added to southern side	CM	CM	SM	10.07.23
F	New note added and geometry lines turned to black	CDW	CM	SM	05.01.23
E	Compound updated on plan	TO	CM	SM	27.10.22
D	Updated for SBC submission	CM	SM	SM	01.08.22
C	Updated to comments received from SBC June 2022	CDW	SM	RM	01.07.22
B	Footpath Removed and Layby Updated	CM	SM	RM	27.06.22
A	Updated Scale from 1:250 to 1:200	MA	SM	RM	31.03.22
-	First Issue	MP	MP	SM	02.03.22

BROOKBANKS

6150 Knights Court, Solihull Parkway, Birmingham, B37 7WY
T +44 (0)203 958 5400 E mail@brookbanks.com
W brookbanks.com

Swindon EDAG

Swindon EDA

Thornhill Road Planning Layout SBC TA S1055

Status		Status Date
Approval		MAR' 2022
Drawn	**Checked**	**Date**
MP	SM	02.03.22
Scale	**Number**	**Rev**
1:250	1335/HL/56/105	M

0 5 10 15 20 25
METRES

UNTIL TECHNICAL APPROVAL HAS BEEN OBTAINED FROM THE RELEVANT LOCAL AUTHORITIES, IT SHOULD BE UNDERSTOOD THAT ALL DRAWINGS ARE ISSUED AS PRELIMINARY AND NOT FOR CONSTRUCTION. SHOULD THE CONTRACTOR COMMENCE SITE WORK PRIOR TO APPROVAL BEING GIVEN, IT IS ENTIRELY AT HIS OWN RISK.

© Brookbanks Consulting Limited 2023

C:\Users\ChristianMcArdle\OneDrive - Brookbanks Consulting Ltd\Documents - Projects\1335\CAD\BCL\Current Drawings\S278-Thornhill Road\1335-HL-056-105M Planning Layout.dwg